




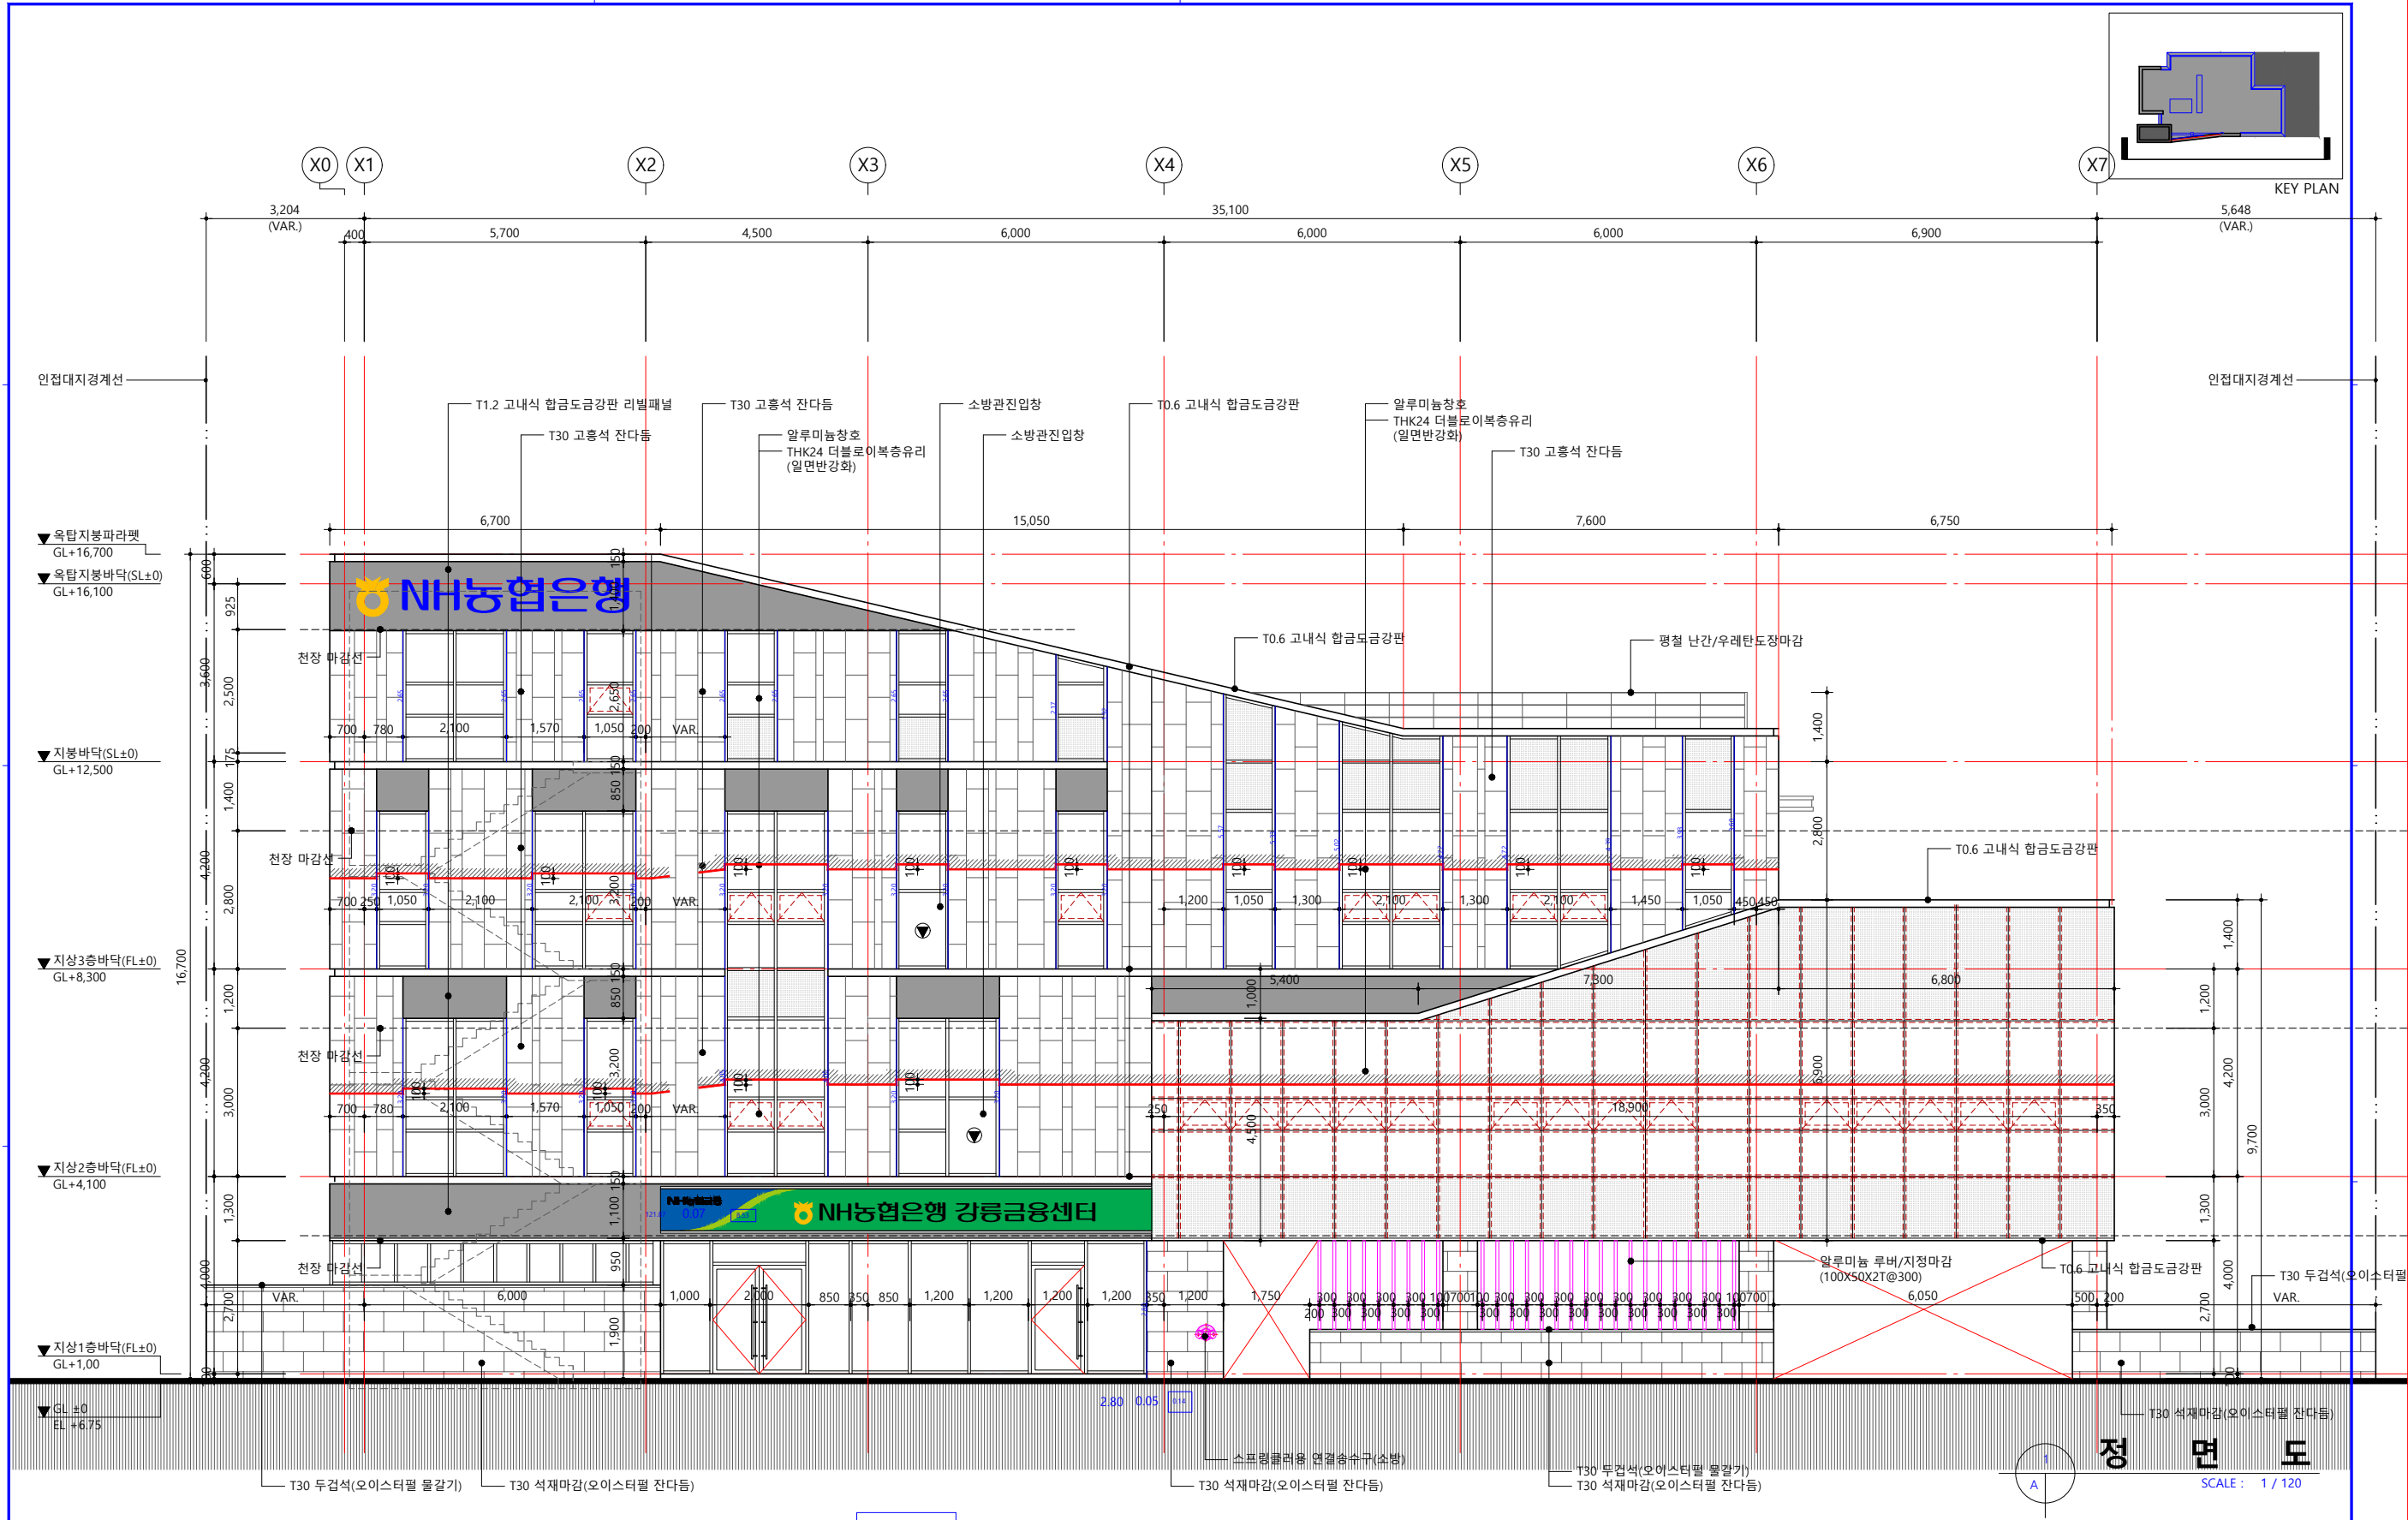

건축주 CLIENT	설계사무소 DESIGN OFFICE Tel. 02-6014-2137 / Fax. 02-6014-2138 Email : archjian21@naver.com	NOTE. 8.67 10.72 1.05 11.26	△ △ △ No. Date Revision Description Chkd.	설계명 PROJECT TITLE 설계단계 CONSULTANT 건축구조 : (주)탐앤지니어링 토목 : (주)제일기초이엔씨 전기/통신/소방 : (주)하랑엔지니어링	프로젝트번호 PROJECT CODE JP25-0001 승인 APPROVED BY 황진희 00.00.00 전문분야 SUBJECT 건축 검토 CHECKED BY 최용규 00.00.00 설계단계 DESIGN PHASE 실시설계(변경) 작성 Drawn By 신가영 00.00.00	도면명 DRAWING TITLE 정 면 도 도면번호 DRAWING NO. A32-001 출척 SCALE A1: 1/60 A3: 1/120 도면번호 SHEET NO. 000 REV. No. △
---------------------------------------	---	--	---	---	--	--

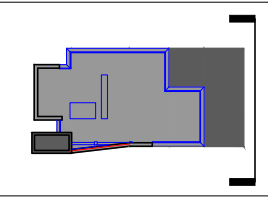


KEY PLAN

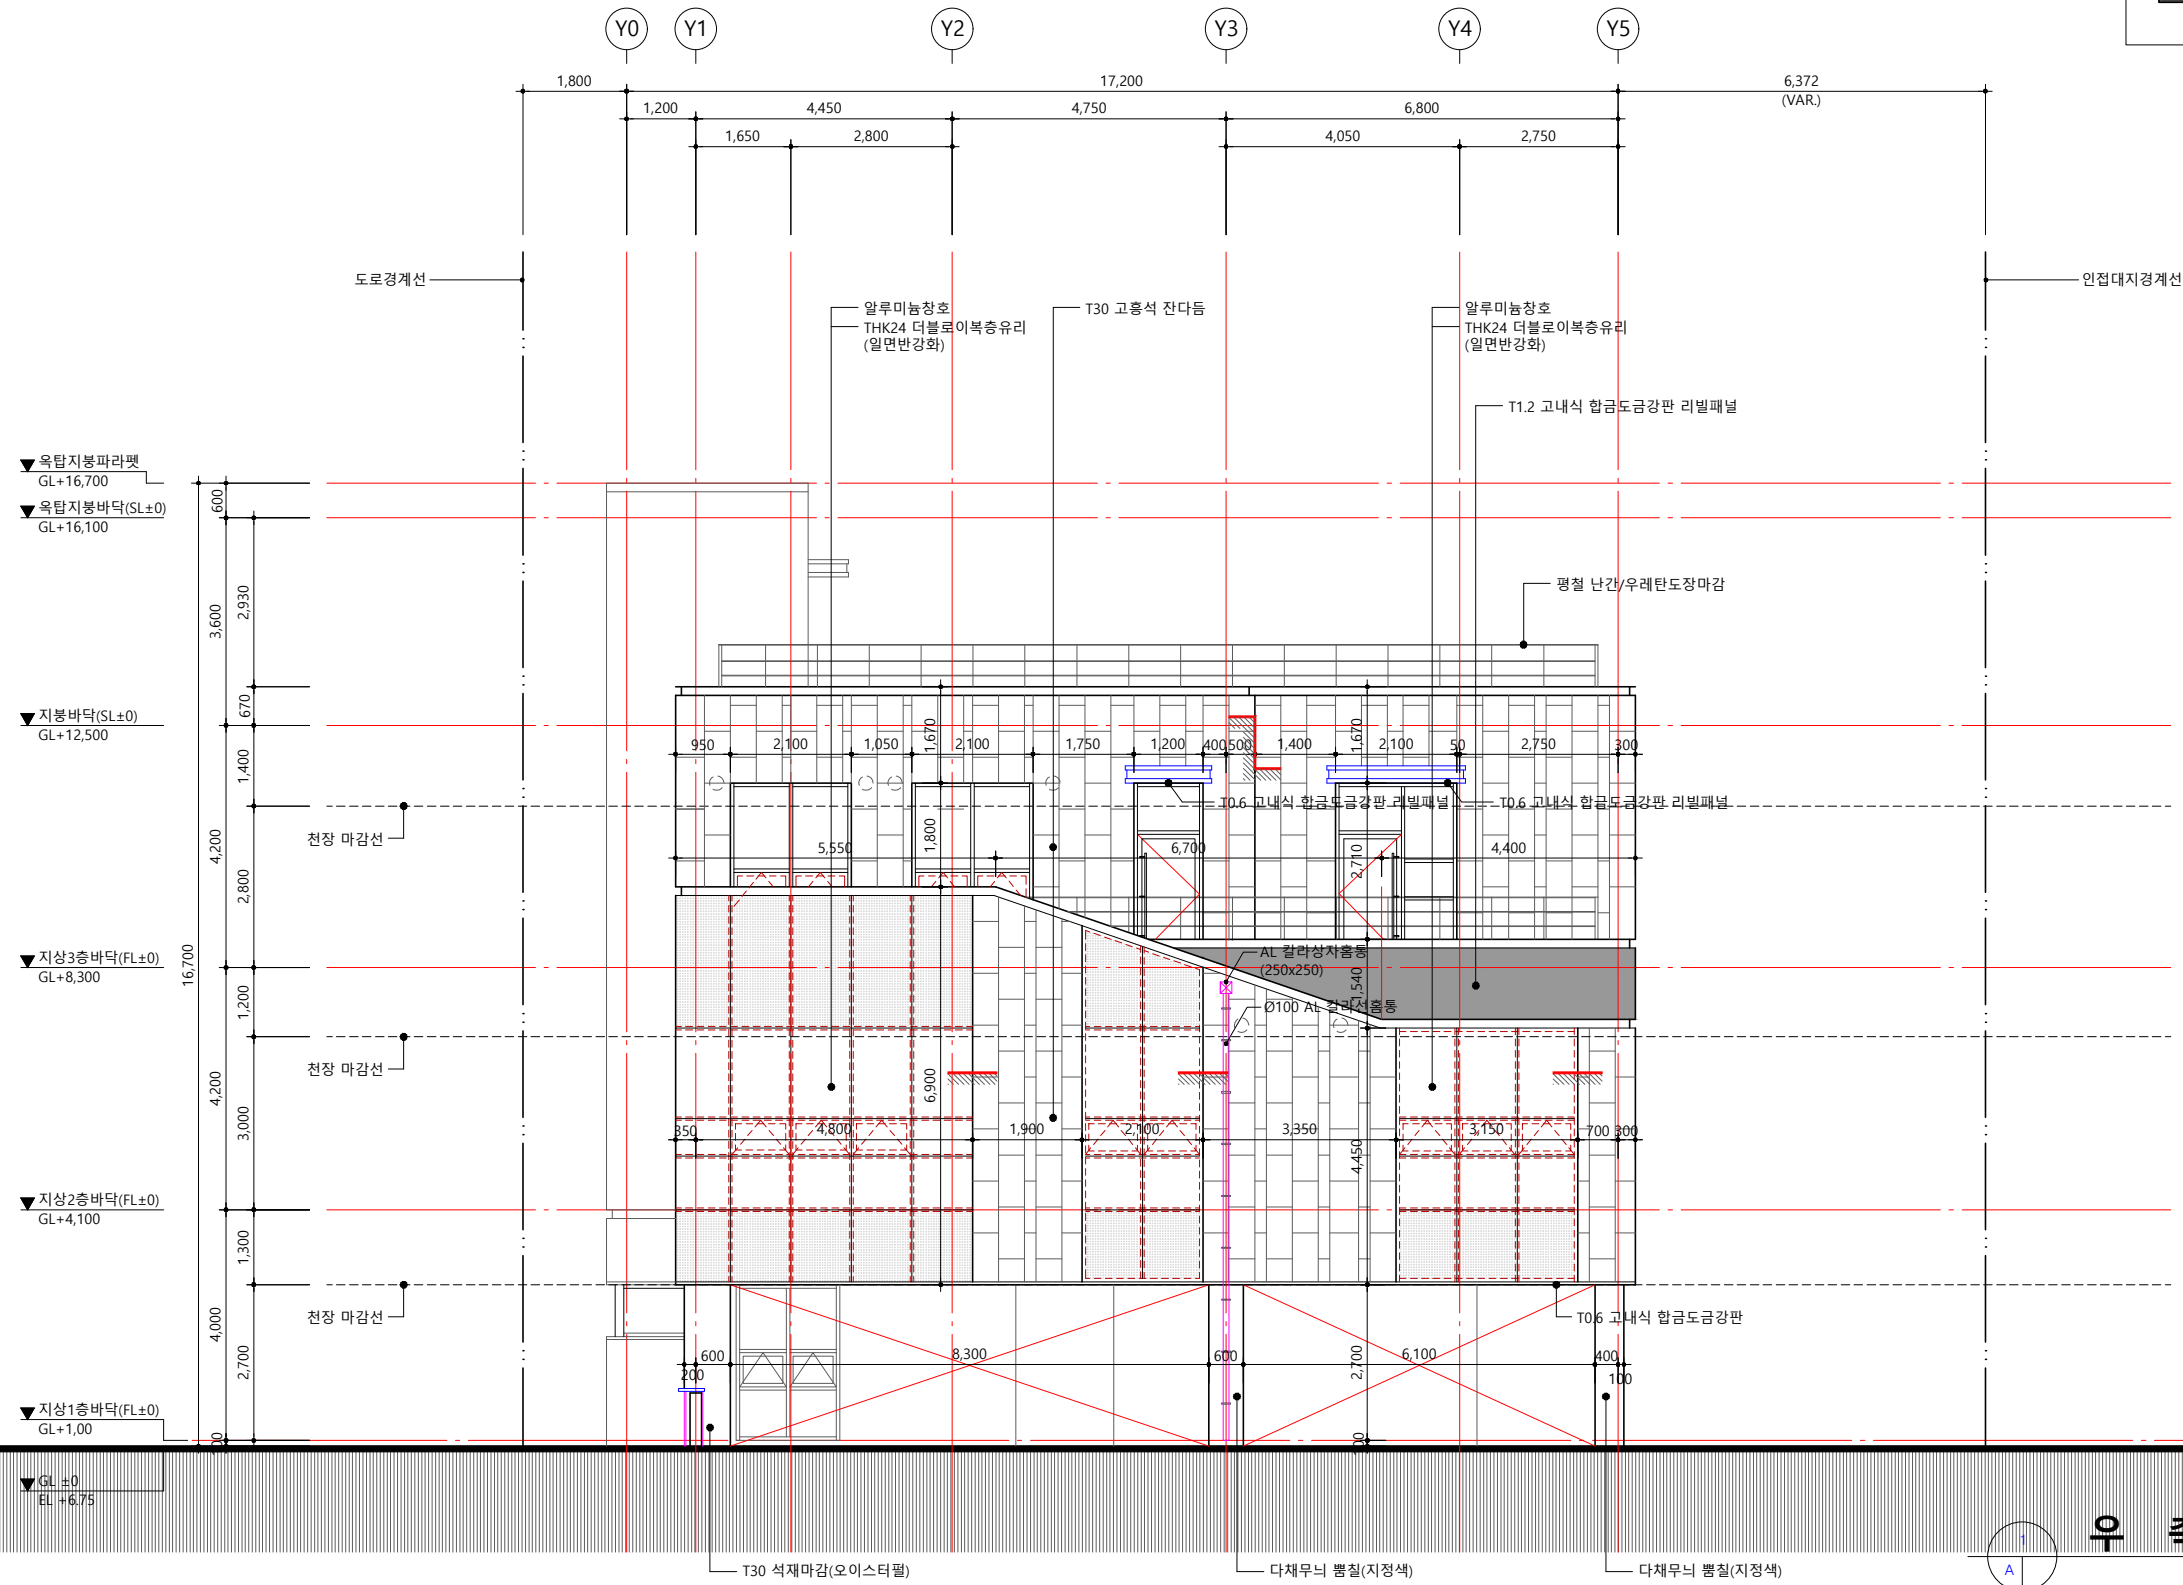

우 측 면 도
SCALE : 1 / 120

건축주 CLIENT	설계사무소 DESIGN OFFICE	 지안21 Tel. 02-6014-2137 / Fax. 02-6014-2138 Email : archjian21@naver.com	NOTE.					설계명 PROJECT TITLE	 NH농협은행 강릉 금융센터 신축공사	프로젝트번호 PROJECT CODE		승인 APPROVED BY		도면명 DRAWING TITLE						
										JP25-0001	황진희 00.00.00									
										협력설계 CONSULTANT	건축구조 : (주)탐앤지니어링 토목 : (주) 제일기초이엔씨 전기/통신/소방 : (주)하랑엔지니어링	검토 CHECKED BY		검토 Drawn By		축척 SCALE	A1: 1/60		도면번호 DRAWING NO. A32-002	
												최용규 00.00.00	최용규							
												No.	Date	Revision Description	Chkd.		설계단계 DESIGN PHASE		작성 Drawn By	
								실시설계(변경)		신가영 00.00.00										

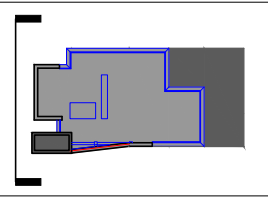


KEY PLAN




좌 측 면 도
SCALE : 1 / 120



건축주 CLIENT NH농협은행 (강원본부)	설계사무소 DESIGN OFFICE 지안21 건축사무소 Tel. 02-6014-2137 / Fax. 02-6014-2138 Email : archjian21@naver.com	NOTE.	1.54	설계명 PROJECT TITLE NH농협은행 강릉 금융센터 신축공사 설계/설계 CONSULTANT 건축구조 : (주)탐앤지니어링 토목 : (주)제일기초이엔씨 전기/통신/소방 : (주)하랑엔지니어링	프로젝트번호 PROJECT CODE JP25-0001 설계단계 DESIGN PHASE 실시설계(변경)	승인 APPROVED BY 황진희 00.00.00 검토 CHECKED BY 최용규 00.00.00 작성 Drawn By 신가영 00.00.00 도면명 DRAWING TITLE 좌 측 면 도 도면번호 DRAWING NO. A32-004 일련번호 SHEET NO. 000 REV. No. △
---	--	--------------	-------------	---	--	--

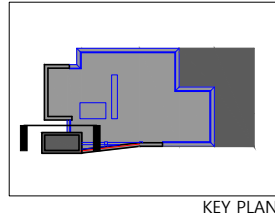

KEY PLAN

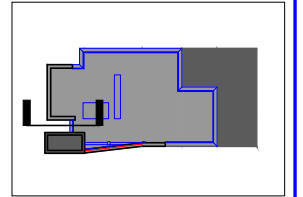


KEY PLAN

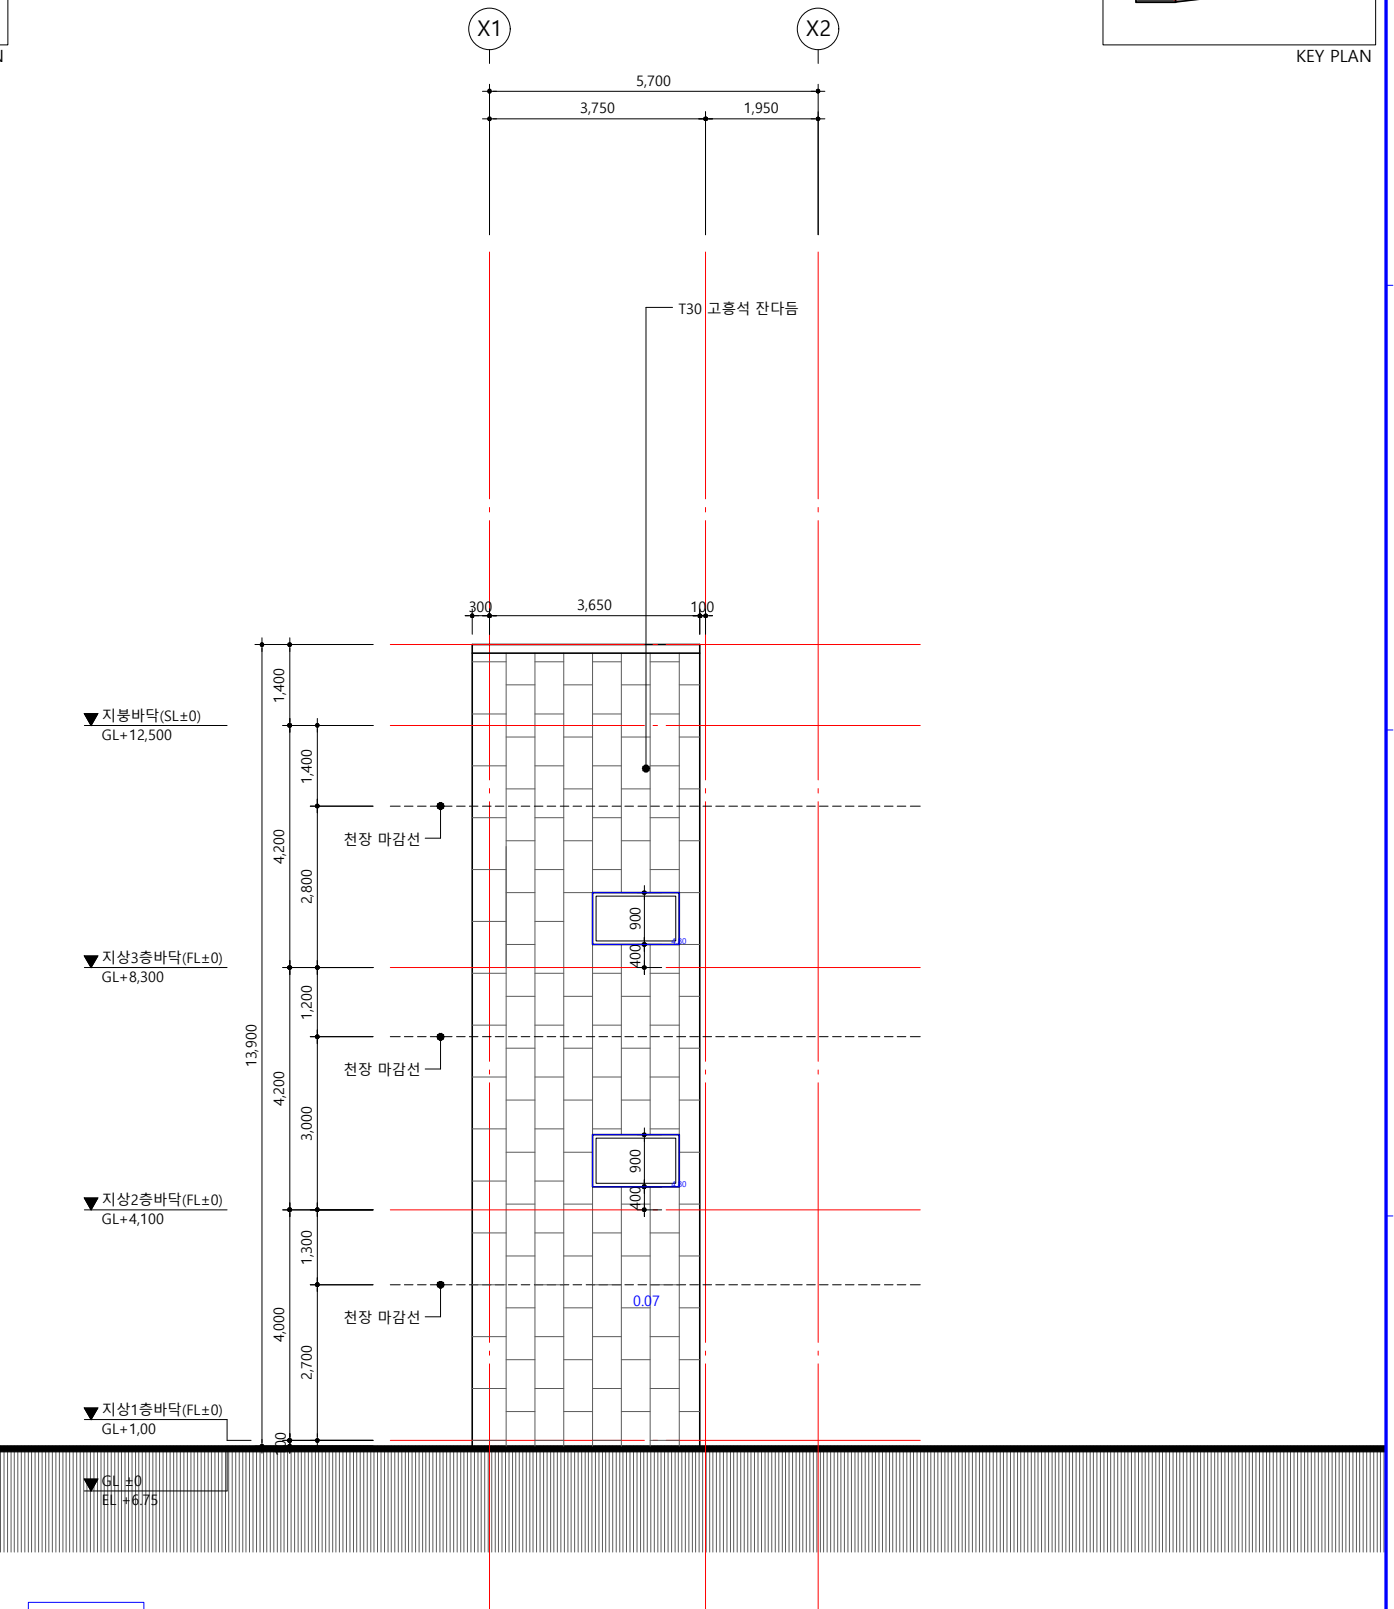
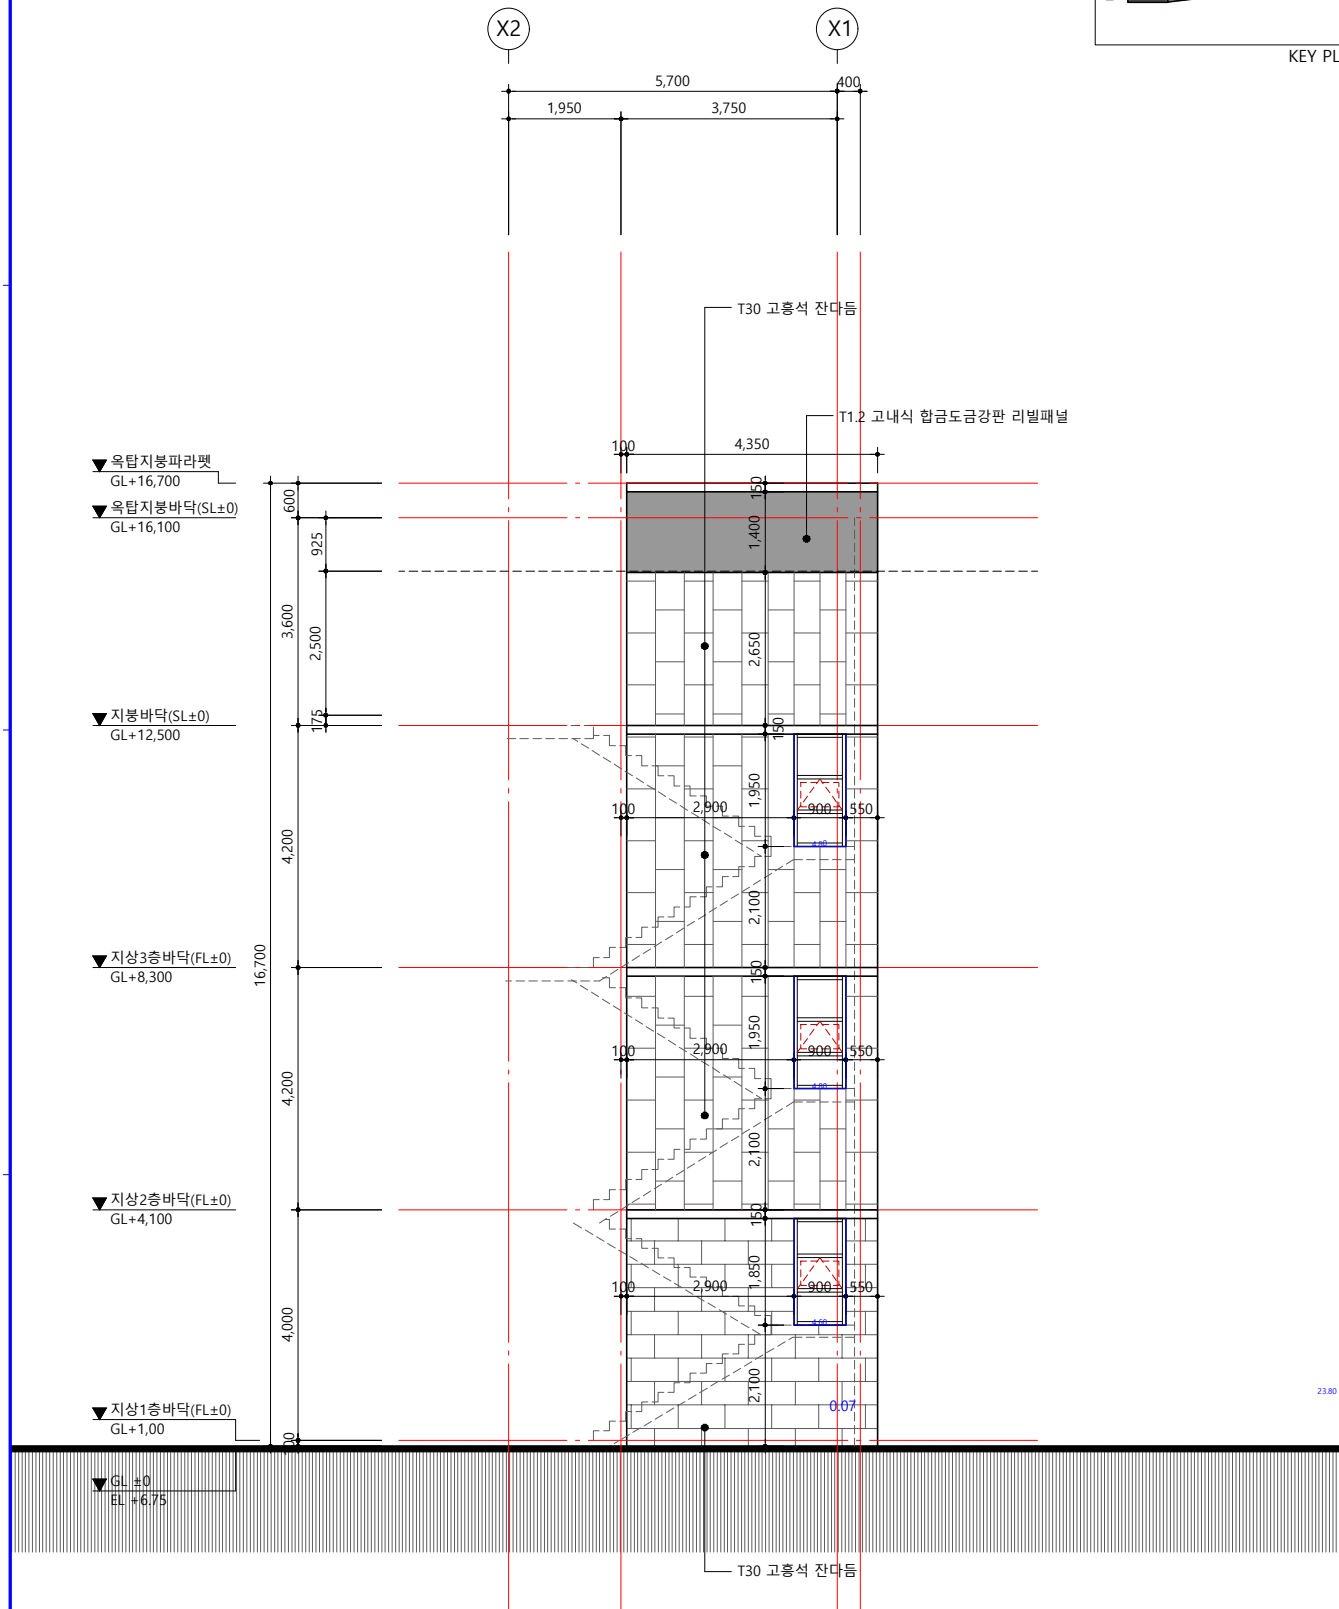



건축주 CLIENT		설계사무소 DESIGN OFFICE	 건축사무소 지안21 Tel. 02-6014-2137 / Fax. 02-6014-2138 Email : archjian21@naver.com	NOTE	1.67	설계명 PROJECT TITLE NH농협은행 강릉 금융센터 신축공사 현역설계 CONSULTANT 건축구조 : (주)탐엔지니어링 토목 : (주) 제일기초이엔씨 전기/통신/소방 : (주)하랑엔지니어링	프로젝트번호 PROJECT CODE JP25-0001 건축 설계단계 DESIGN PHASE 실시설계(변경)	승인 APPROVED BY 황진희 00.00.00 최용규 00.00.00 작성 Drawn By 신가영 00.00.00	도면명 DRAWING TITLE				
									부 분 입 면 도				
									축척 SCALE	도면번호 DRAWING NO.		REV. No.	
										A1: 1/60		A32-005	
										A3: 1/120		일련번호 SHEET NO. 000	


■지상1층

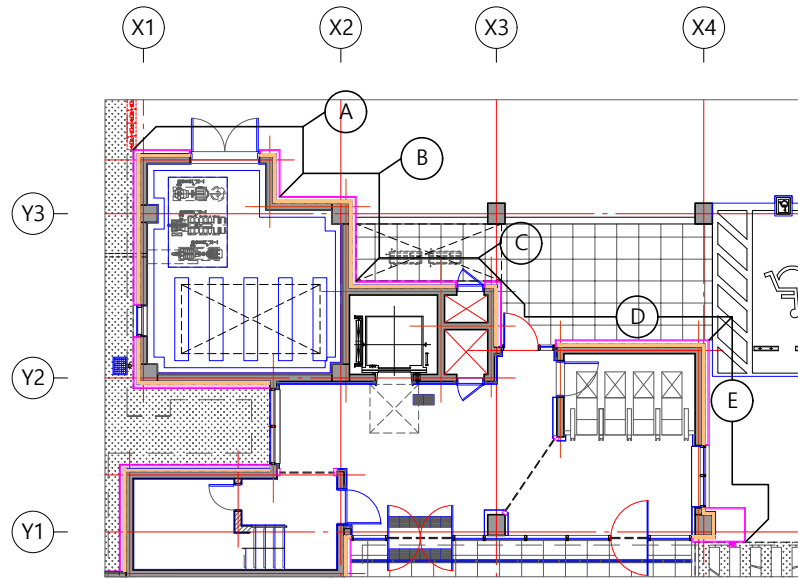

■지상3층

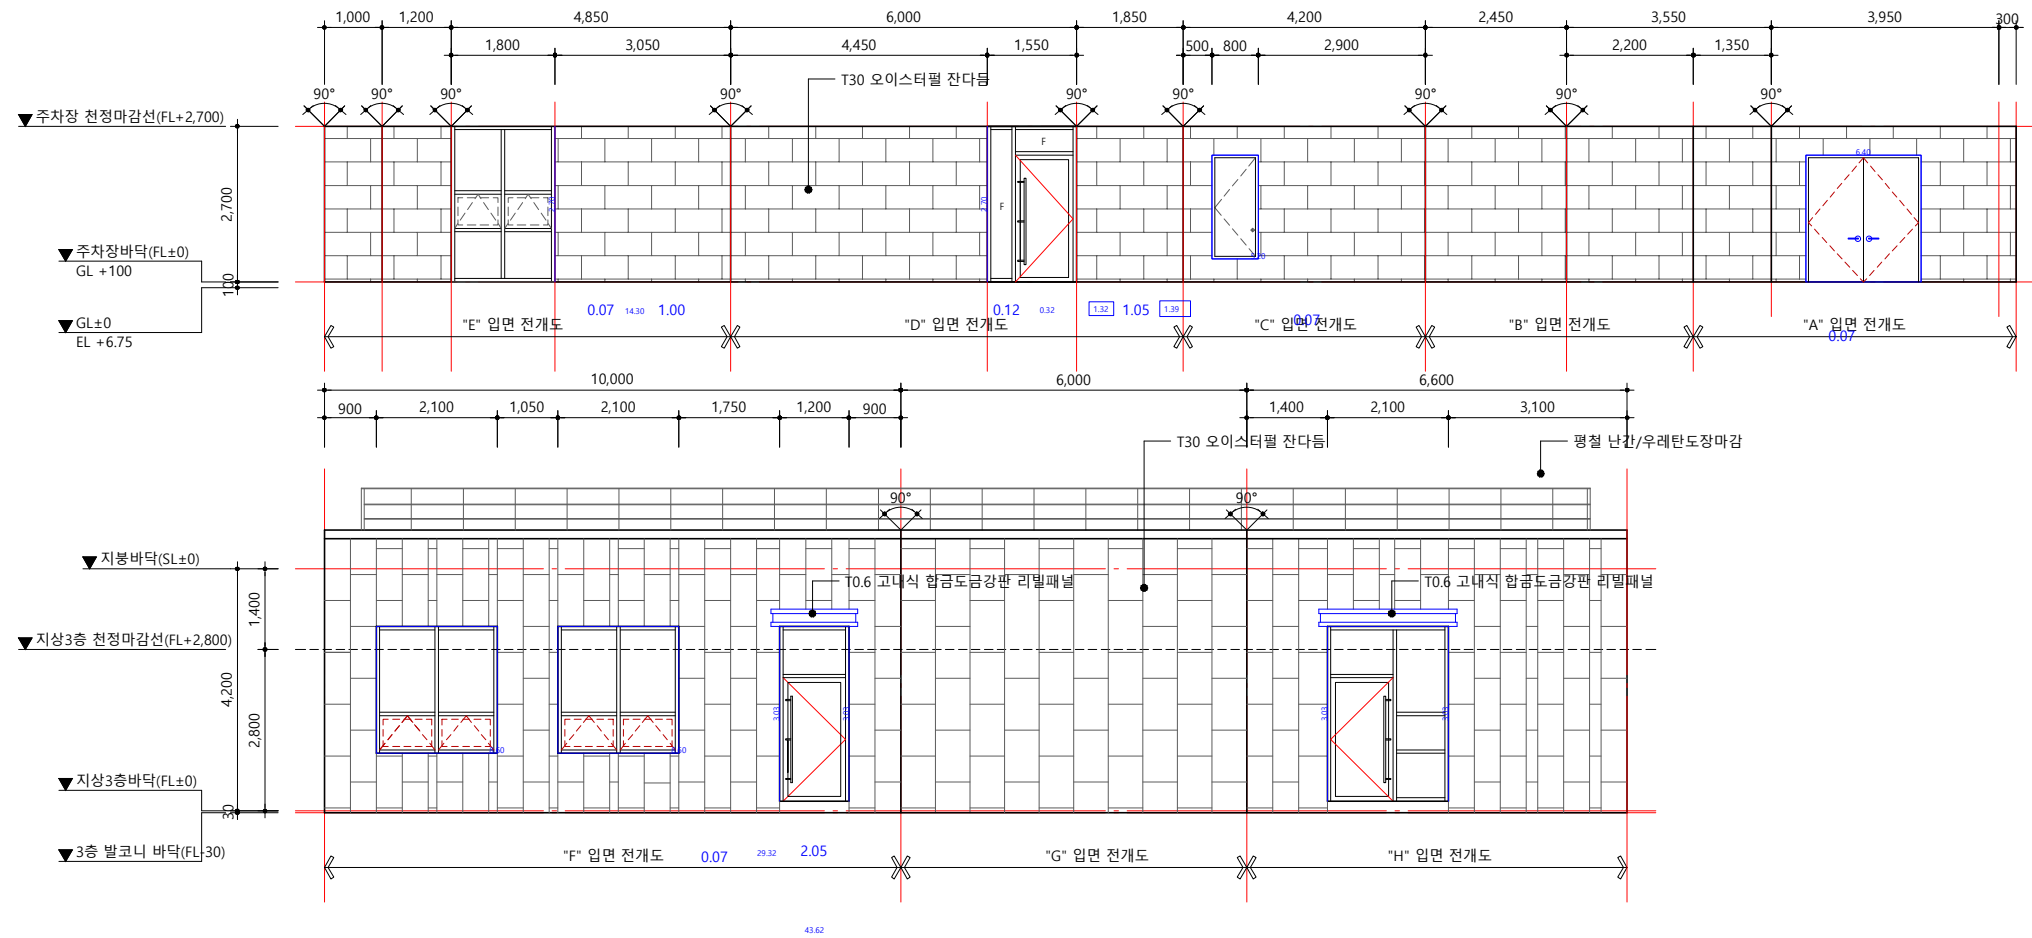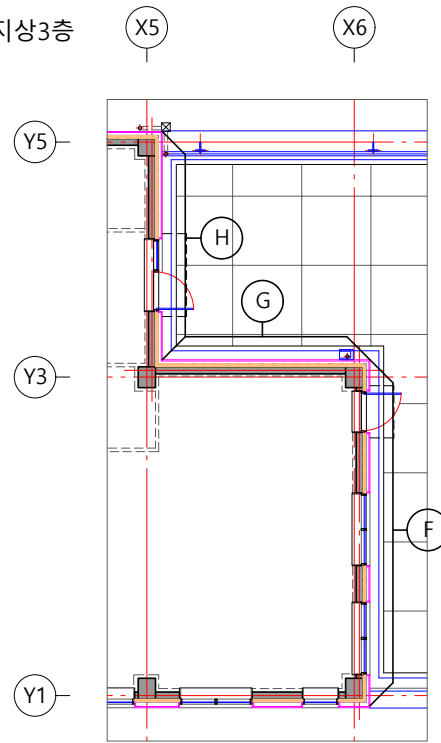

 건축주 CLIENT 	설계사무소 DESIGN OFFICE  지안21 건축사사무소 Tel. 02-6014-2137 / Fax. 02-6014-2138 Email : archjian21@naver.com	NOTE. 3.05	△			설계명 PROJECT TITLE 	프로젝트번호 PROJECT CODE JP25-0001	승인 APPROVED BY 황진희 00.00.00	도면명 DRAWING TITLE 부분 입 면 전 개 도 - 1			
			△				설계단계 CONSULTANT 건축구조 : (주)탐앤지니어링 토목 : (주) 제일기초이엔씨 전기/통신/소방 : (주)하랑엔지니어링	전문분야 SUBJECT 건축	검토 CHECKED BY 최용규 00.00.00	축척 SCALE	A1: 1/60	도면번호 DRAWING NO. A32-006
			△					설계단계 DESIGN PHASE 실시설계(변경)	작성 Drawn By 신가영 00.00.00	A3: 1/120	일련번호 SHEET NO. 000	REV. No. △
			No.	Date	Revision Description			Chkd.				

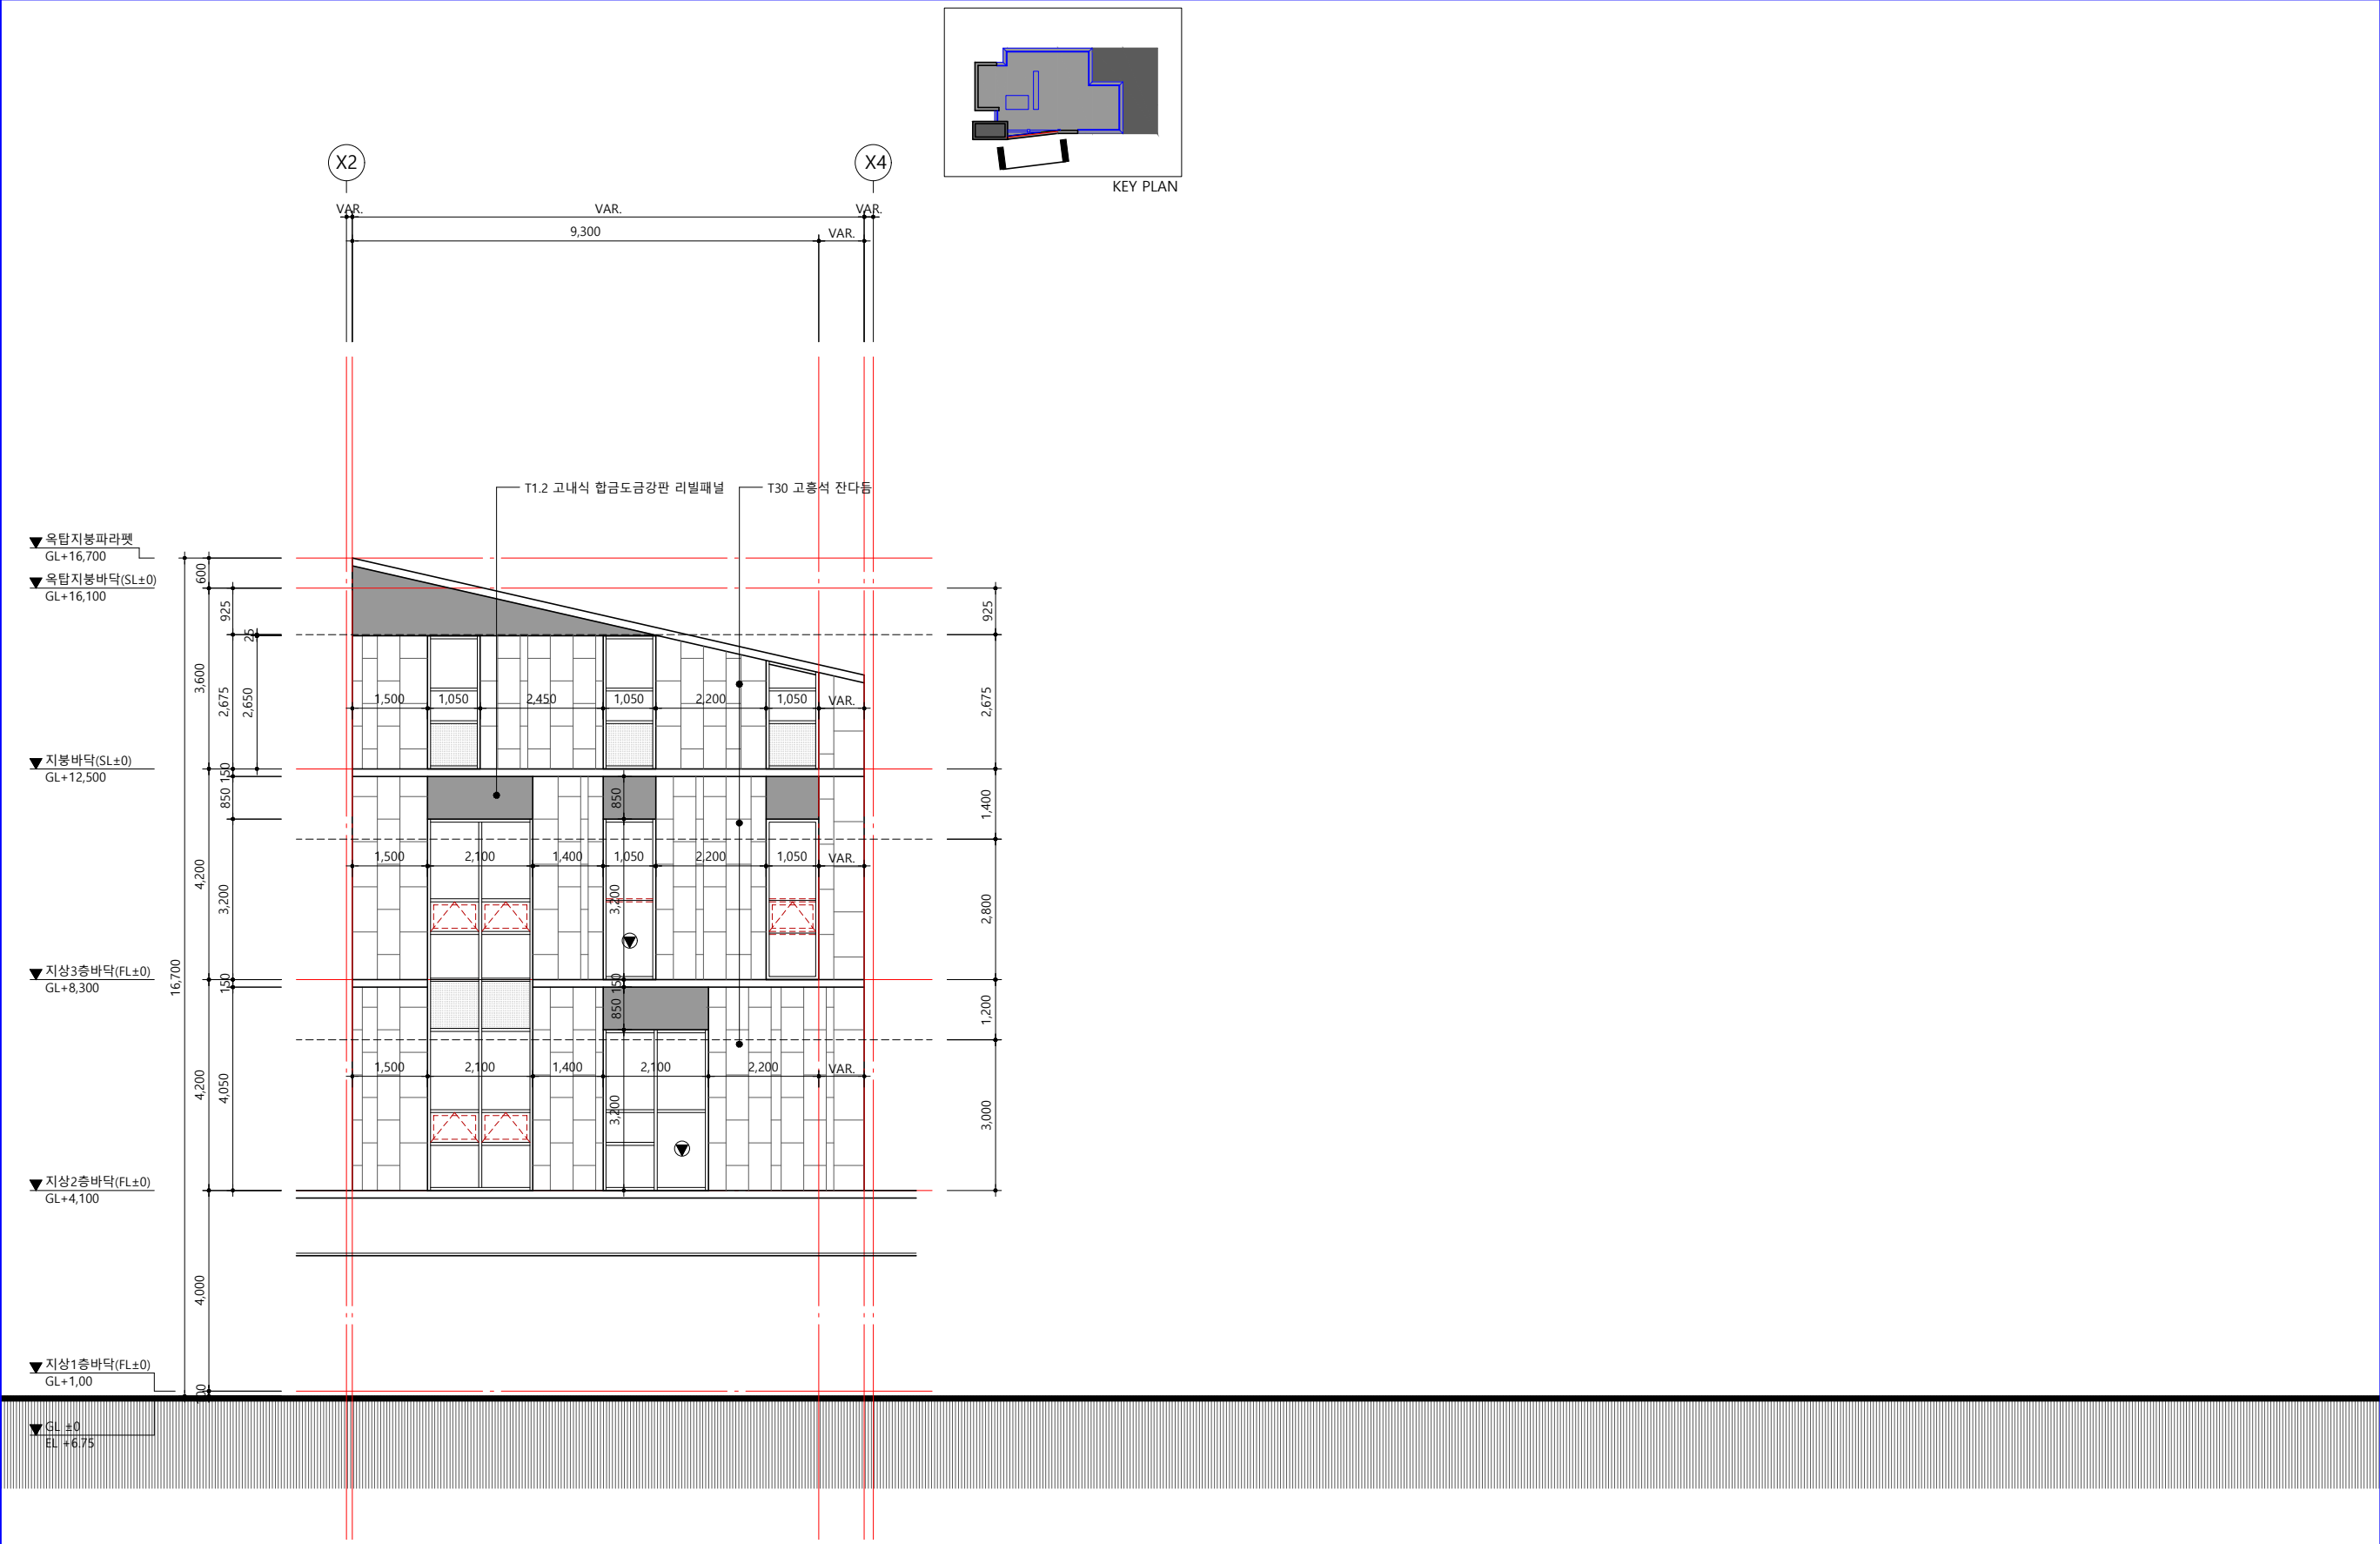

건축주 CLIENT 	설계사무소 DESIGN OFFICE Tel. 02-6014-2137 / Fax. 02-6014-2138 Email : archjian21@naver.com	NOTE.	No. Date Revision Description Chkd.	설계명 PROJECT TITLE 강릉 금융센터 신축공사	프로젝트번호 PROJECT CODE JP25-0001	승인 APPROVED BY 황진희 00.00.00	도면명 DRAWING TITLE 부분 입면 전 개 도 - 2		
				전문분야 SUBJECT 건축	검토 CHECKED BY 최용규 00.00.00	축척 SCALE A1: 1/60	도면번호 DRAWING NO. A32-007		
				협력설계 CONSULTANT 건축구조 : (주)탐앤지니어링 토목 : (주)제일기초이엔씨 전기/통신/소방 : (주)하랑엔지니어링	설계단계 DESIGN PHASE 실시설계(변경)	작성 Drawn By 신가영 00.00.00	일련번호 SHEET NO. 000	REV. No.	
							A3: 1/120		