



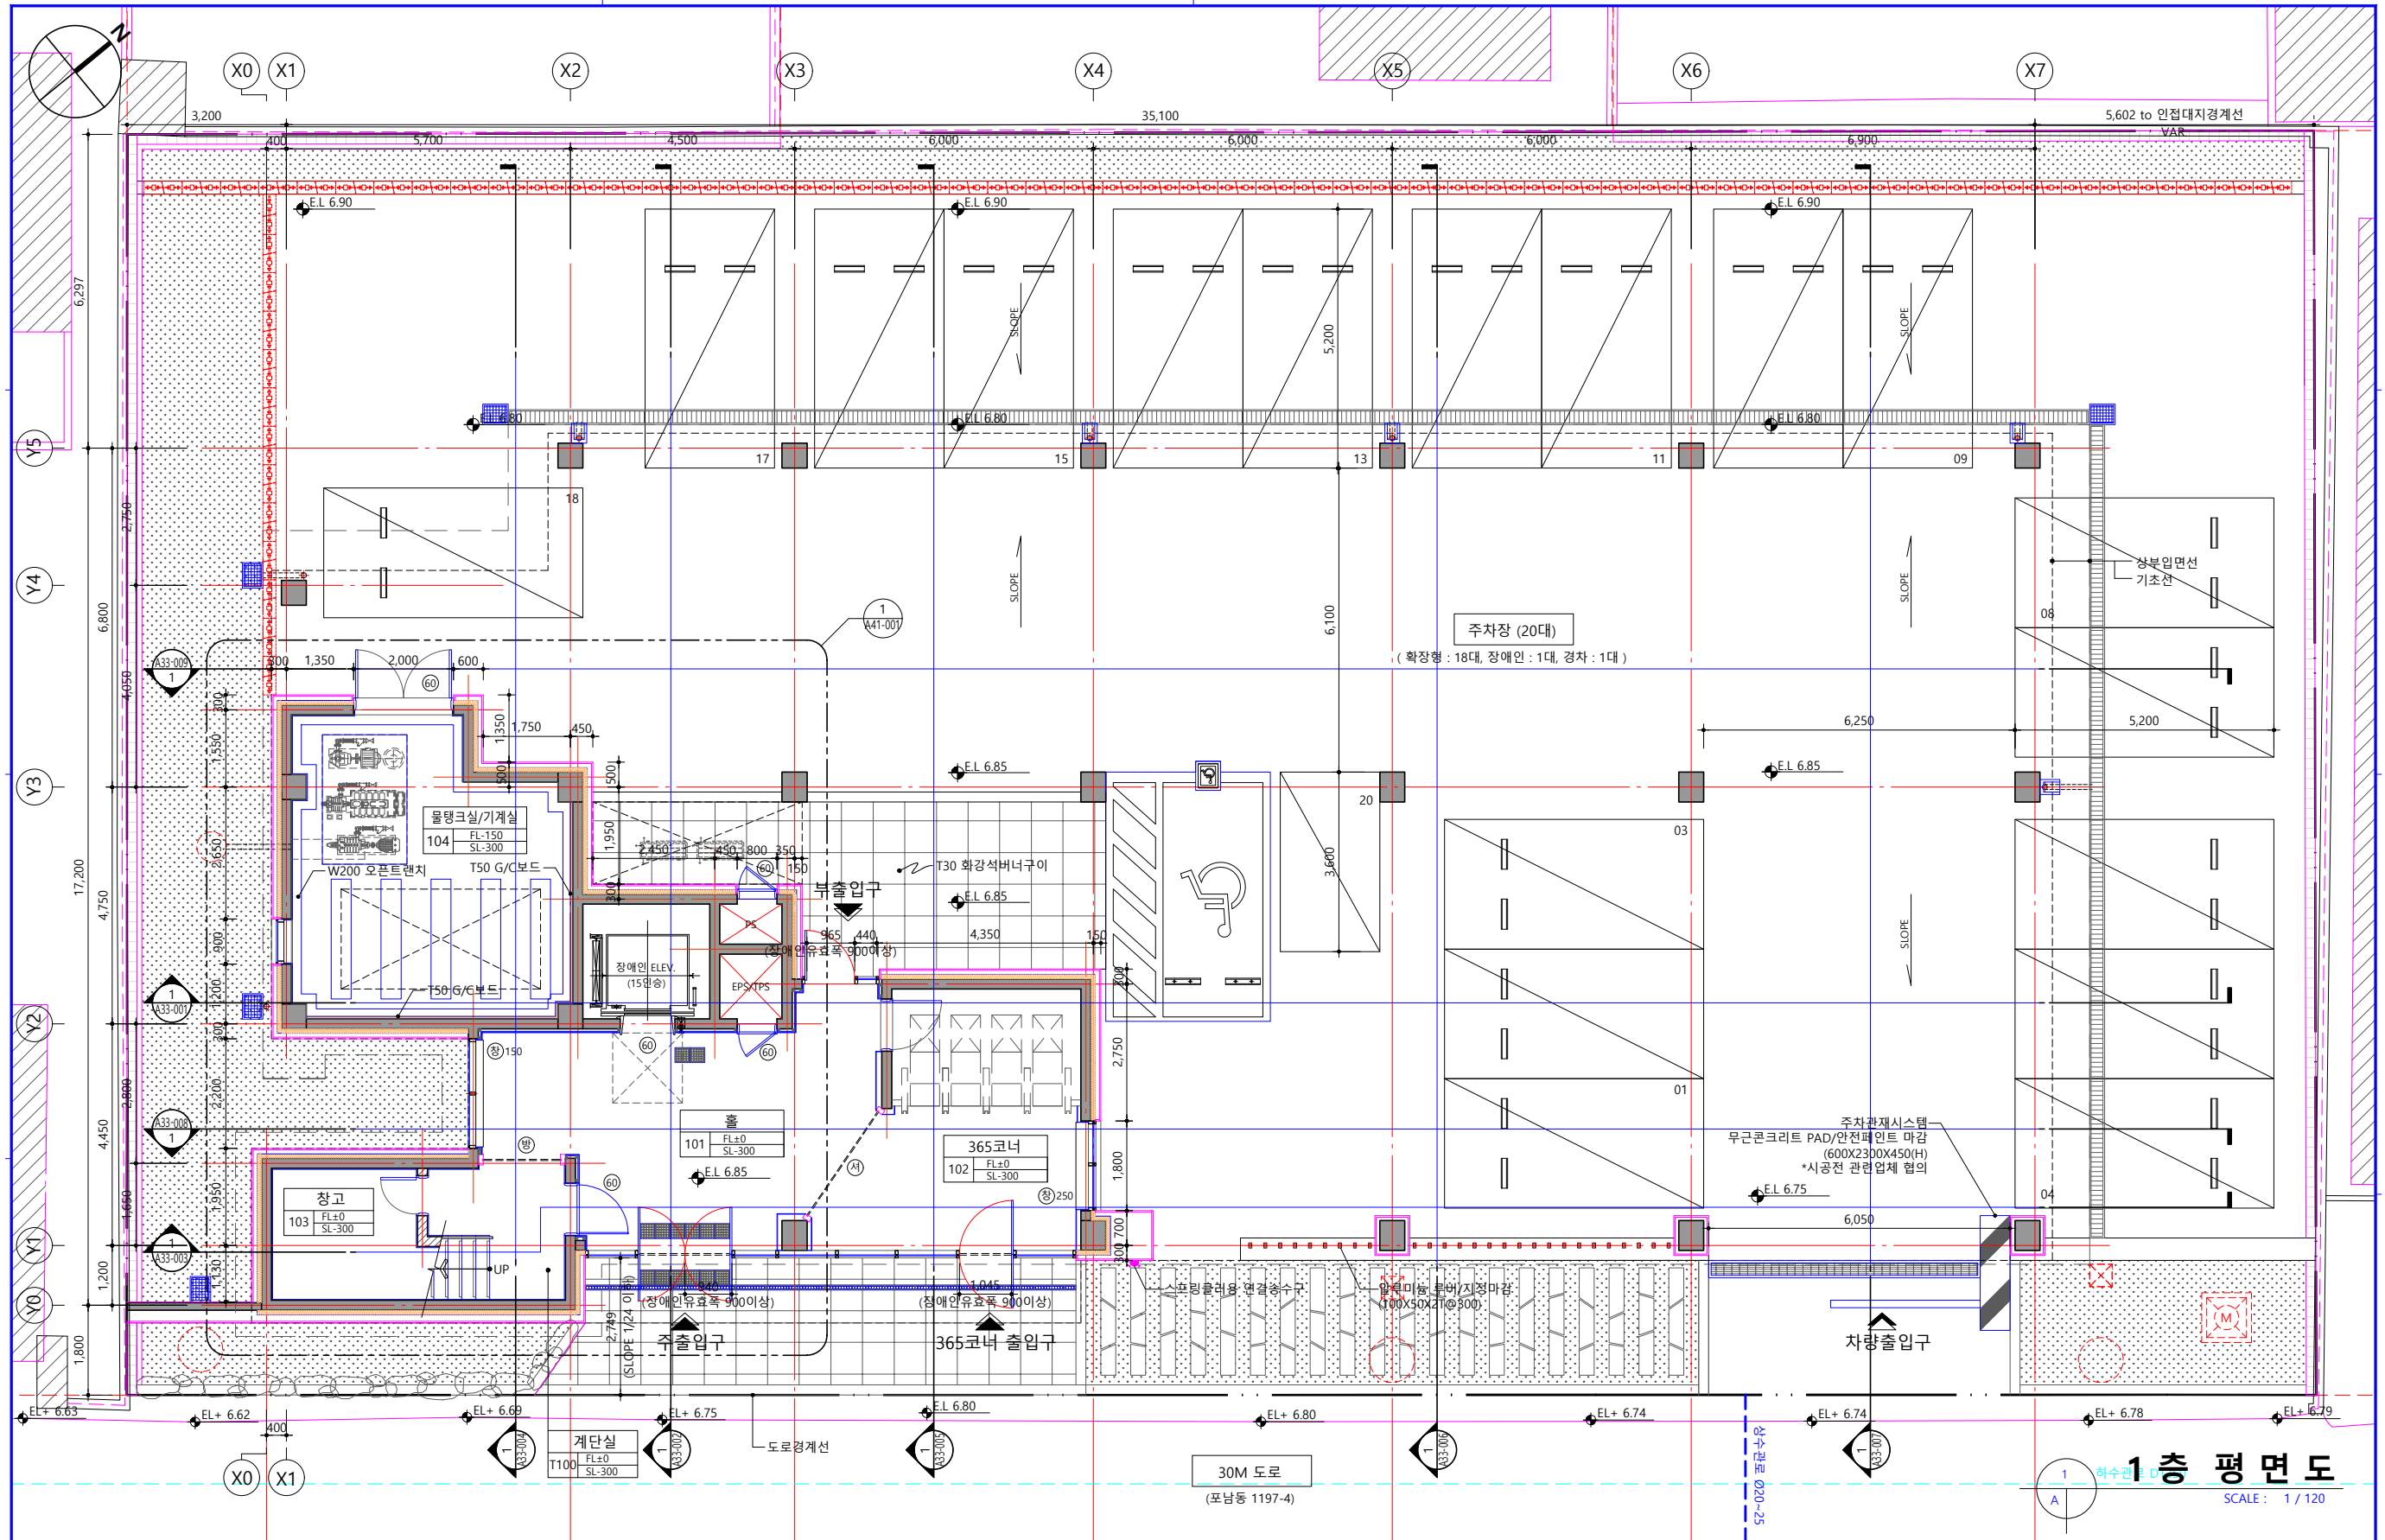


|                                                        |   |                                                     |   |   |   |   |
|--------------------------------------------------------|---|-----------------------------------------------------|---|---|---|---|
| <div>건축주<br/>CLIENT</div> <div>NH농협은행<br/>(강원본부)</div> | <div>설계사무소<br/>DESIGN OFFICE</div> <div>지안21</div> <div>Tel. 02-6014-2137 / Fax. 02-6014-2138<br/>Email : archjian21@naver.com</div> | <div>NOTE.</div> <div>30M 도로<br/>(포남동 1197-4)</div> | <div>설계명<br/>PROJECT TITLE</div> <div>NH농협은행<br/>강릉 금융센터 신축공사</div> <div>설계단위<br/>DESIGN PHASE</div> <div>실시설계(변경)</div> | <div>프로젝트번호<br/>PROJECT CODE</div> <div>JP25-0001</div> <div>설계분야<br/>SUBJECT</div> <div>건축</div> <div>승인<br/>APPROVED BY</div> <div>황진희</div> <div>검토<br/>CHECKED BY</div> <div>최용규</div> <div>작성<br/>Drawn By</div> <div>신가영</div> | <div>도면명<br/>DRAWING TITLE</div> <div>1층 평면도</div> <div>도면번호<br/>DRAWING NO.</div> <div>A31-001</div> <div>도면변호<br/>SHEET NO.</div> <div>000</div> | <div>도면번호<br/>DRAWING NO.</div> <div>A31-001</div> <div>도면변호<br/>SHEET NO.</div> <div>000</div> <div>REV. No.</div> <div>1</div> |
|--------------------------------------------------------|---|-----------------------------------------------------|---|---|---|---|

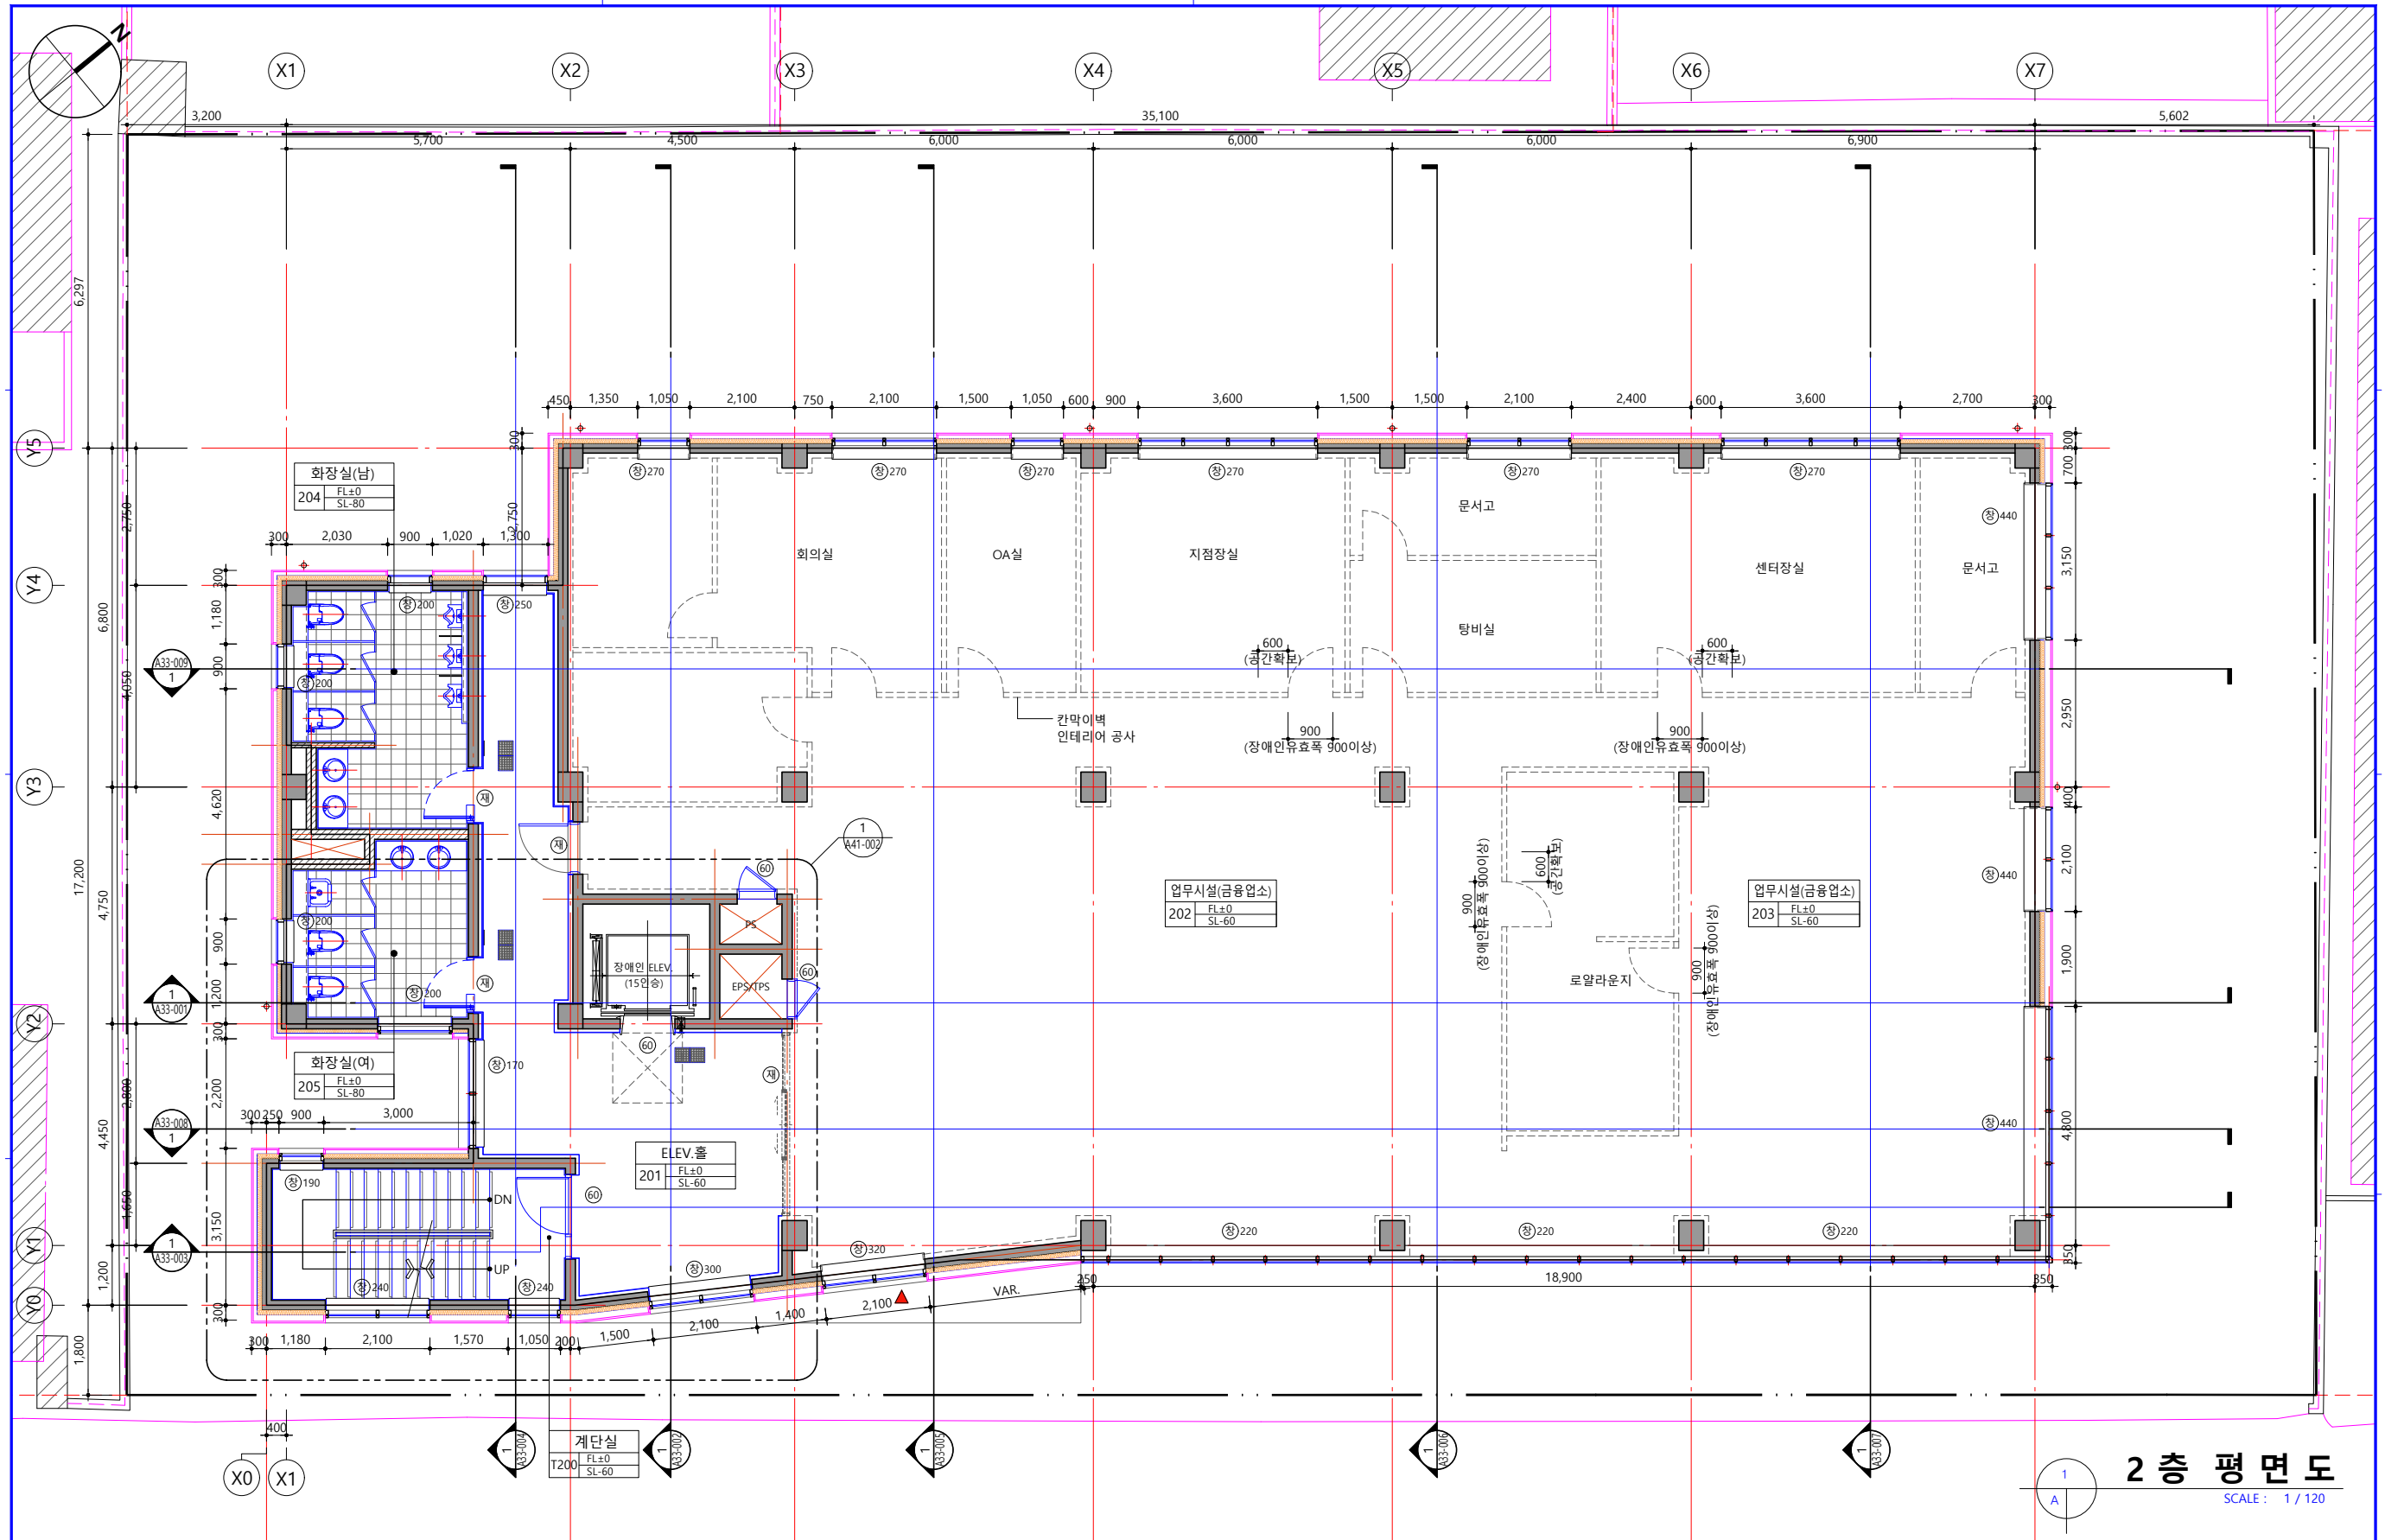


2층 평면도  
SCALE: 1/120

|               |                        |       |   |                      |                     |                                                                     |                   |               |             |           |                             |
|---------------|------------------------|-------|---|----------------------|---------------------|---------------------------------------------------------------------|-------------------|---------------|-------------|-----------|-----------------------------|
| 건축주<br>CLIENT | 설계사무소<br>DESIGN OFFICE | NOTE. | <div><div>△</div><div>△</div><div>△</div><div>△</div><div>No.</div><div>Date</div><div>Revision Description</div><div>Chkd.</div></div> | 설계명<br>PROJECT TITLE | 프로젝트번호 PROJECT CODE | 승인 APPROVED BY                                                      | 도면명 DRAWING TITLE |               |             |           |                             |
|               |                        |       |   | 강릉 금융센터 신축공사         | JP25-0001           | 황진희 00.00.00                                                        | 2 층 평 면 도         |               |             |           |                             |
|               |                        |       |   |                      | 협력설계<br>CONSULTANT  | 건축<br>건축구조 : (주)탐앤지니어링<br>토목 : (주) 제일기초이엔씨<br>전기/통신/소방 : (주)하랑엔지니어링 | 전문분야 SUBJECT      | 검토 CHECKED BY | 축척<br>SCALE | A1: 1/60  | 도면번호 DRAWING NO.<br>A31-002 |
|               |                        |       |   |                      |                     |                                                                     | 설계단계 DESIGN PHASE | 작성 Drawn By   |             | A3: 1/120 | 일련번호 SHEET NO.<br>000       |
|               |                        |       |   |                      | 실시설계(변경)            | 신가영 00.00.00                                                        |                   |               |             |           |                             |

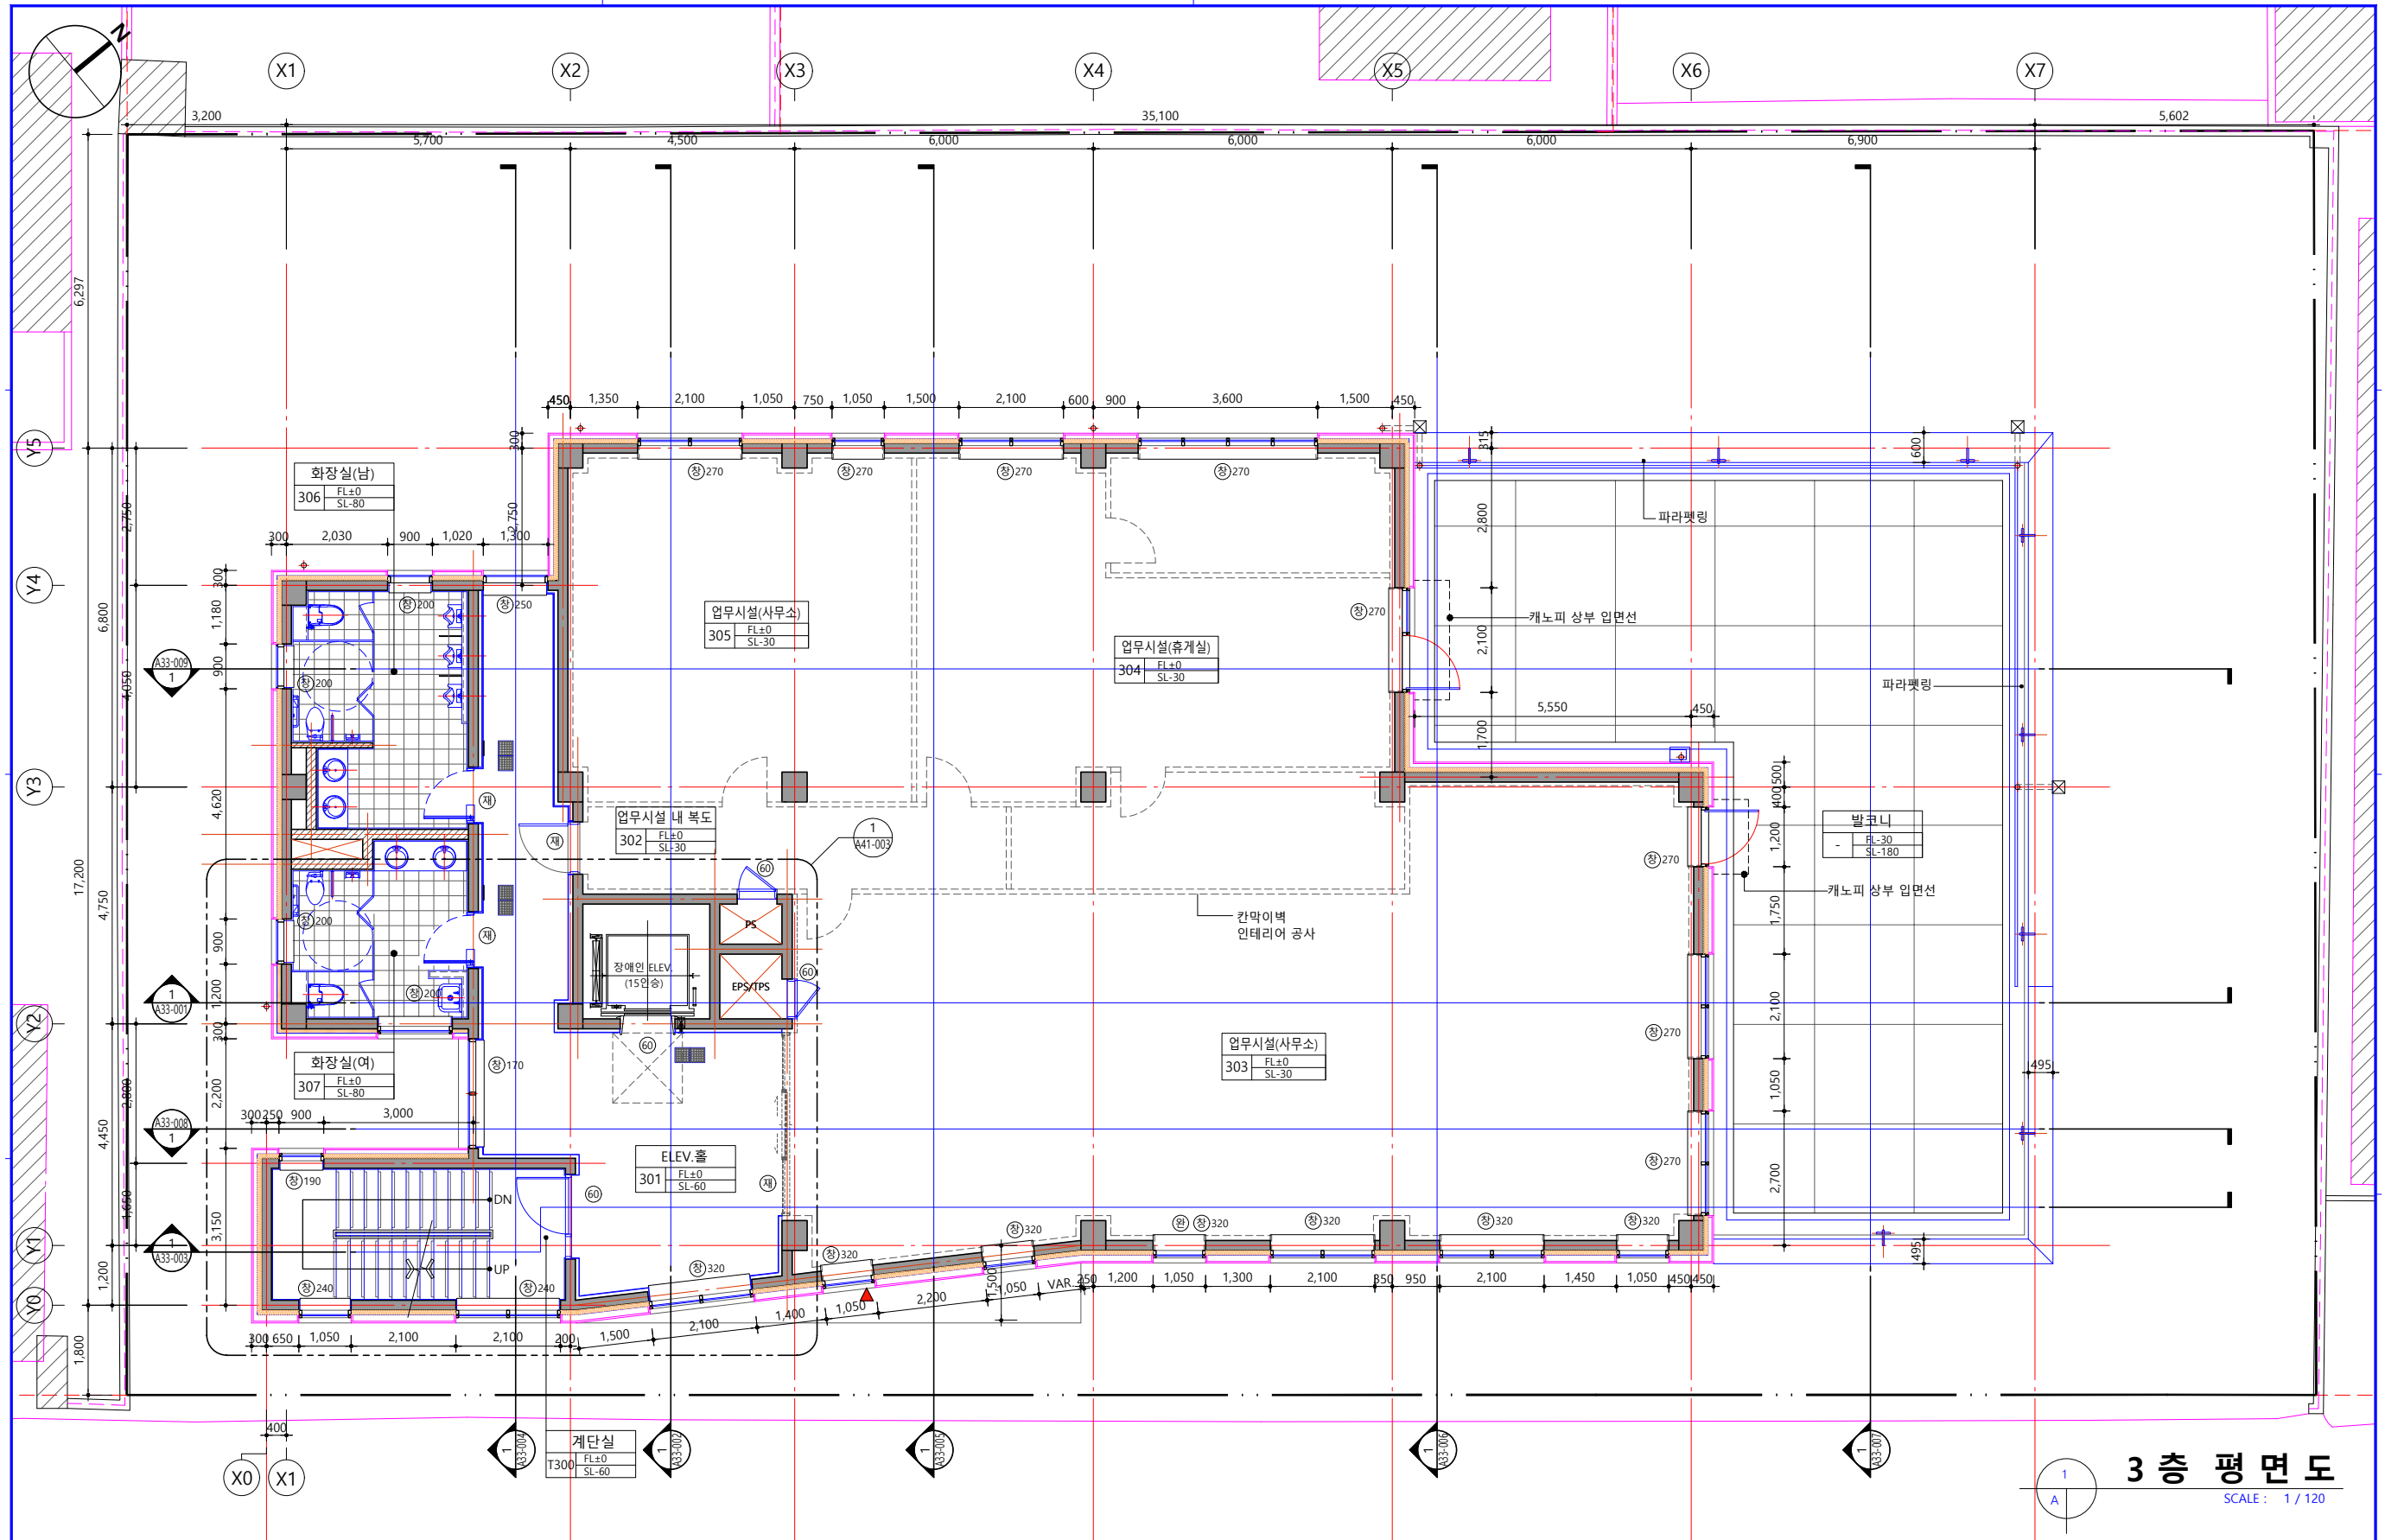

3층 평면도  
SCALE: 1/120

|                                                        |   |   |   |   |   |   |
|--------------------------------------------------------|---|---|---|---|---|---|
| <div>건축주<br/>CLIENT</div> <div>NH농협은행<br/>(강원본부)</div> | <div>설계사무소<br/>DESIGN OFFICE</div> <div>지안21</div> <div>Tel. 02-6014-2137 / Fax. 02-6014-2138<br/>Email: archjian21@naver.com</div> | <div>NOTE.</div> <div><div>1</div><div>2</div><div>3</div><div>4</div><div>100</div></div> | <div>설계명<br/>PROJECT TITLE</div> <div>NH농협은행<br/>강릉 금융센터 신축공사</div> <div>설계단계<br/>CONSULTANT</div> <div>건축구조 : (주)탐앤지니어링<br/>토목 : (주)제일기초이엔씨<br/>전기/통신/소방 : (주)하랑엔지니어링</div> | <div>프로젝트번호 PROJECT CODE</div> <div>JP25-0001</div> <div>설계분야 SUBJECT</div> <div>건축</div> <div>설계단계 DESIGN PHASE</div> <div>실시설계(변경)</div> <div>승인 APPROVED BY</div> <div>황진희 00.00.00</div> <div>검토 CHECKED BY</div> <div>최용규 00.00.00</div> <div>작성 Drawn By</div> <div>신가영 00.00.00</div> | <div>도면명 DRAWING TITLE</div> <div>3층 평면도</div> <div>도면번호 DRAWING NO.</div> <div>A31-003</div> <div>밀련번호 SHEET NO.</div> <div>000</div> <div>REV. No.</div> <div>1</div> | <div>도면명 DRAWING TITLE</div> <div>3층 평면도</div> <div>도면번호 DRAWING NO.</div> <div>A31-003</div> <div>밀련번호 SHEET NO.</div> <div>000</div> <div>REV. No.</div> <div>1</div> |
|--------------------------------------------------------|---|---|---|---|---|---|

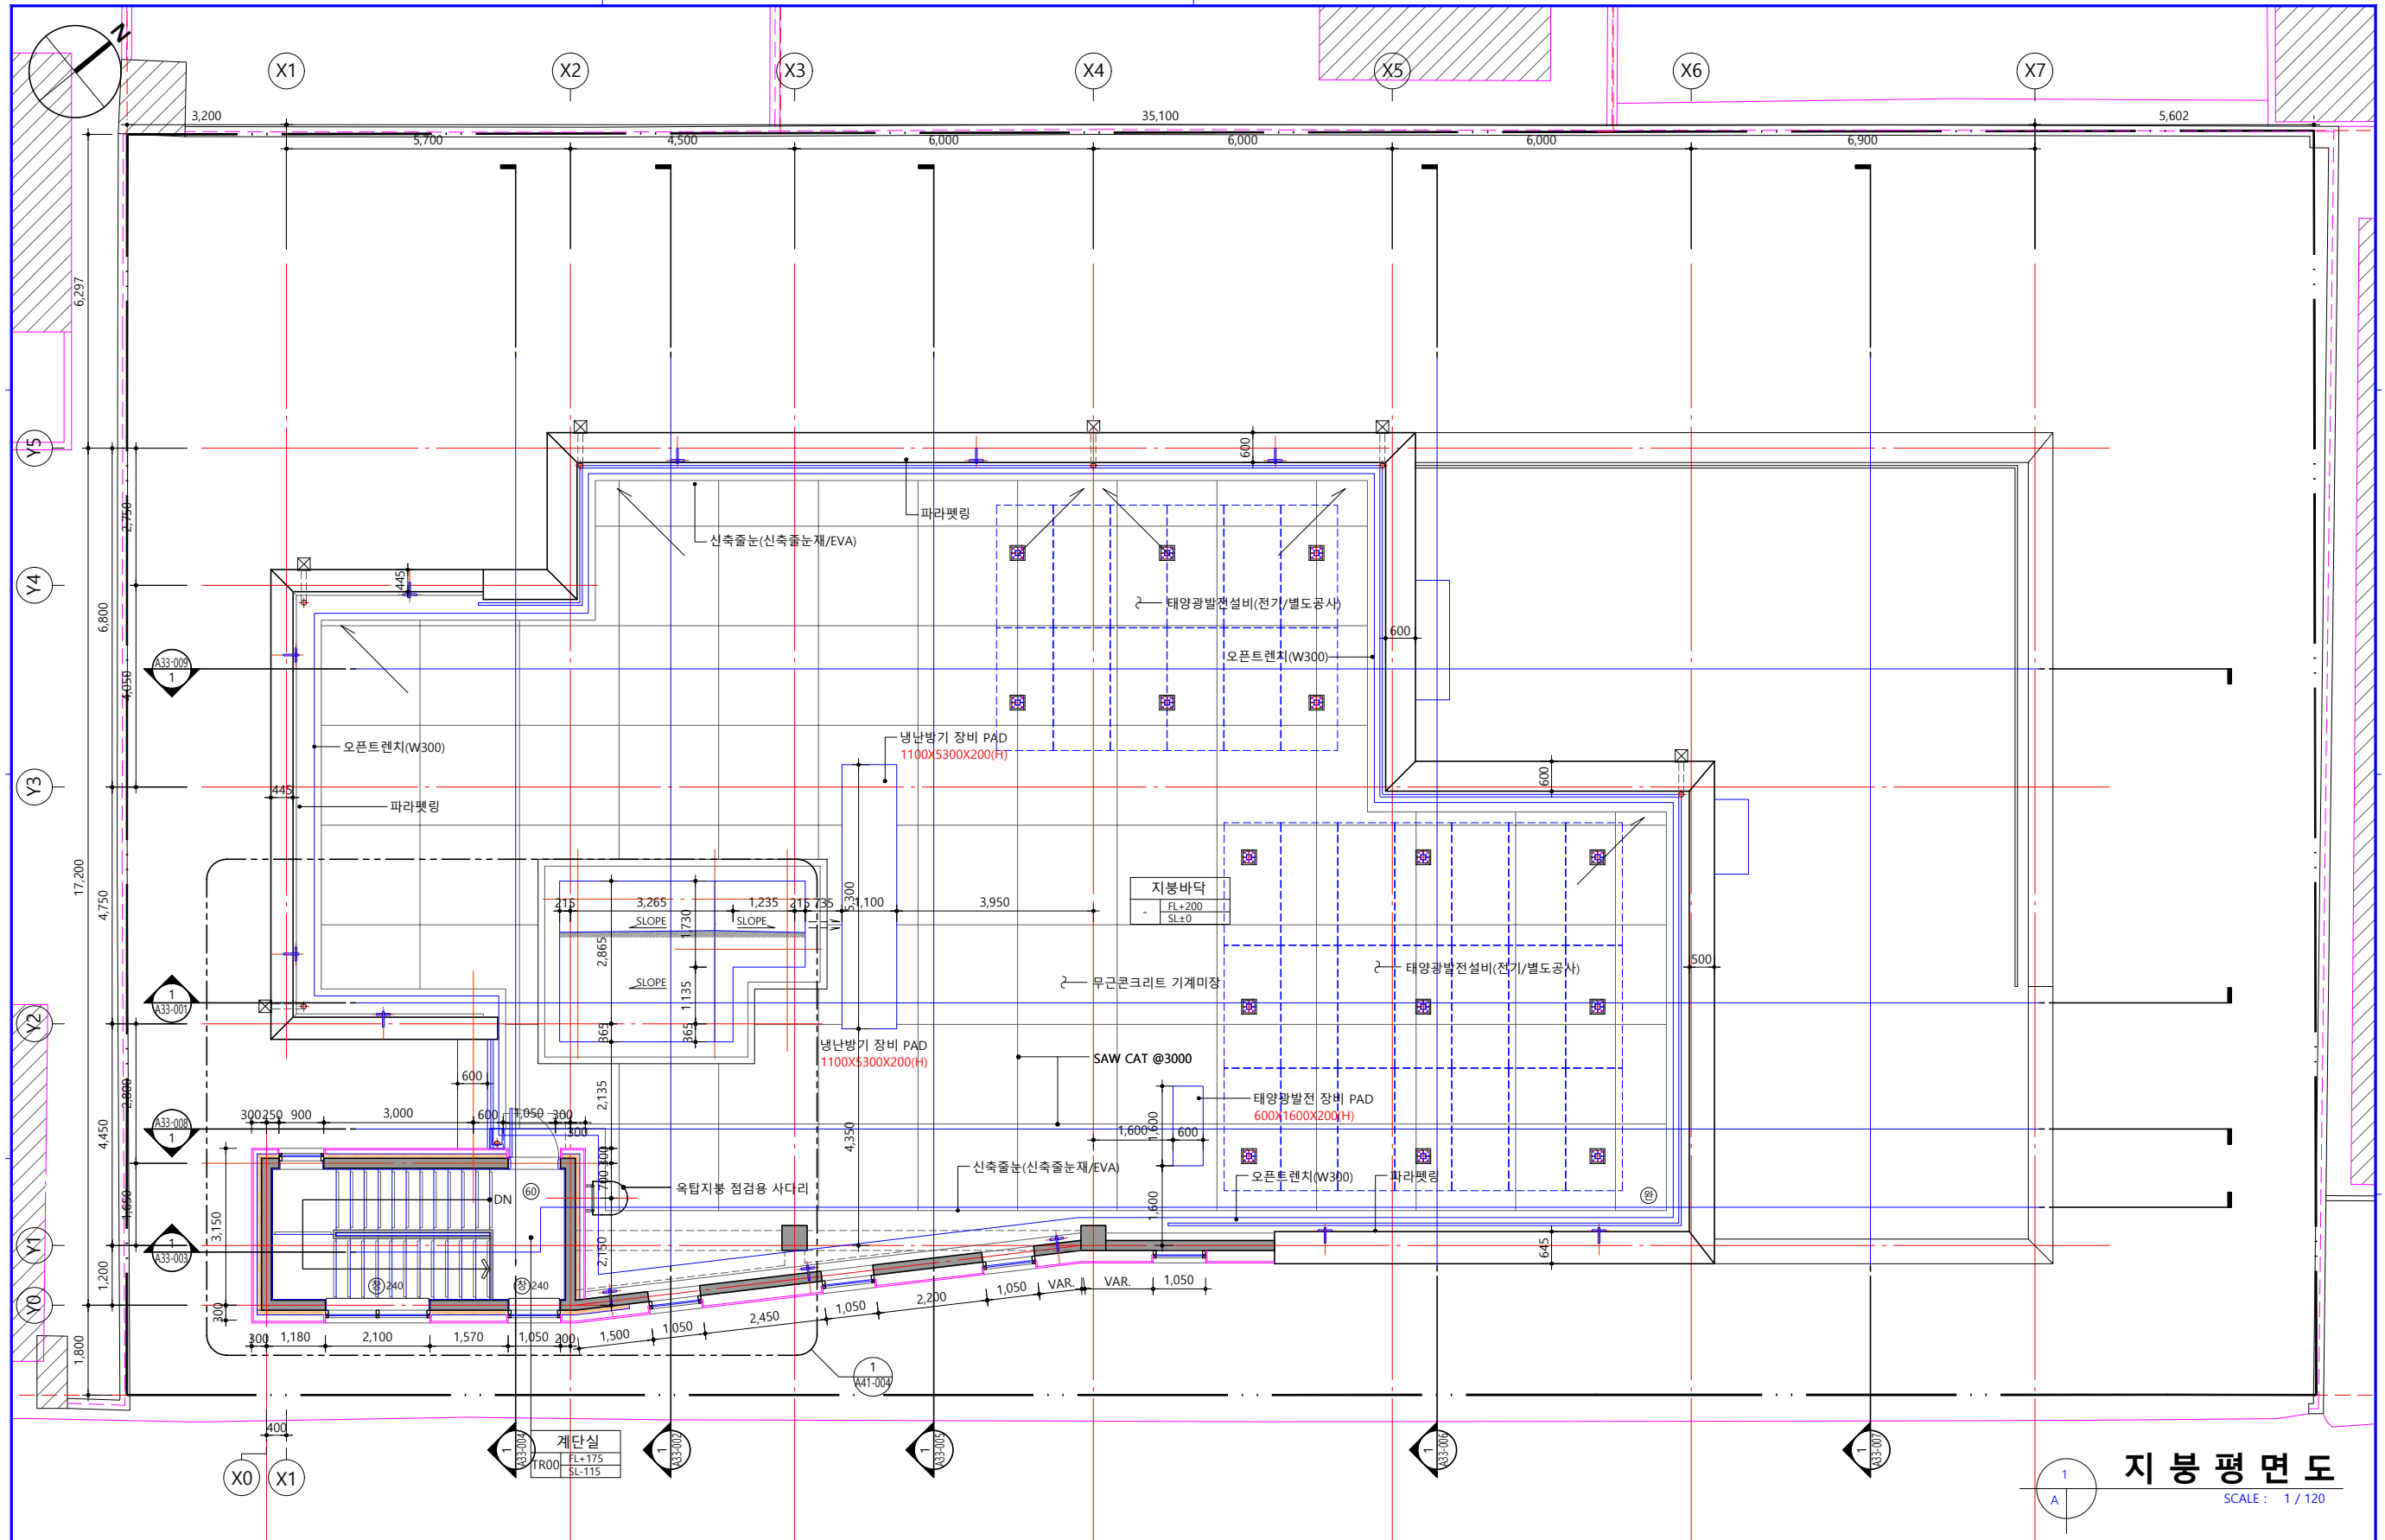

지붕 평면도  
SCALE: 1 / 120

|   |   |                      |                                                 |                    |                               |                                                  |   |                                                                    |                             |                                   |                             |                       |                                     |
|---|---|----------------------|-------------------------------------------------|--------------------|-------------------------------|--------------------------------------------------|---|--------------------------------------------------------------------|-----------------------------|-----------------------------------|-----------------------------|-----------------------|-------------------------------------|
| 건축주<br>CLIENT<br><div> NH농협은행<br/>(강원본부)</div> | 설계사무소<br>DESIGN OFFICE<br><div> 건축사무소<br/>지안21<br/>Tel. 02-6014-2137 / Fax. 02-6014-2138<br/>Email: archjian21@naver.com</div> | NOTE.                |                                                 |                    |                               |                                                  | 설계명<br>PROJECT TITLE<br><div> NH농협은행<br/>강릉 금융센터 신축공사</div> | 프로젝트번호 PROJECT CODE<br>JP25-0001<br>승인 APPROVED BY<br>황진희 00.00.00 | 도면명 DRAWING TITLE<br>지붕 평면도 |                                   |                             |                       |                                     |
|   |   |                      | <div><div>△</div><div>△</div><div>△</div></div> | 전문분야 SUBJECT<br>건축 | 검토 CHECKED BY<br>최용규 00.00.00 | 설계단계 DESIGN PHASE<br>작성 Drawn By<br>신가영 00.00.00 |   |                                                                    |                             | 축척 SCALE<br>A1: 1/60<br>A3: 1/120 | 도면번호 DRAWING NO.<br>A31-004 | 밀련번호 SHEET NO.<br>000 | REV. No.<br><div><div>△</div></div> |
|   |   |                      |                                                 |                    |                               |                                                  |   |                                                                    |                             |                                   |                             |                       |                                     |
| No.   | Date   | Revision Description | Chkd.                                           |                    |                               |                                                  |   |                                                                    |                             |                                   |                             |                       |                                     |

