


(중부2 지역)		구 분		(단위 : W/m ² · K)	단열재 종류	비 고
외벽	직접	공동주택 외벽	0.240 이하	단열재 W1	T90 NF보드(중물면) (열전도율 0.020W/m ² · K 이하)	-
				단열재 W2	T135 암합법보온판 (열전도율 0.027W/m ² · K 이하)	
				-		육상 ELEV 승강로
	간접					
최상층 지붕	직접		0.340 이하	단열재 W3	T80 암합법보온판 (열전도율 0.027W/m ² · K 이하)	ELEV PIT 외벽
	직접		0.150 이하	단열재 R1	T140 NF보드(중물면) (열전도율 0.020W/m ² · K 이하)	
최상층 바닥	직접	비난방	0.200 이하	단열재 F1	T110 NF보드(중물면) (열전도율 0.030W/m ² · K 이하)	필로티(주작장상부)
	간접		0.290 이하	단열재 F2	T100 암합법보온판 (열전도율 0.027W/m ² · K 이하)	1층 바닥


주단면도-3(횡-2)

건축주 CLIENT  NH농협은행 (강릉본부)	설계사무소 DESIGN OFFICE  건축사사무소 지안21 Tel. 02-6014-2137 / Fax. 02-6014-2138 Email : anchian21@naver.com	NOTE 1. 별도 표기가 없어도 모든 물품기(Drip Edge) 및 물줄림(Flashing)을 위한 두께 및 장안방, 하인방 등의 후래싱 경사도는 3°이상을 확보하여 시공할 것. 2. 안압대지 당장 시공시 반드시 면과와 현장상황을 고려한 시공계획을 수립하여 감독과의 승인을 득하여 시공할 것. 3. 방수층이 적어지는 모서리 부분은 삼각면개(구조재와 이철재 사용)를 활용하여 방수층 보호 조치 후 시공할 것.	                                                        
--	--	---	--

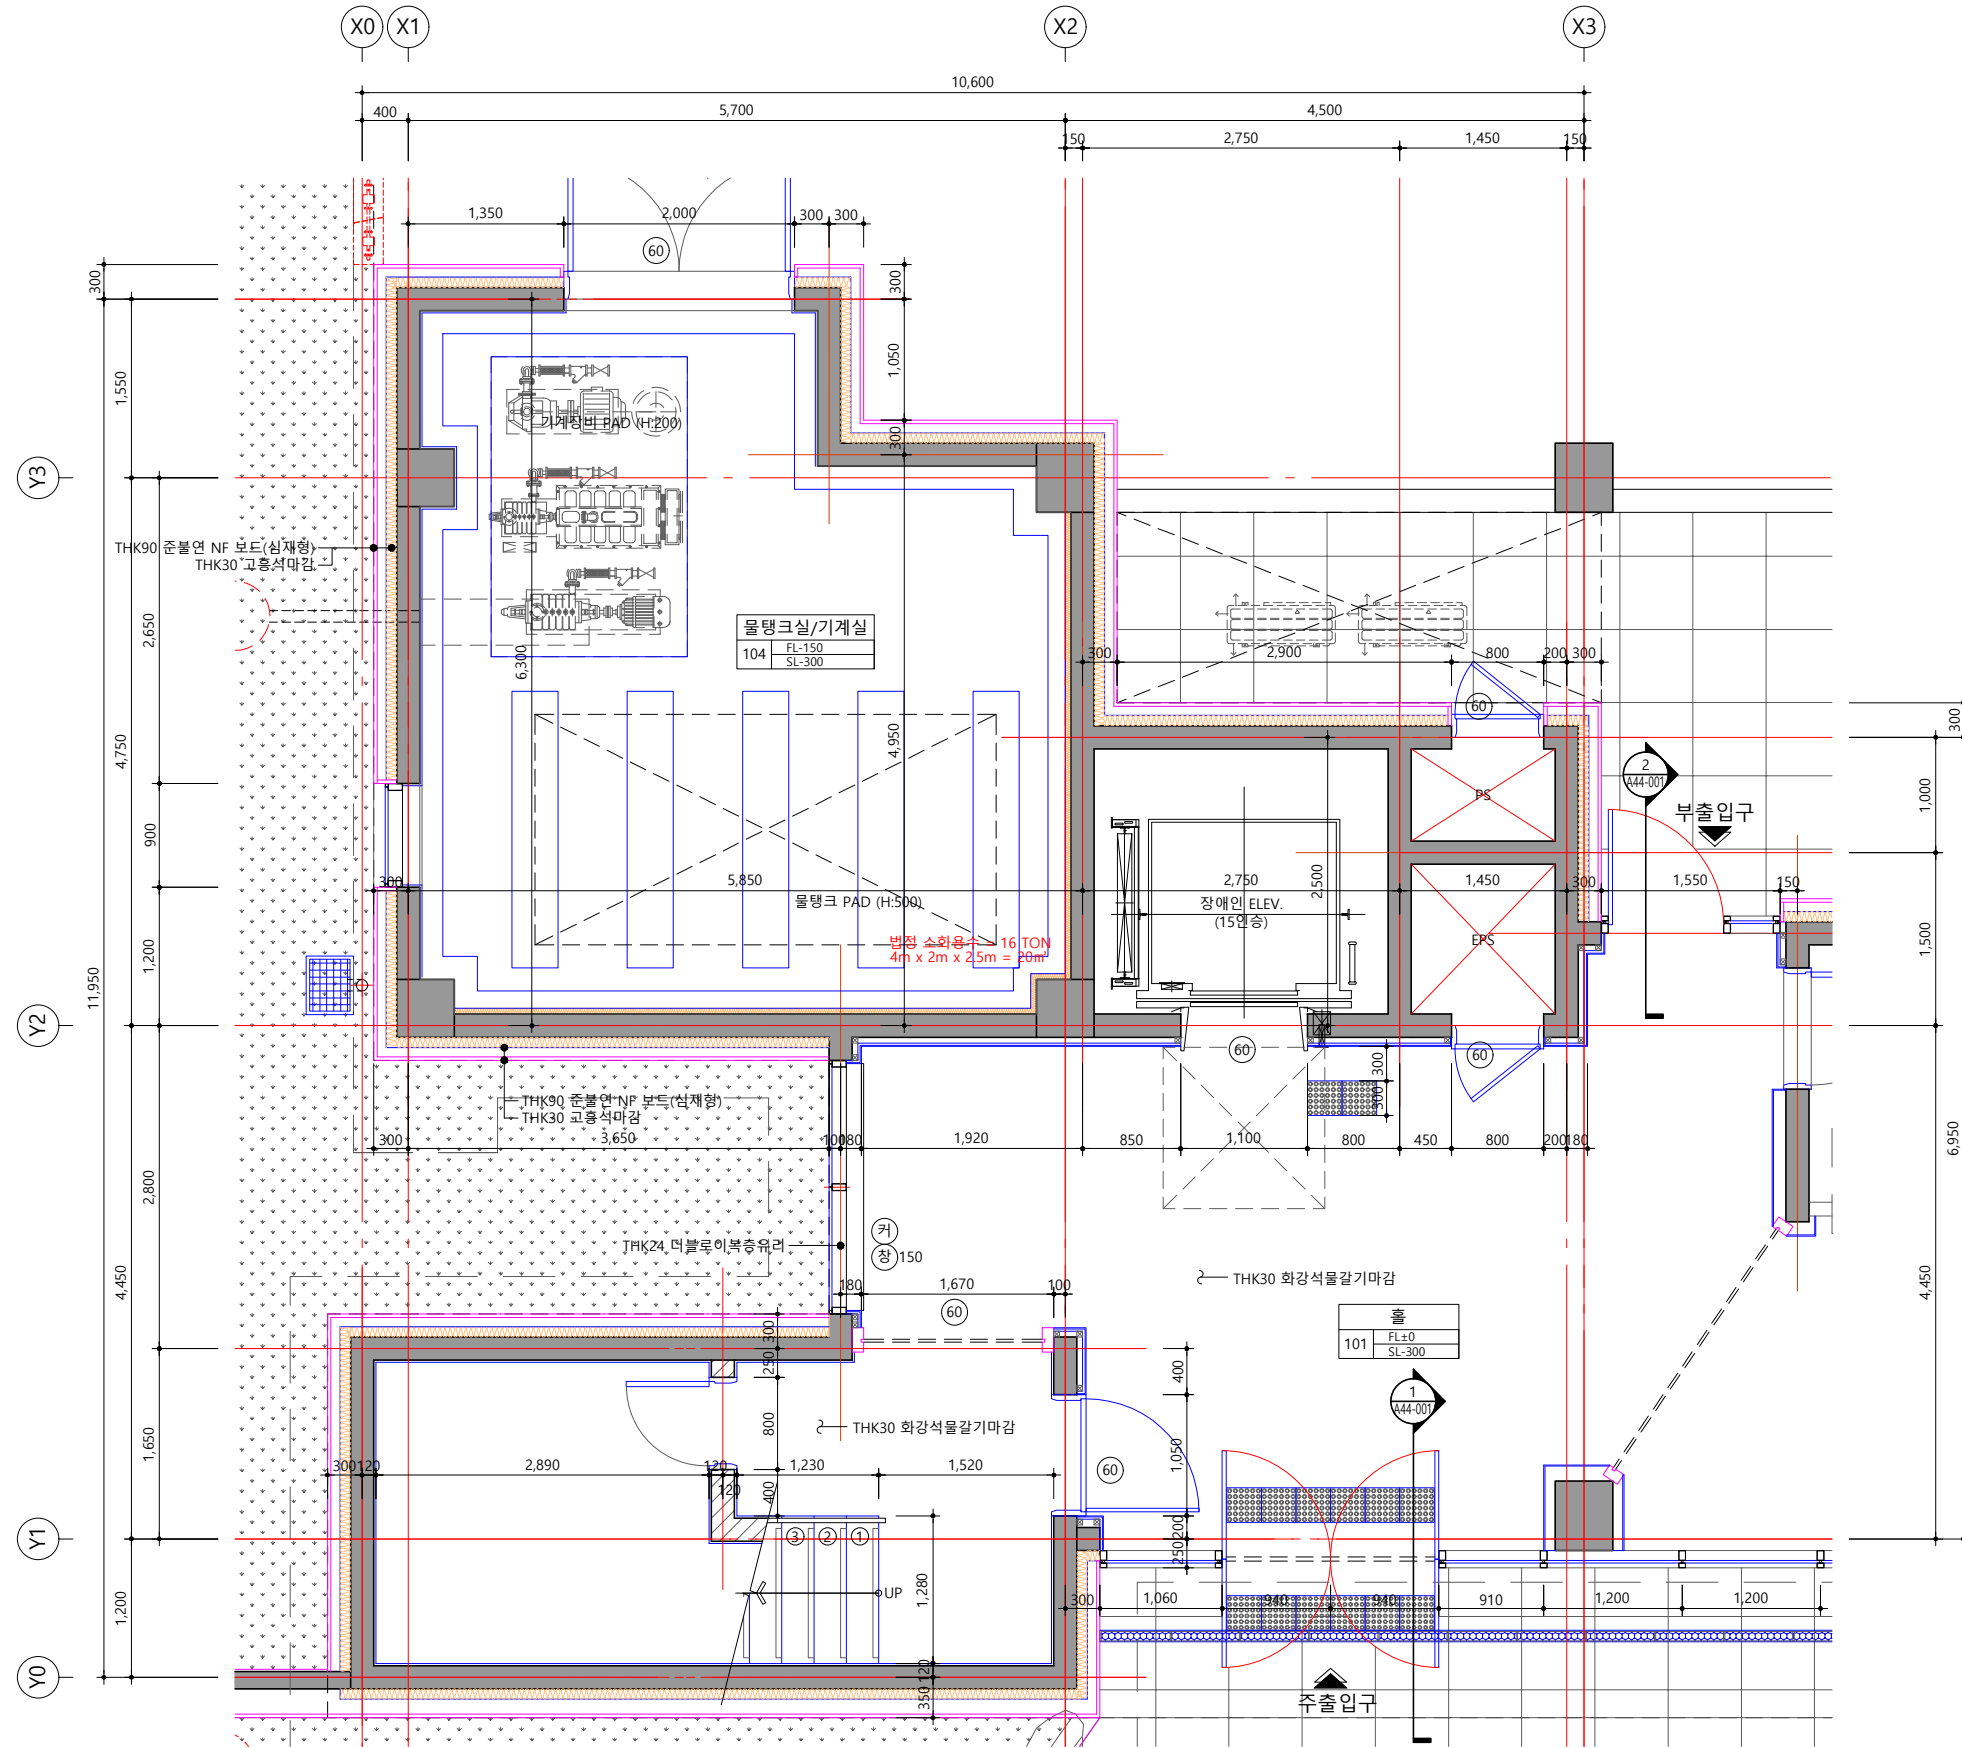


1층 계단실 확대평면도
SCALE: 1/60

건축주 CLIENT	NH농협은행 (강원본부) 지안21 건축사무소 Tel. 02-6014-2137 / Fax. 02-6014-2138 Email : archjian21@naver.com	NOTE. 1. 방화구획 방화문 ⑥0 2. 화강석 창대석 ⑧W:000 3. 커튼박스 ㄱ 4. 재료분리대 ㉔	No. Date Revision Description Chkd.	설계명 PROJECT TITLE	프로젝트번호 PROJECT CODE	승인 APPROVED BY	도면명 DRAWING TITLE				
				강릉 금융센터 신축공사	JP25-0001	황진희 00.00.00	1층 계단실 확대평면도				
					협약설계 CONSULTANT	건축구조 : (주)탐앤지니어링 토목 : (주)제일기초이엔씨 전기/통신/소방 : (주)하람엔지니어링	전문분야 SUBJECT	검토 CHECKED BY	축척 SCALE	A1: 1/30	도면번호 DRAWING NO. A41-001
						실시설계(변경)	최용규 00.00.00	작성 Drawn By			
				신가영 00.00.00							

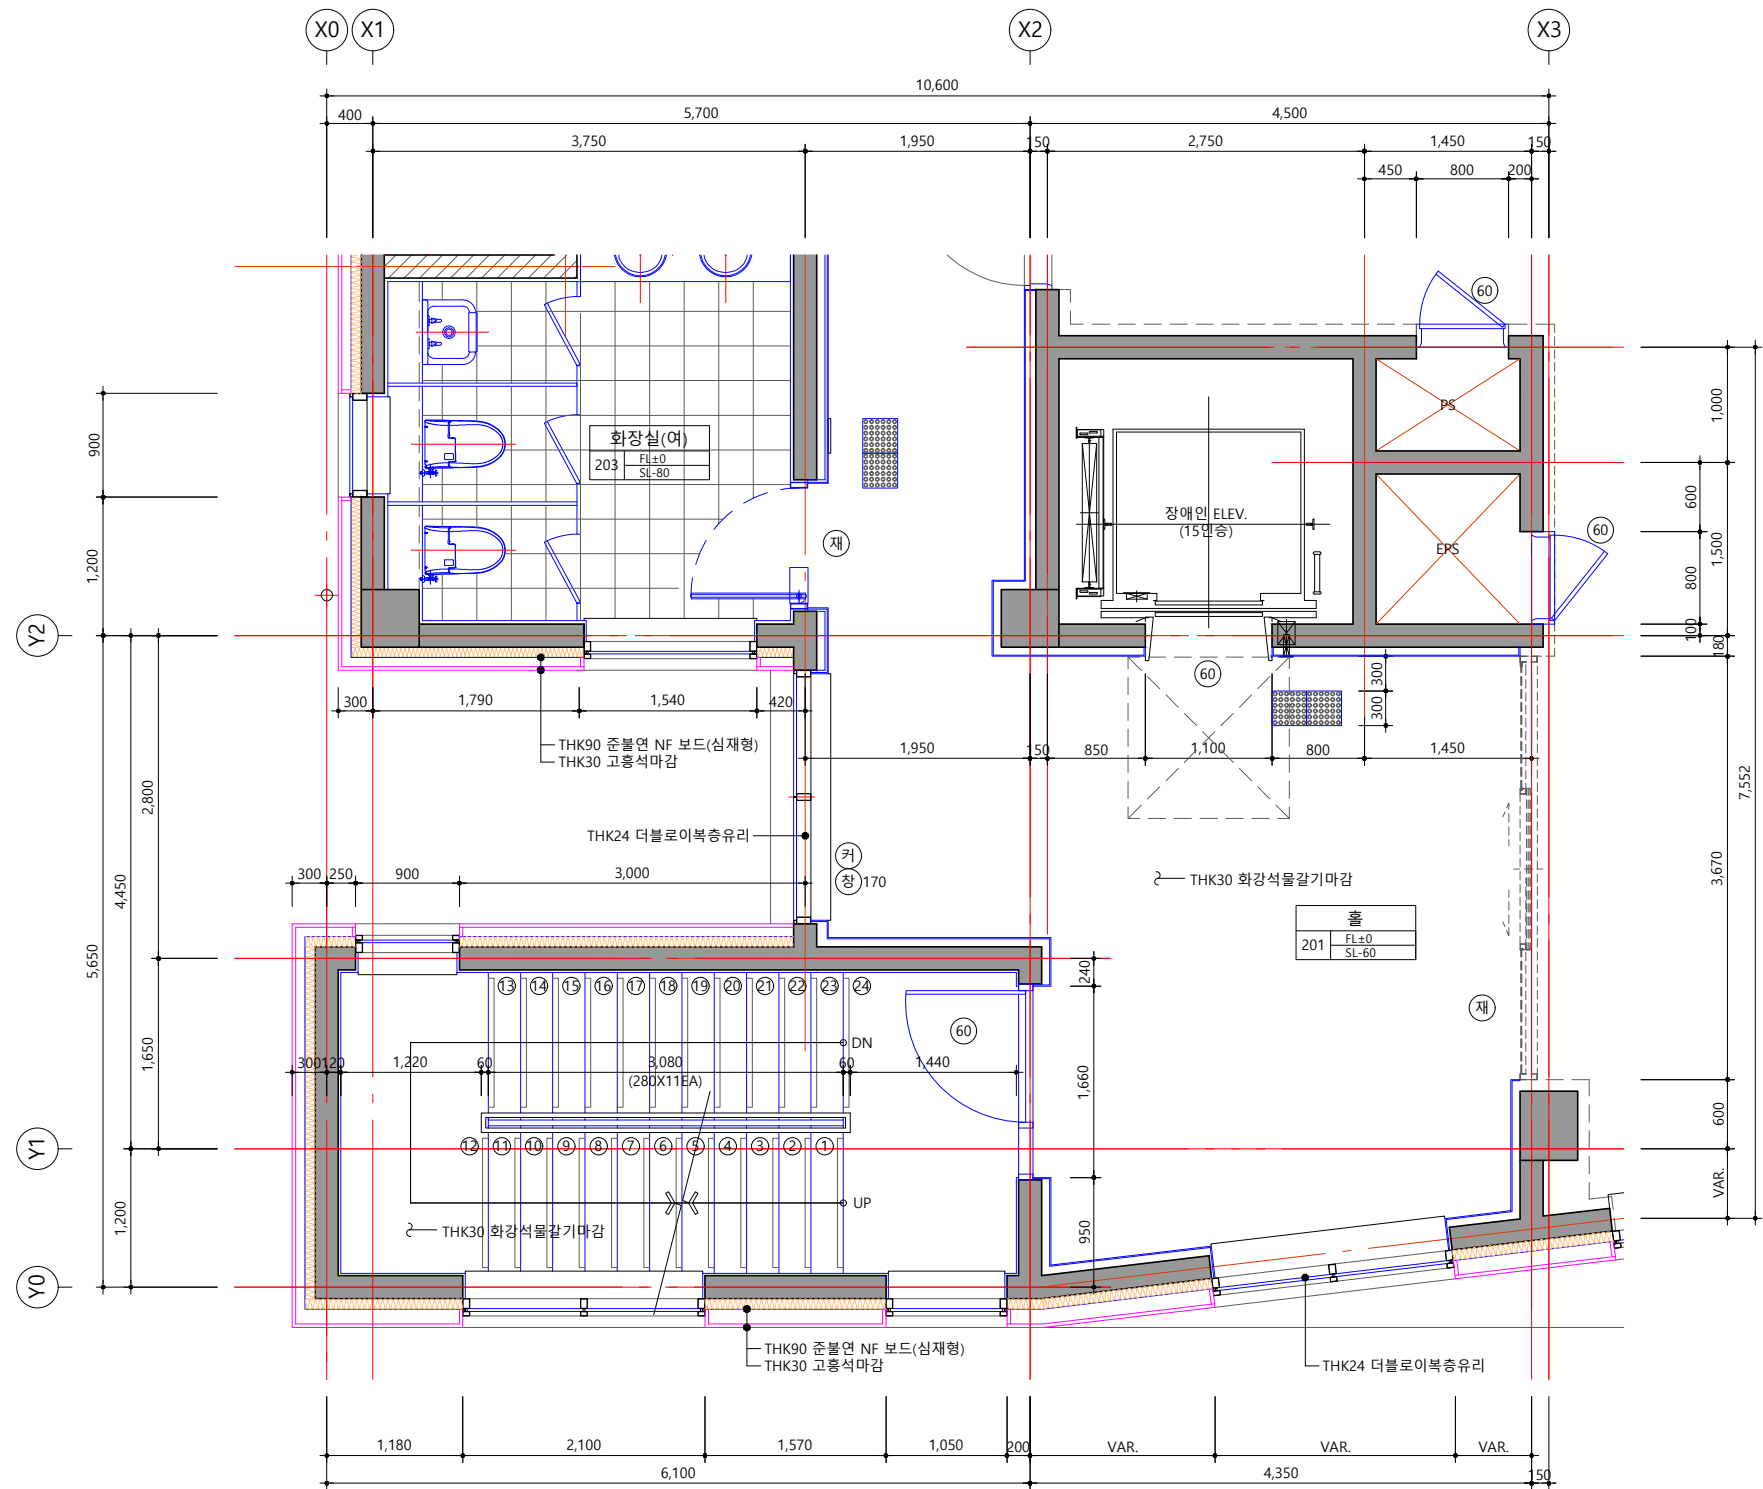


1
A
2층 계단실 확대평면도
SCALE : 1 / 60

건축주 CLIENT	설계사무소 DESIGN OFFICE Tel. 02-6014-2137 / Fax. 02-6014-2138 Email : archjian21@naver.com	NOTE. 1. 방화구획 방화문 ㉔ 2. 화강석 창대석 ㉔ W:900 3. 커튼박스 ㉔ 4. 재료분리대 ㉔	△			설계명 PROJECT TITLE 협력설계 CONSULTANT 건축구조 : (주)탐앤지니어링 토목 : (주) 제일기조이엔씨 전기/통신/소방 : (주)하랑엔지니어링	프로젝트번호 PROJECT CODE JP25-0001	승인 APPROVED BY 황진희 00.00.00	도면명 DRAWING TITLE 2층 계단실 확대평면도			
			△				전문분야 SUBJECT 건축	검토 CHECKED BY 최용규 00.00.00	축척 SCALE A1: 1/30 A3: 1/60	도면번호 DRAWING NO. A41-002	일련번호 SHEET NO. 000	REV. NO. △
			△				설계단계 DESIGN PHASE 실시설계(변경)	작성 Drawn By 신가영 00.00.00				
			△									
			No.	Date	Revision Description		Chkd.					

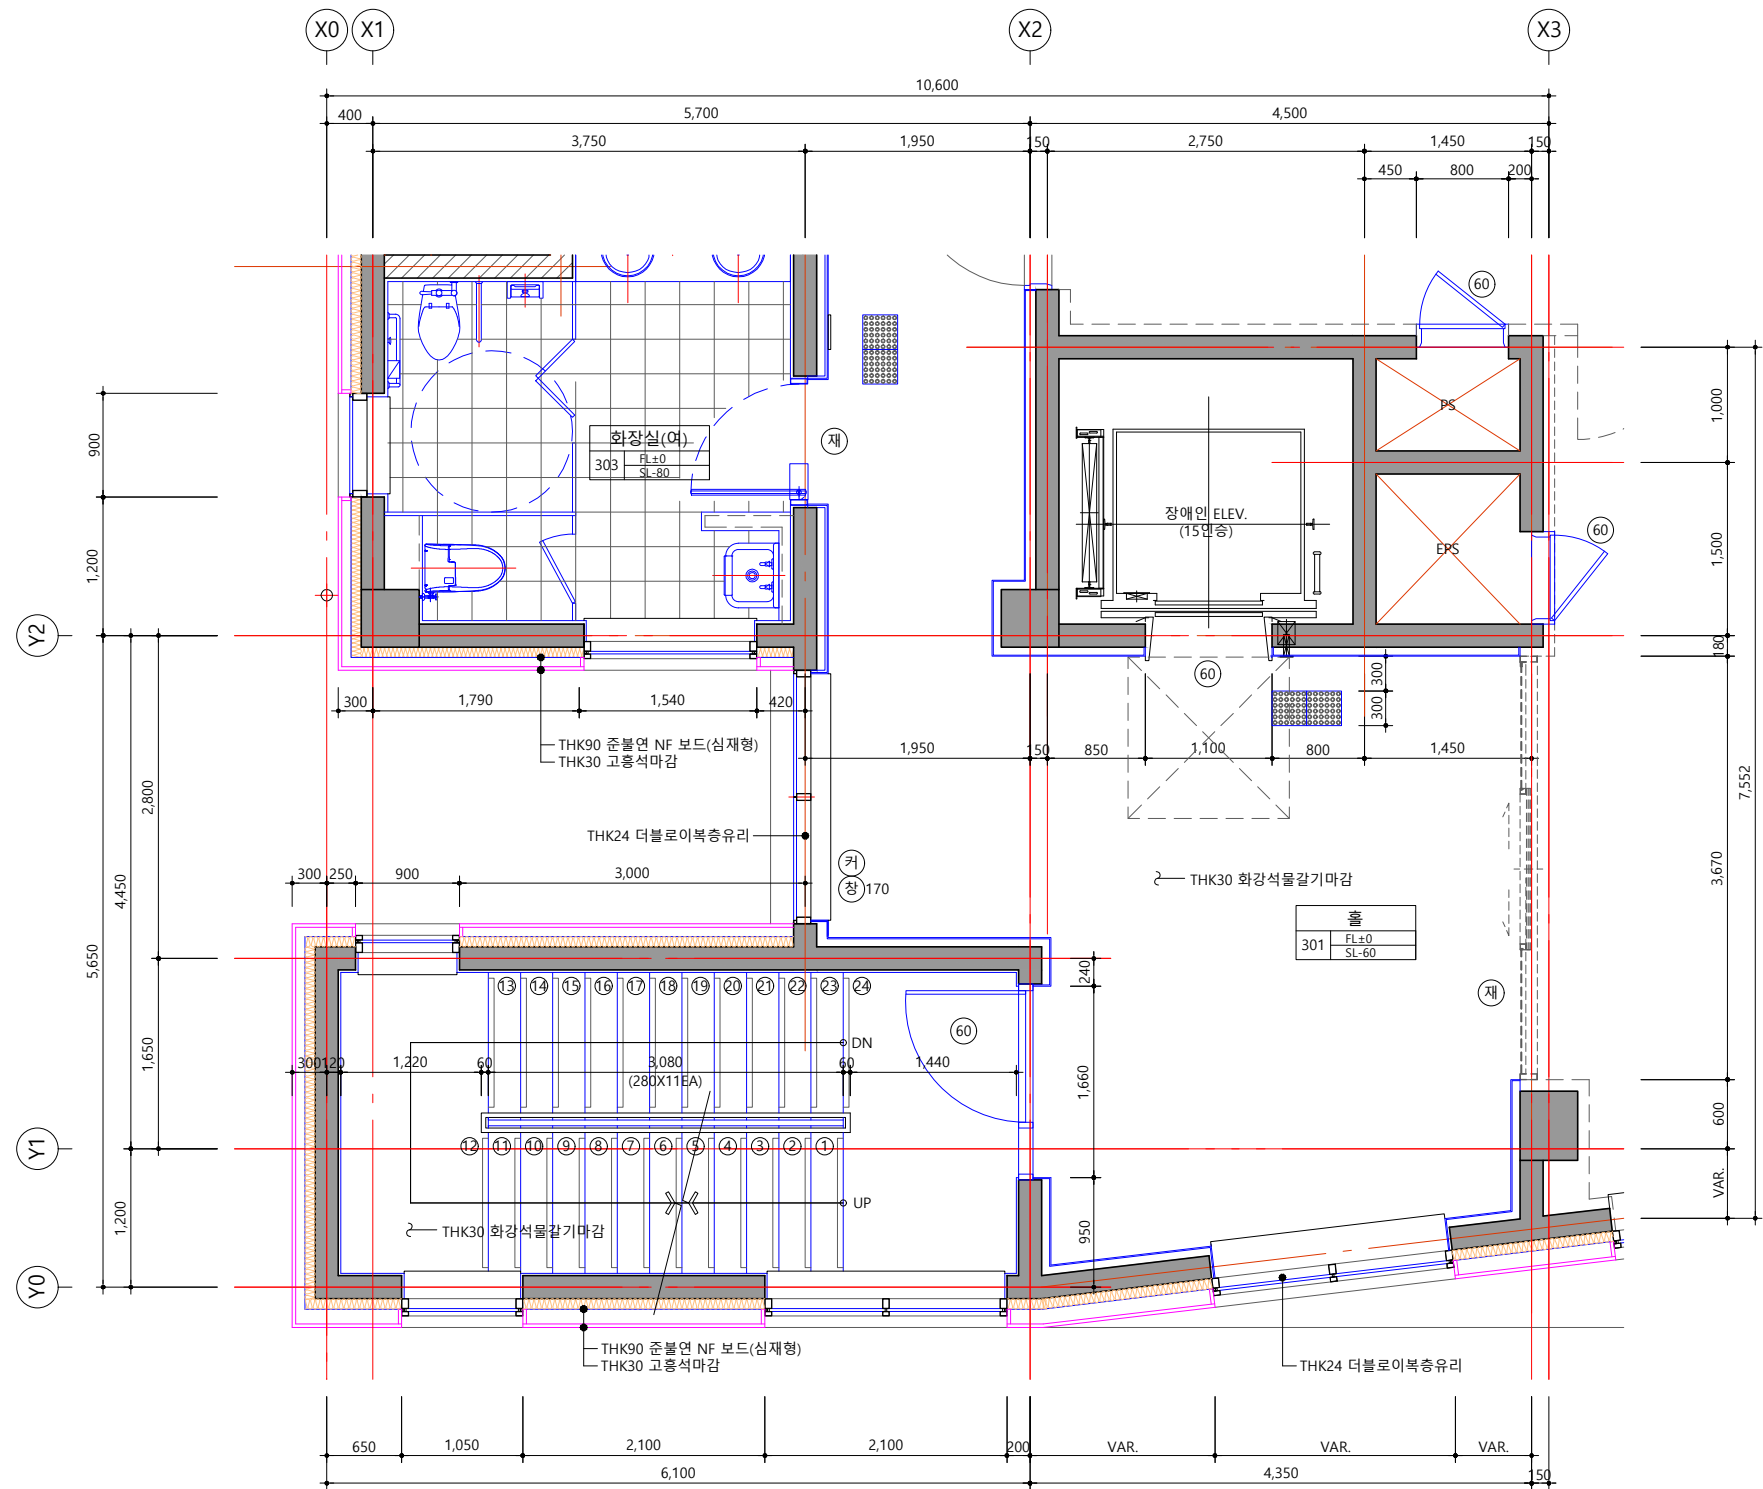


3층 계단실 확대평면도
SCALE : 1 / 60

건축주 CLIENT		설계사무소 DESIGN OFFICE	 지안21 Tel. 02-6014-2137 / Fax. 02-6014-2138 Email : archjian21@naver.com	NOTE. 1. 방화구획 방화문 ⑥ 2. 화강석 창대석 ⑧ W:900 3. 커튼박스 ⑦ 4. 재료분리대 ④	△			설계명 PROJECT TITLE		프로젝트번호 PROJECT CODE	승인 APPROVED BY	도면명 DRAWING TITLE	3층 계단실 확대평면도		
					△					전문분야 SUBJECT	검토 CHECKED BY		축척 SCALE	A1: 1/30	도면번호 DRAWING NO. A41-003
					△					건축	최용규				
					△					협력설계 CONSULTANT	건축구조 : (주)탐앤지니어링 토목 : (주) 제일기초이엔씨 전기/통신/소방 : (주)하랑엔지니어링		설계단계 DESIGN PHASE	작성 Drawn By	실면번호 SHEET NO. 000
No.	Date	Revision Description	Chkd.	실시설계(변경)	신가영	00.00.00									

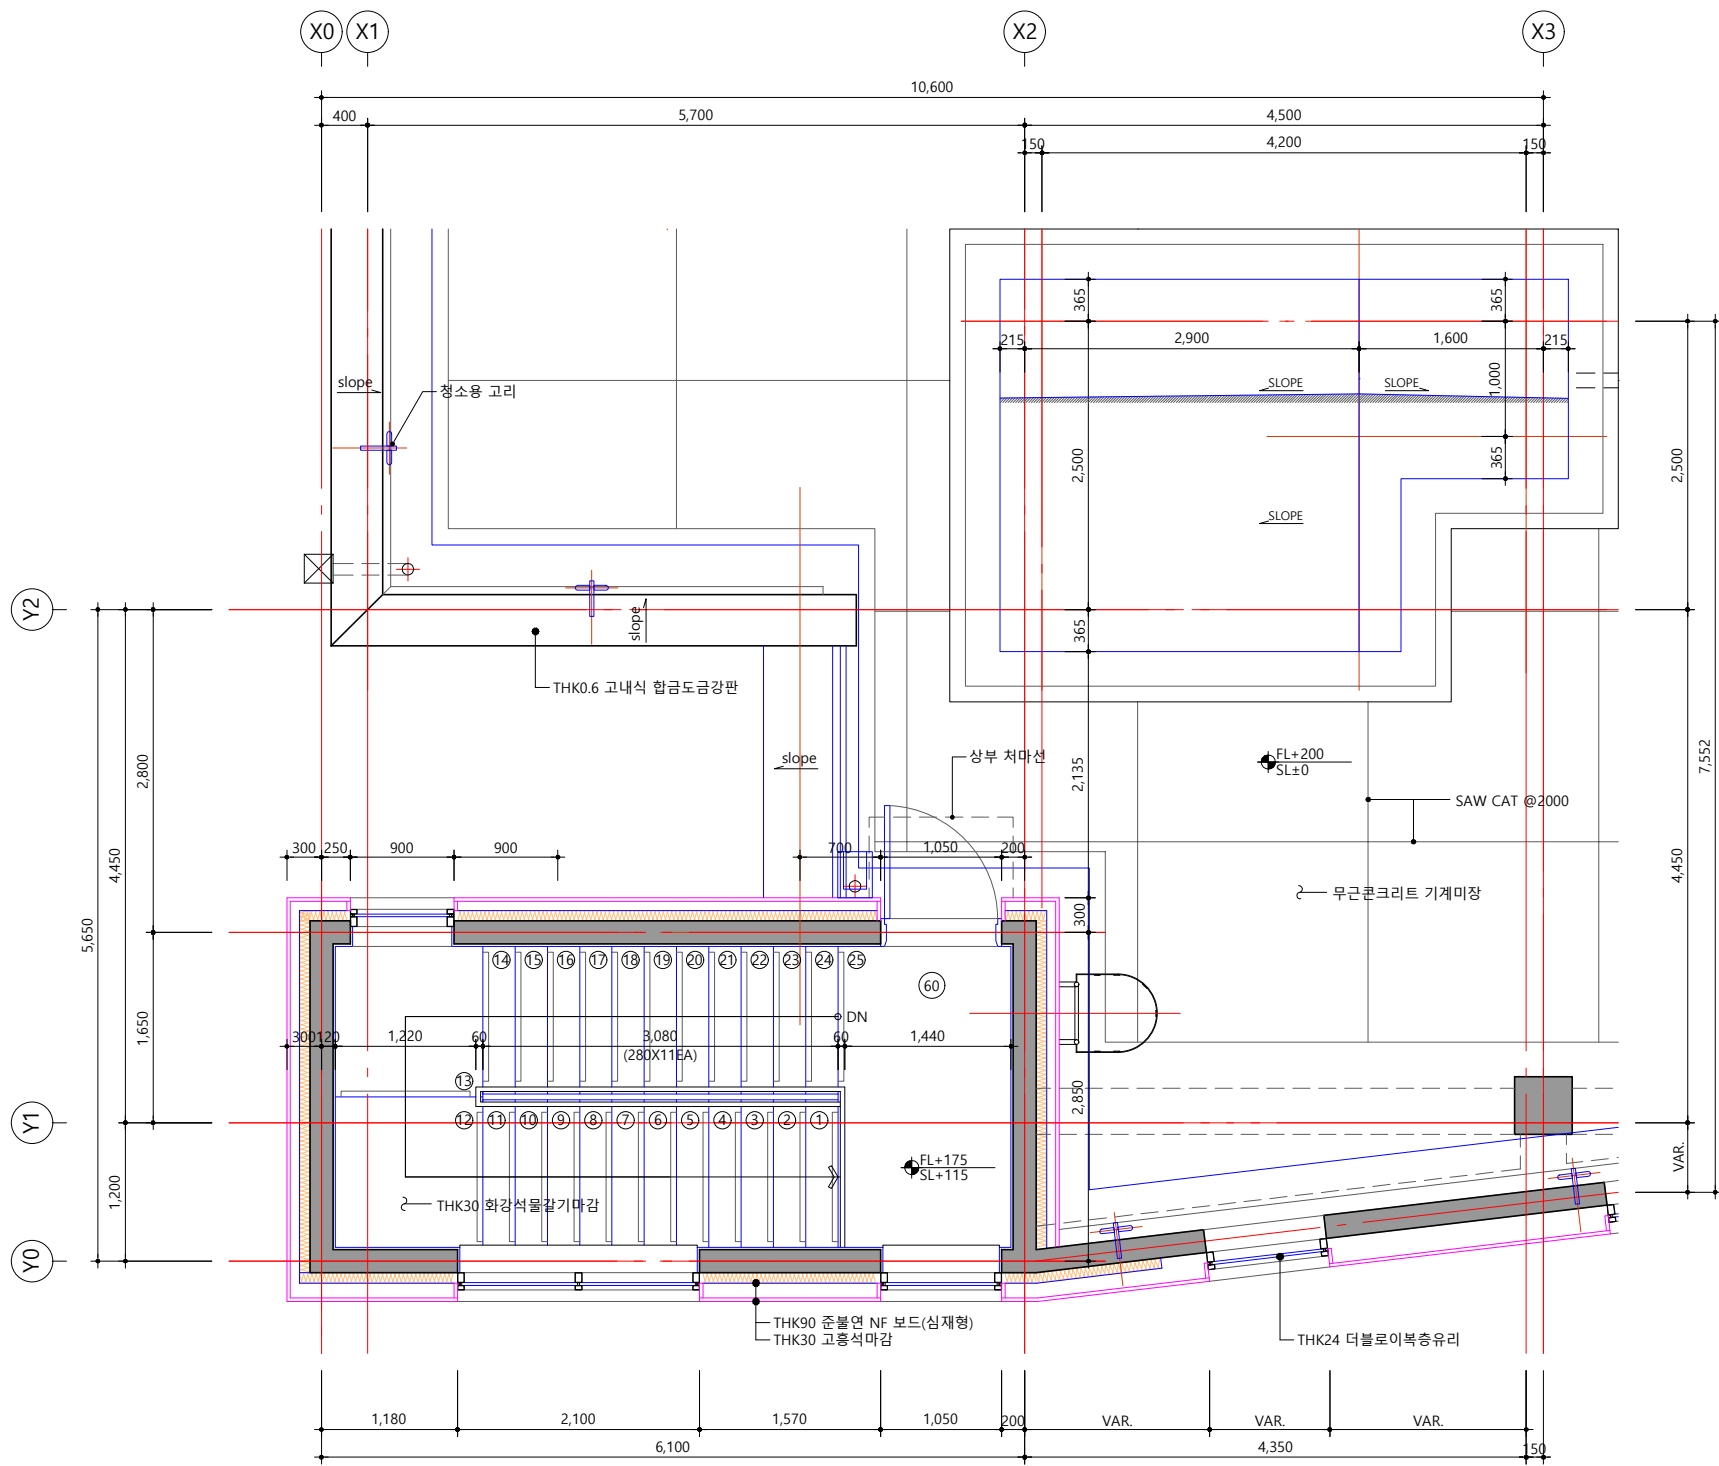

1 지붕 계단실 확대평면도
SCALE: 1 / 60

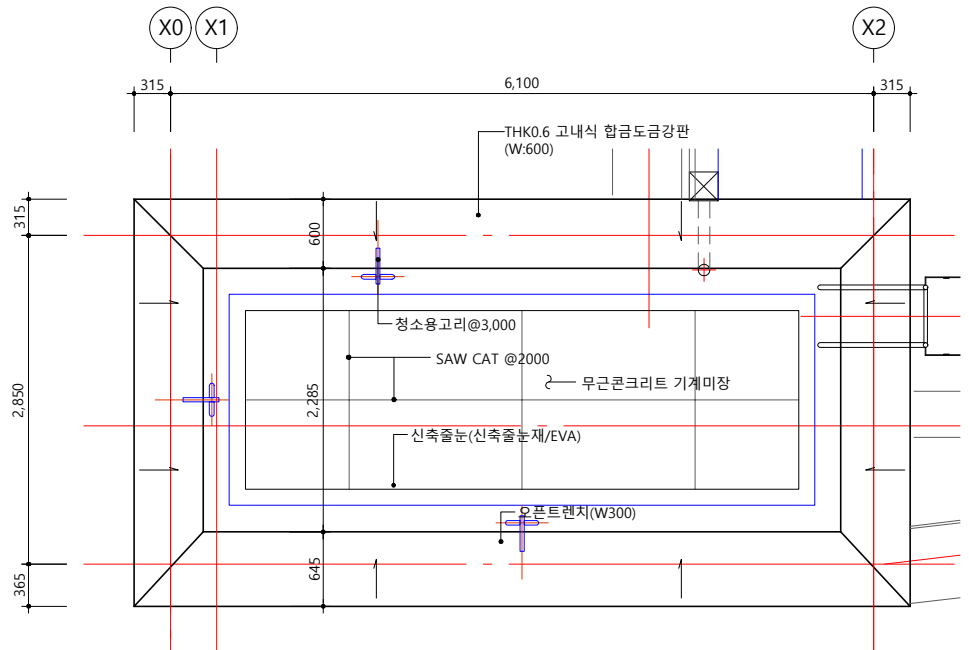

2 옥탑지붕 계단실 확대평면도
SCALE: 1 / 60

건축주 CLIENT	설계사무소 DESIGN OFFICE	건축사무소 지안21 Tel. 02-6014-2137 / Fax. 02-6014-2138 Email : archjian21@naver.com	NOTE.	설계명 PROJECT TITLE				프로젝트번호 PROJECT CODE	승인 APPROVED BY	도면명 DRAWING TITLE		
			1. 방화구획 방화문 ⑥	강릉 금융센터 신축공사				JP25-0001	황진희 00.00.00	옥탑, 옥탑지붕 계단실 확대평면도		
			2. 화강석 창대석 ⑧ W:900	협력설계 CONSULTANT				건축	최용규 00.00.00	축척 SCALE	A1: 1/30	도면번호 DRAWING NO. A41-004
			3. 커튼박스 ⑨					건축구조 : (주)탐앤지니어링	작성 Drawn By			
			4. 재료분리대 ⑩					토목 : (주) 제일기초이엔씨	신가영 00.00.00		REV. No. △	
No.	Date	Revision Description	Chkd.	설계단계 DESIGN PHASE	실시설계(변경)							