

1 층

[illegible][illegible]


지붕

The diagram shows a roof plan with a grid system. The horizontal grid lines are labeled X1 through X7, and the vertical grid lines are labeled Y0 through Y5. The total width of the plan is 35,100 units, and the total depth is 17,200 units. The plan includes a staircase area at the bottom left, a central corridor, and two large rectangular areas with blue dashed lines and small squares, likely representing structural elements or equipment. Dimensions are provided for the grid intervals: 5,700 (X1-X2), 4,500 (X2-X3), 6,000 (X3-X4), 6,000 (X4-X5), 6,000 (X5-X6), and 6,900 (X6-X7). Vertical dimensions are 200 (Y0-Y1), 4,450 (Y1-Y2), 4,750 (Y2-Y3), 4,050 (Y3-Y4), and 2,750 (Y4-Y5). A circular feature labeled '5 FSD' is located near the staircase. Four circular features labeled '4-1 AW', '4-2 AW', '4-3 AW', and '4-4 AW' are located along the bottom edge of the plan.

 NH농협은행 (강원본부)	설계사무소 DESIGN OFFICE 건축사사무소 아찬21 Tel. 02-6014-2137 / Fax. 02-6014-2138 Email : archjan21@naver.com	NOTE				설계명 PROJECT TITLE 	프로젝트번호 PROJECT CODE 승인 APPROVED BY		도면명 DRAWING TITLE				
		1. 창세트 에너지소비효율등급 기준 1등급 : 열관류율 R ≤ 0.9 (W/m ² K) /기밀성 1등급 2등급 : 0.9 < R ≤ 1.2 /기밀성 1등급 3등급 : 1.2 ≤ R ≤ 1.8 /기밀성 2등급 이상 4등급 : 1.8 < R ≤ 2.3 /기밀성 용치 없음		4. 모든 외벽 창호는 외부용 기밀, 방수테이프를 반드시 적용하여 시공할 것.			설계명 PROJECT TITLE	JP25-0001		한진희 00.00.00			
		5. 기밀, 방수테이프의 폭은 해당제품 사양서에 따르며, 창호와 끝조와의 간격이 넓을수록 충분한 접착면을 확보하도록 시공할 것.			협력설계 CONSULTANT		건축 구조 : (주)탐페니지니어링 목욕 : (주) 제일기초이엔씨 전기/통신/소방 : (주)하림엔지니어링		원도 CHECKED BY 최홍규 00.00.00		축적 SCALE A1: 1/150 A3: 1/300	도면번호 DRAWING NO. A61-001 알랜번호 SHEET No. 000	
		2. 창호는 설계된 등급과 동등이상의 제품으로 시공할 것. 3. 창호 Bar, 유리, 백판넬, 유리내측 부 피인트의 색상은 감독관의 승인을 득하여 시공 할 것.			No. Date Revision Description Chkd.		실시설계(변경)		작성 Drawn By 신가영 00.00.00				


축척 SCALE	A1: 1/50	도면번호 DRAWING NO. A61-003	
	A3: 1/100	일련번호 SHEET NO. 000	REV. No. 

도면명 DRAWING TITLE 창호일람표-3			
축척 SCALE	A1: 1/50	도면번호 DRAWING NO. A61-004	
	A3: 1/100	일련번호 SHEET NO. 000	REV. No. 

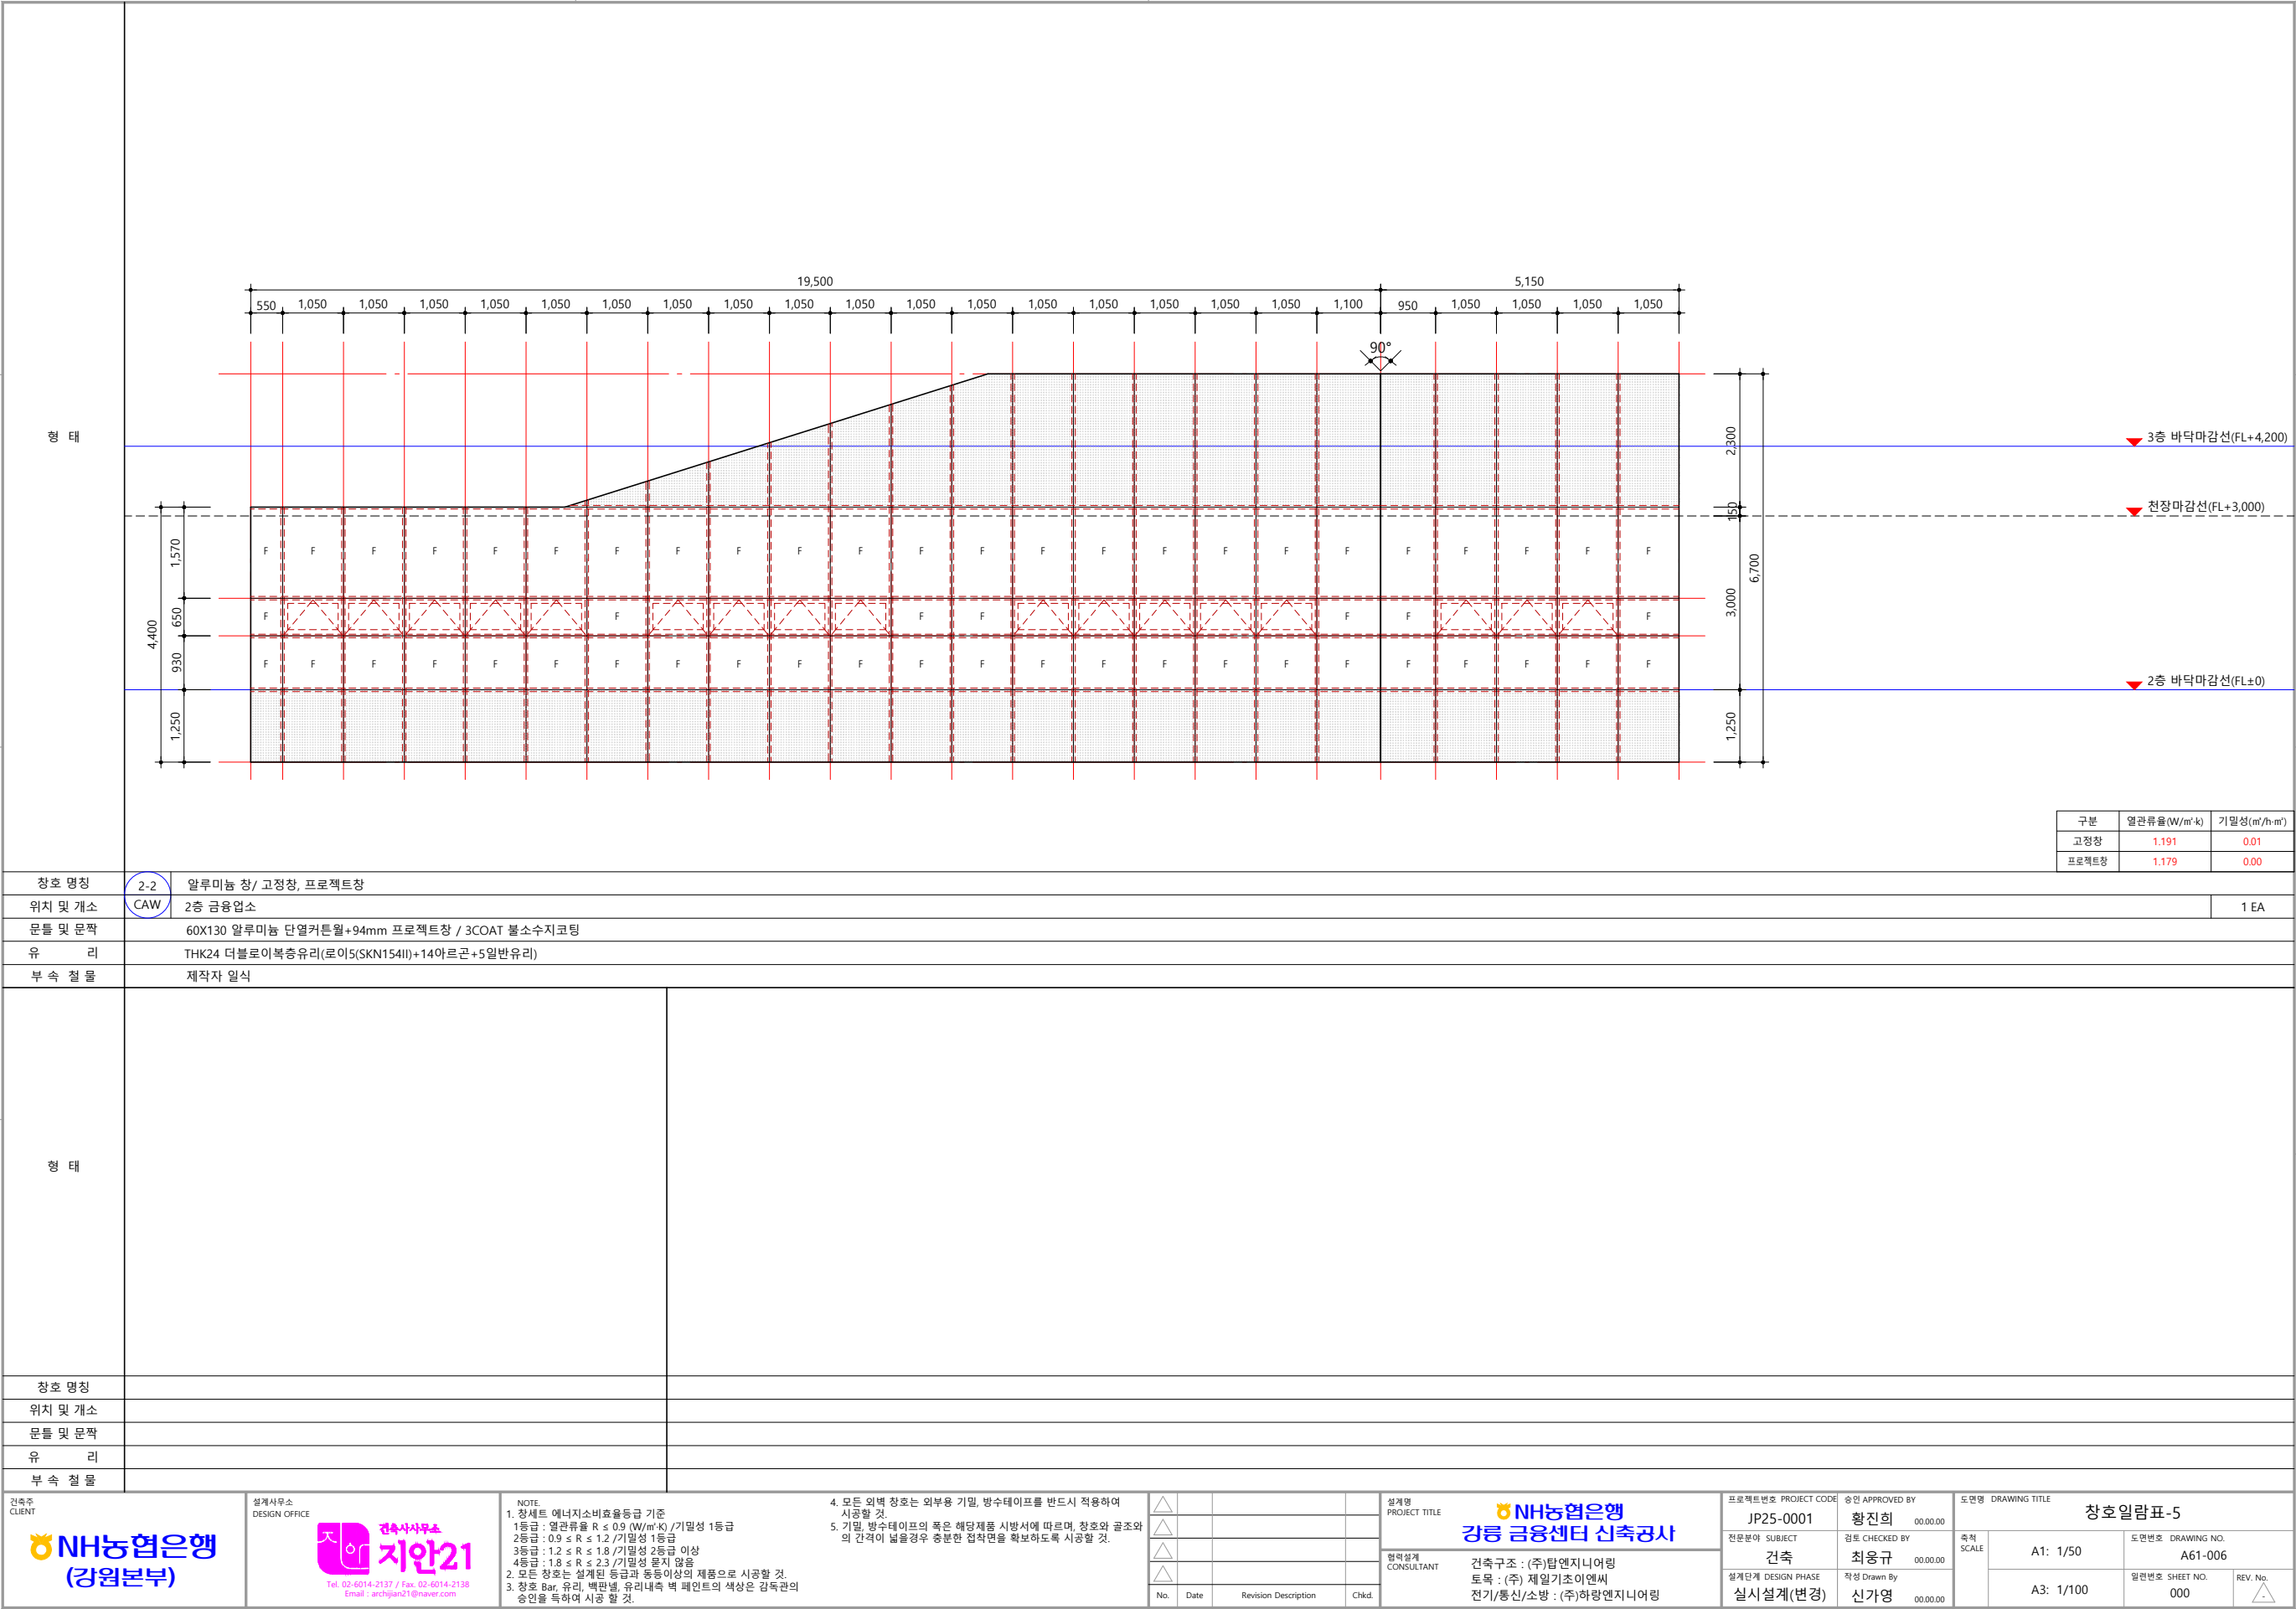


형 태																																					
	<table><tr><td>구분</td><td>열관류율(W/m²·k)</td><td>기밀성(m³/h·m²)</td></tr><tr><td>고정창</td><td>1.191</td><td>0.01</td></tr></table>		구분	열관류율(W/m²·k)	기밀성(m³/h·m²)	고정창	1.191	0.01	<table><tr><td>구분</td><td>열관류율(W/m²·k)</td><td>기밀성(m³/h·m²)</td></tr><tr><td>고정창</td><td>1.191</td><td>0.01</td></tr><tr><td>프로젝트창</td><td>1.179</td><td>0.00</td></tr></table>		구분	열관류율(W/m²·k)	기밀성(m³/h·m²)	고정창	1.191	0.01	프로젝트창	1.179	0.00	<table><tr><td>구분</td><td>열관류율(W/m²·k)</td><td>기밀성(m³/h·m²)</td></tr><tr><td>고정창</td><td>1.191</td><td>0.01</td></tr><tr><td>프로젝트창</td><td>1.179</td><td>0.00</td></tr></table>		구분	열관류율(W/m²·k)	기밀성(m³/h·m²)	고정창	1.191	0.01	프로젝트창	1.179	0.00	<table><tr><td>구분</td><td>열관류율(W/m²·k)</td><td>기밀성(m³/h·m²)</td></tr><tr><td>고정창</td><td>1.191</td><td>0.01</td></tr></table>		구분	열관류율(W/m²·k)	기밀성(m³/h·m²)	고정창	1.191
구분	열관류율(W/m²·k)	기밀성(m³/h·m²)																																			
고정창	1.191	0.01																																			
구분	열관류율(W/m²·k)	기밀성(m³/h·m²)																																			
고정창	1.191	0.01																																			
프로젝트창	1.179	0.00																																			
구분	열관류율(W/m²·k)	기밀성(m³/h·m²)																																			
고정창	1.191	0.01																																			
프로젝트창	1.179	0.00																																			
구분	열관류율(W/m²·k)	기밀성(m³/h·m²)																																			
고정창	1.191	0.01																																			
창호 명칭	3-1	알루미늄 창/ 고정창(완강기창)		3-2	알루미늄 창/ 고정창, 프로젝트창		3-3	알루미늄 창/ 고정창, 프로젝트창		3-4	알루미늄 창/ 고정창																										
위치 및 개소	CAW	3층 여신관리단 1 EA		CAW	3층 여신관리단 1 EA		CAW	3층 여신관리단 1 EA		CAW	3층 여신관리단 1 EA																										
문틀 및 문짝	60X150 알루미늄 단열커튼월 / 3COAT 불소수지코팅			60X150 알루미늄 단열커튼월+94mm 프로젝트창 / 3COAT 불소수지코팅			60X150 알루미늄 단열커튼월+94mm 프로젝트창 / 3COAT 불소수지코팅			60X150 알루미늄 커튼월 / 3COAT 불소수지코팅																											
유 리	THK24 더블로이복층유리(로이5(SKN154II))+14아르곤+5일반유리)			THK24 더블로이복층유리(로이5(SKN154II))+14아르곤+5일반유리)			THK24 더블로이복층유리(로이5(SKN154II))+14아르곤+5일반유리)			THK24 더블로이복층유리(로이5(SKN154II))+14아르곤+5일반유리)																											
부 속 철 물	제작자 일식			제작자 일식			제작자 일식			제작자 일식																											
	<table><tr><td>구분</td><td>열관류율(W/m²·k)</td><td>기밀성(m³/h·m²)</td></tr><tr><td>고정창</td><td>1.191</td><td>0.01</td></tr></table>		구분	열관류율(W/m²·k)	기밀성(m³/h·m²)	고정창	1.191	0.01	<table><tr><td>구분</td><td>열관류율(W/m²·k)</td><td>기밀성(m³/h·m²)</td></tr><tr><td>고정창</td><td>1.191</td><td>0.01</td></tr><tr><td>프로젝트창</td><td>1.179</td><td>0.00</td></tr></table>		구분	열관류율(W/m²·k)	기밀성(m³/h·m²)	고정창	1.191	0.01	프로젝트창	1.179	0.00																		
구분	열관류율(W/m²·k)	기밀성(m³/h·m²)																																			
고정창	1.191	0.01																																			
구분	열관류율(W/m²·k)	기밀성(m³/h·m²)																																			
고정창	1.191	0.01																																			
프로젝트창	1.179	0.00																																			
창호 명칭	4-1	알루미늄 창/ 고정창		4-2	알루미늄 창/ 고정창, 프로젝트창		4-3	알루미늄 창/ 고정창		4-4	알루미늄 창/ 고정창																										
위치 및 개소	AW	지붕 계단실 1 EA		AW	지붕 계단실 1 EA		AW	지붕(외부) 2 EA		AW	지붕(외부) 1 EA																										
문틀 및 문짝	60X150 알루미늄 단열커튼월 / 3COAT 불소수지코팅			60X150 알루미늄 단열커튼월+94mm 프로젝트창 / 3COAT 불소수지코팅			60X150 알루미늄 단열커튼월 / 3COAT 불소수지코팅			60X150 알루미늄 단열커튼월 / 3COAT 불소수지코팅																											
유 리	THK24 더블로이복층유리(로이5(SKN154II))+14아르곤+5일반유리)			THK24 더블로이복층유리(로이5(SKN154II))+14아르곤+5일반유리)			THK24 더블로이복층유리(로이5(SKN154II))+14아르곤+5일반유리)			THK24 더블로이복층유리(로이5(SKN154II))+14아르곤+5일반유리)																											
부 속 철 물	제작자 일식			제작자 일식			제작자 일식			제작자 일식																											
건축주 CLIENT	설계사무소 DESIGN OFFICE		NOTE. 1. 창세트 에너지소비효율등급 기준 1등급: 열관류율 R ≤ 0.9 (W/m²·K) / 기밀성 1등급 2등급: 0.9 ≤ R ≤ 1.2 / 기밀성 1등급 3등급: 1.2 ≤ R ≤ 1.8 / 기밀성 2등급 이상 4등급: 1.8 ≤ R ≤ 2.3 / 기밀성 불지 않음 2. 모든 창호는 설계된 등급과 동등이상의 제품으로 시공할 것. 3. 창호 Bar, 유리, 벽판넬, 유리내측 벽 페인트의 색상은 감독관의 승인을 득하여 시공 할 것.		4. 모든 외벽 창호는 외부용 기밀, 방수테이프를 반드시 적용하여 시공할 것. 5. 기밀, 방수테이프의 폭은 해당제품 시방서에 따르며, 창호와 골조와의 간격이 넓을경우 충분한 접착면을 확보하도록 시공할 것.		설계명 PROJECT TITLE NH농협은행 강릉 금융센터 신축공사		프로젝트번호 PROJECT CODE JP25-0001 승인 APPROVED BY 황진희 00.00.00		도면명 DRAWING TITLE 창호일람표-6																										
NH농협은행 (강원본부)		지안21 Tel. 02-6014-2137 / Fax. 02-6014-2138 Email: archjian21@naver.com				No. Date Revision Description Chkd.		협약실제 CONSULTANT 건축구조 : (주)탐앤지니어링 토목 : (주)제일기초이엔씨 전기/통신/소방 : (주)하랑엔지니어링		전문분야 SUBJECT 건축 검토 CHECKED BY 최용규 00.00.00		도면번호 DRAWING NO. A61-007																									
								설계단계 DESIGN PHASE 실시설계(변경) 신가영 00.00.00		A1: 1/50 A3: 1/100		실연번호 SHEET NO. 000 REV. No. △																									


형 태											
	창호 명칭	1 철제외여닫이문 (60분 방화문)		2 철제외여닫이문 (60분 방화문, 단열문)	3 철제양여닫이문 (60분 방화문, 단열문)	4 철제외여닫이문 (60분 방화문)					
	위치 및 개소	FSD 1~3층 EPS실, PS실 5 EA		FSD 1층 PS실 1 EA	FSD 물탱크실 1 EA	FSD 1층 계단실 1 EA					
	문틀 및 문짝	양면 T1.2 아연도강판 /내부 그라스울 충전 /정전분체도장		양면 T1.2 아연도강판 /내부 그라스울 충전 /정전분체도장		양면 T1.2 아연도강판 /내부 그라스울 충전 /정전분체도장					
	부 속 철 물	제작자 일식		제작자 일식		제작자 일식					
형 태											
	창호 명칭	5 철제외여닫이문 (60분 방화문, 단열문)		6 방화문, 방화창 / 고정창, 셰이프도어		1 철제외여닫이문					
	위치 및 개소	FSD 지붕 계단실 1 EA		FSD 2,3층 계단실 1 EA		SD 1층 창고 1 EA					
	문틀 및 문짝	양면 T1.2 아연도강판 /내부 그라스울 충전 /정전분체도장		필요 방화성능 충족		양면 T1.2 아연도강판 / 정전분체도장					
	유 리			THK 8mm 비차열유리							
부 속 철 물	제작자 일식		제작자 일식		제작자 일식						
형 태											
	창호 명칭	1 스텐레스 외여닫이문 (장애인 출입문)				1 서터문		2 서터문(60분 방화문)			
	위치 및 개소	SSD 2,3층 화장실 4 EA				1층 365 1 EA		1층 계단실 1 EA			
	문틀 및 문짝	스텐레스 스틸 외여닫이문, 고정창				스텐레스 스틸		스텐레스 스틸			
	유 리	50x150 T1.5 스텐레스 스틸 (헤어라인 마감) / 10T 강화유리(불투명시트)									
부 속 철 물	하드웨어 및 부속철물 일체				하드웨어 및 부속철물 일체		하드웨어 및 부속철물 일체				
건축주 CLIENT NH농협은행 (강원본부)		설계사무소 DESIGN OFFICE 지안21 건축사무소 Tel. 02-6014-2137 / Fax. 02-6014-2138 Email : archjian21@naver.com		NOTE 1. 창세트 에너지소비효율등급 기준 1등급 : 열관류율 R ≤ 0.9 (W/m²·K) /기밀성 1등급 2등급 : 0.9 ≤ R ≤ 1.2 /기밀성 1등급 3등급 : 1.2 ≤ R ≤ 1.8 /기밀성 2등급 이상 4등급 : 1.8 ≤ R ≤ 2.3 /기밀성 불지 않음 2. 모든 창호는 설계된 등급과 동등이상의 제품으로 시공할 것. 3. 창호 Bar, 유리, 벽판넬, 유리내측 벽 페인트의 색상은 감독관의 승인을 득하여 시공 할 것. 4. 모든 외벽 창호는 외부용 기밀, 방수테이프를 반드시 적용하여 시공할 것. 5. 기밀, 방수테이프의 폭은 해당제품 사양서에 따르며, 창호와 골조와의 간격이 넓을경우 충분한 접착면을 확보하도록 시공할 것.		설계명 PROJECT TITLE NH농협은행 강원 금융센터 신축공사 협력설계 CONSULTANT 건축구조 : (주)탐엔지니어링 토목 : (주) 제일기초이엔씨 전기/통신/소방 : (주)하랑엔지니어링		프로젝트번호 PROJECT CODE JP25-0001 승인 APPROVED BY 황진희 00.00.00 전문분야 SUBJECT 건축 검토 CHECKED BY 최용규 00.00.00 설계단계 DESIGN PHASE 실시설계(변경) 작성 Drawn By 신가영 00.00.00		도면명 DRAWING TITLE 창호일람표-7 도면번호 DRAWING NO. A61-008 축척 SCALE A1: 1/50 A3: 1/100 일련번호 SHEET NO. 000 REV. No. 1	

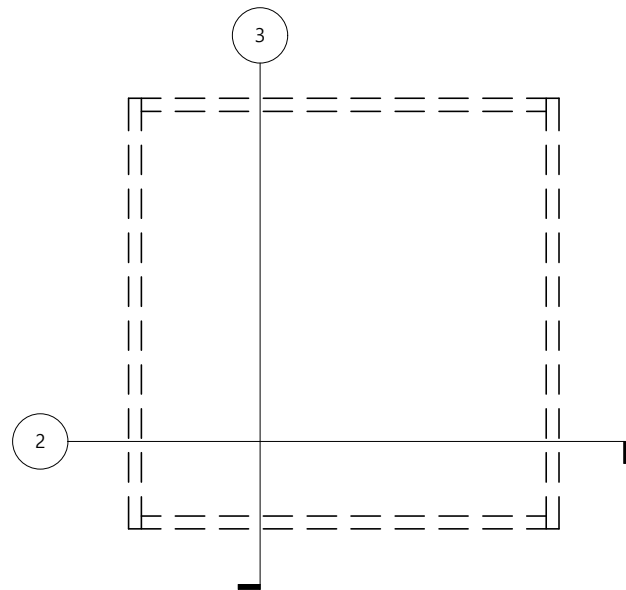

1 **ELEVATION VIEW**
AT 130MM SCALE : NONE(A3)




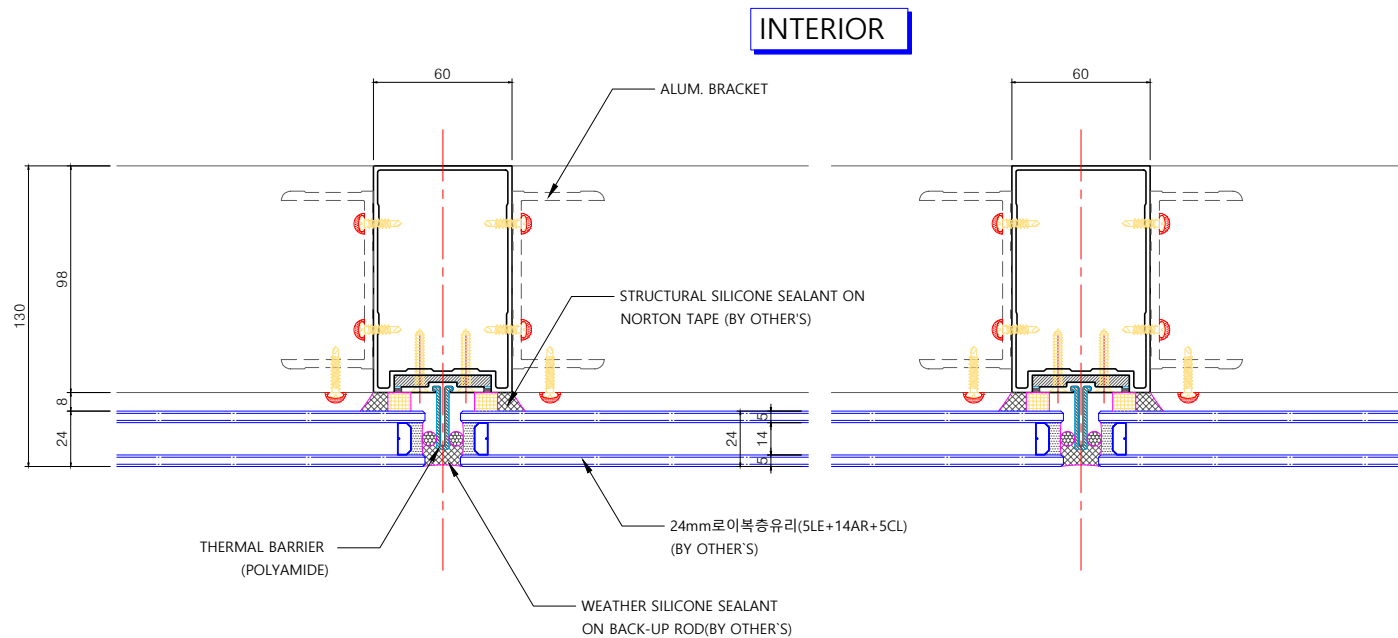


2 **HORIZONTAL SECTION DETAIL**
AT 130MM SCALE : 1/3(A3)

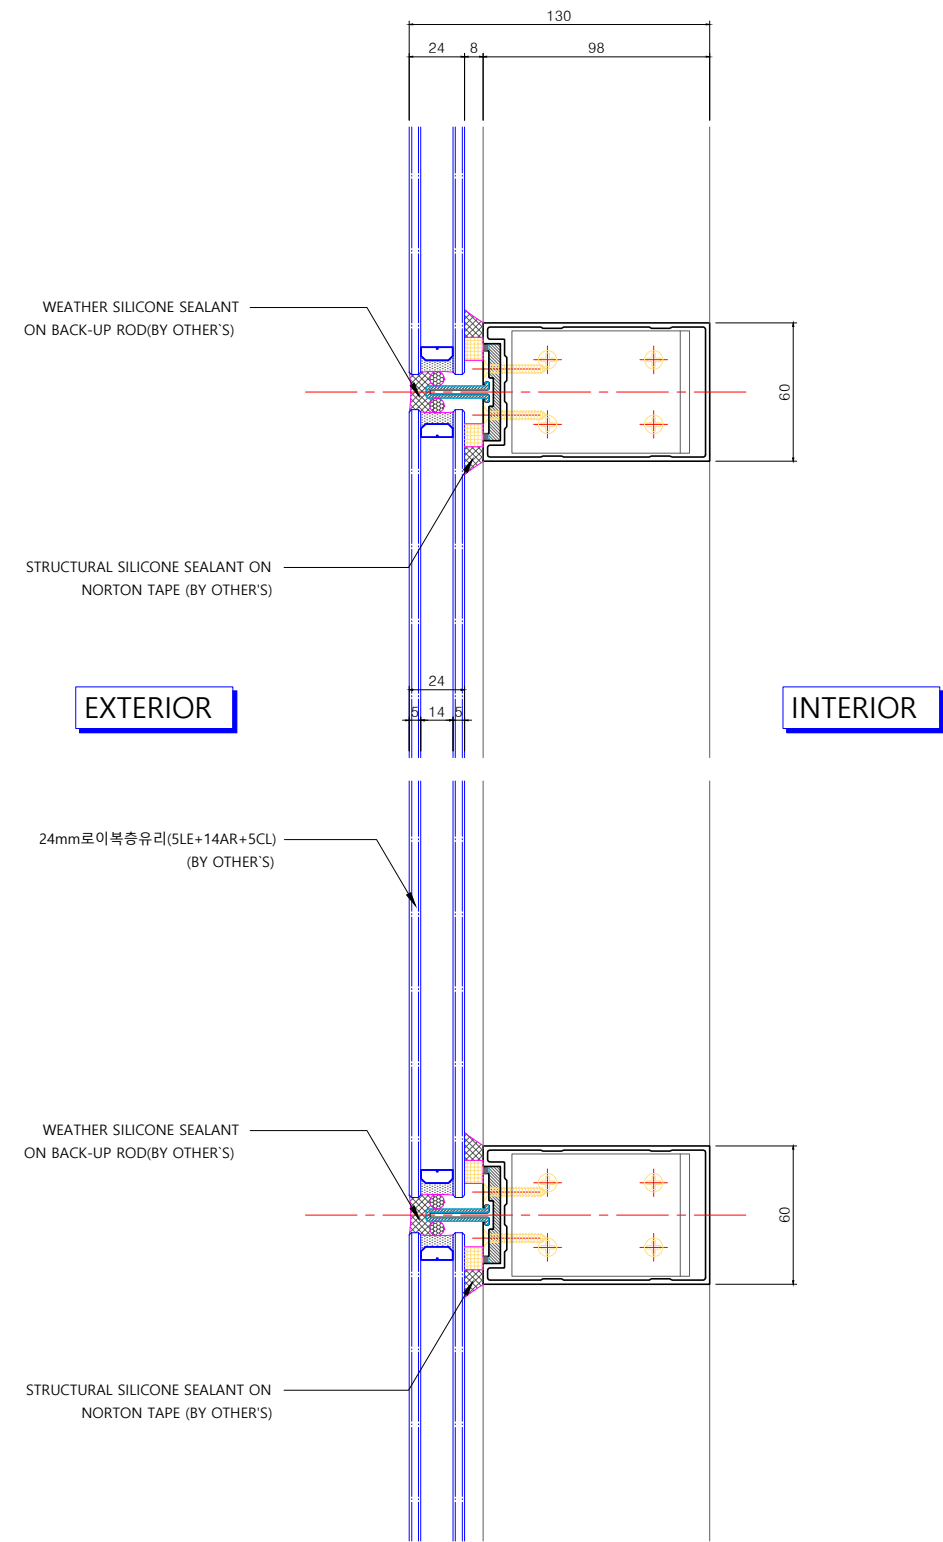

3 **VERTICAL SECTION DETAIL**
AT 130MM SCALE : 1/3(A3)

건축주 CLIENT  NH농협은행 (강원본부)	설계사무소 DESIGN OFFICE  건축사무소 지안21 Tel. 02-6014-2137 / Fax. 02-6014-2138 Email : archjian21@naver.com	NOTE.			설계명 PROJECT TITLE  NH농협은행 강릉 금융센터 신축공사	프로젝트번호 PROJECT CODE JP25-0001 승인 APPROVED BY 황진희 00.00.00	도면명 DRAWING TITLE 창호상세도-1 (하든 커튼월)			
					영역설계 CONSULTANT 건축구조 : (주)탐앤지니어링 토목 : (주) 제일기초이앤씨 전기/통신/소방 : (주)하랑엔지니어링	전문분야 SUBJECT 건축 최용규 00.00.00	검토 CHECKED BY 최용규 00.00.00	축척 SCALE A1: 1/1.5	도면번호 DRAWING NO. A62-001	
						설계단계 DESIGN PHASE 실시설계(변경) 신가영 00.00.00	작성 Drawn By 신가영 00.00.00		A3: 1/3	일련번호 SHEET NO. 000
										REV. No.
		No.	Date	Revision Description	Chkd.					

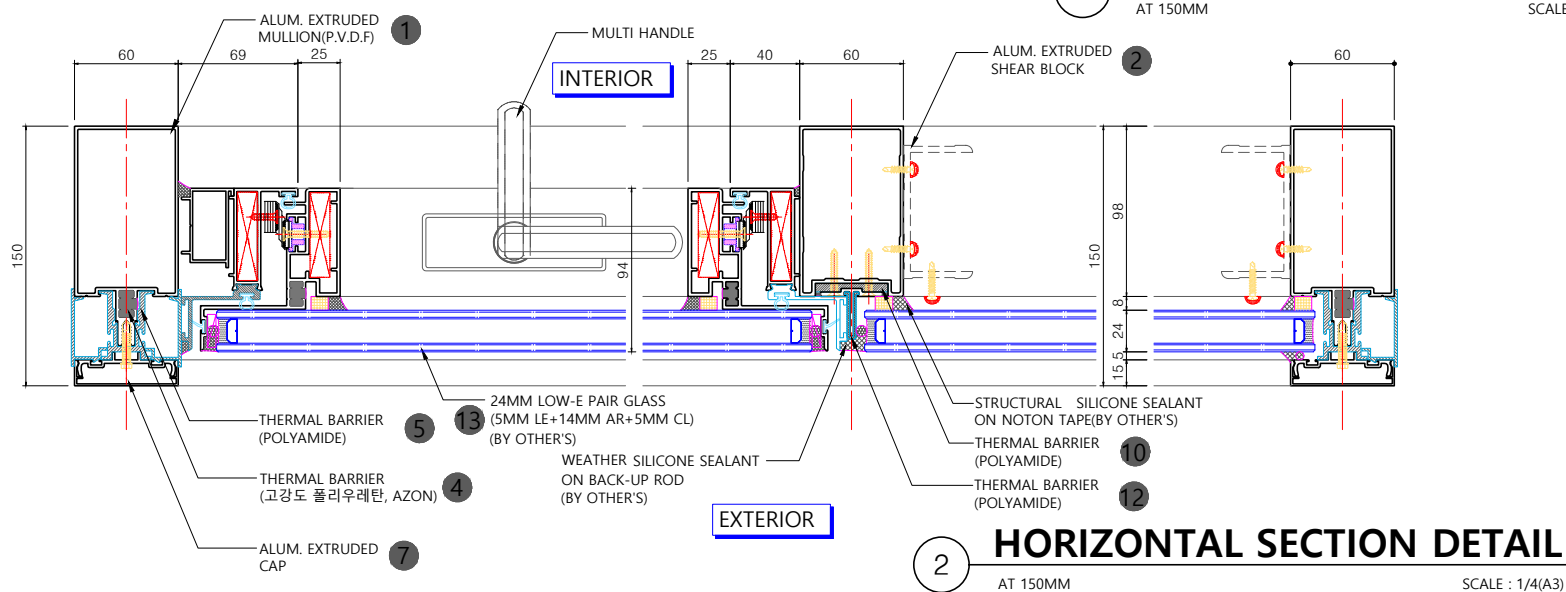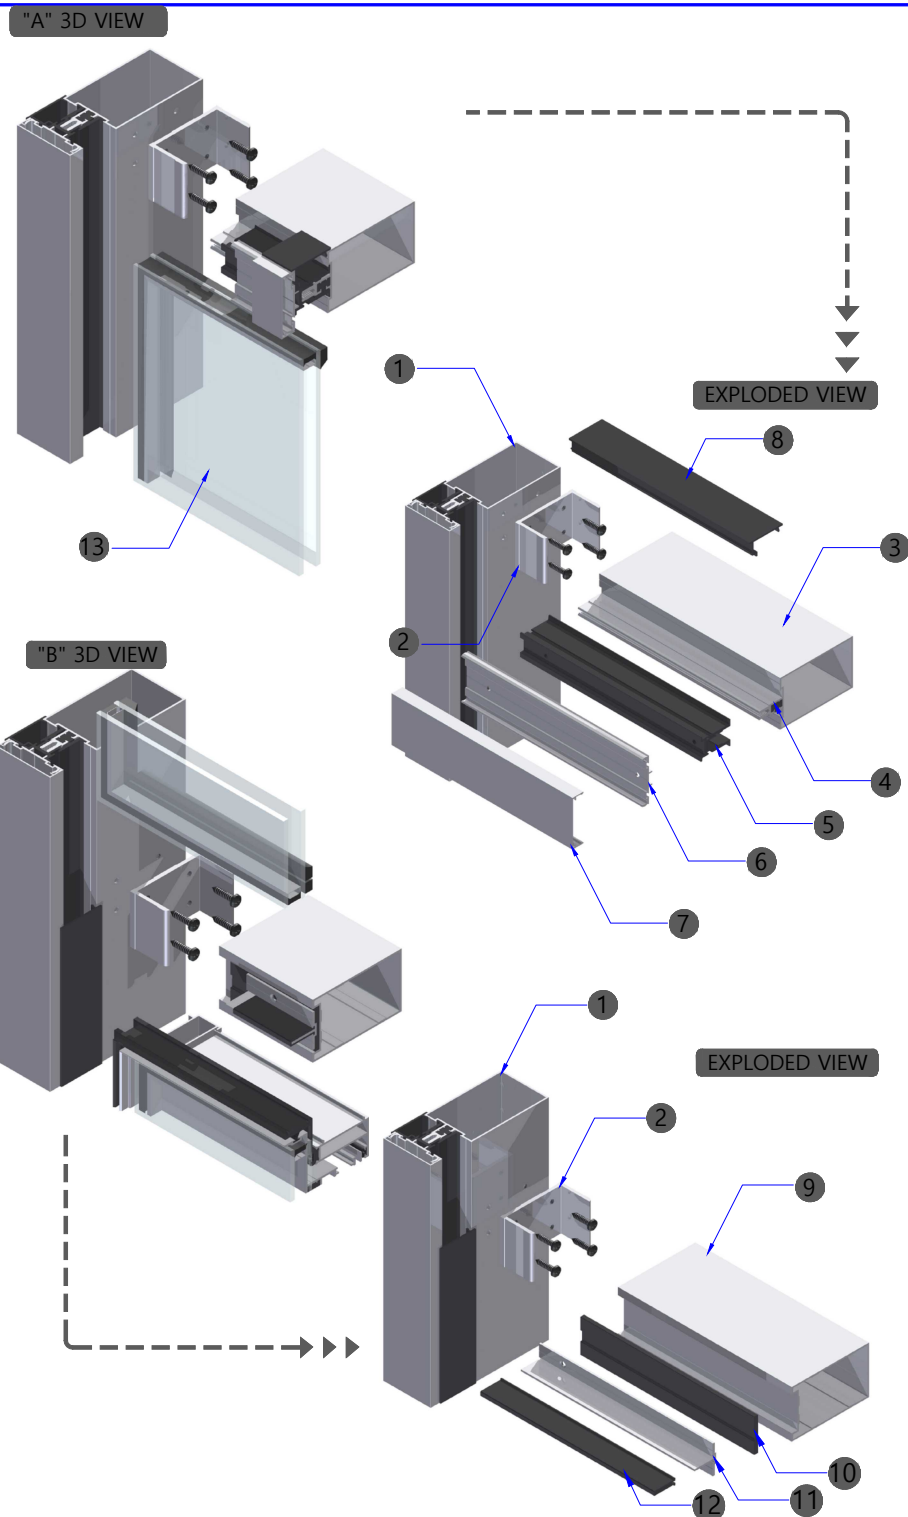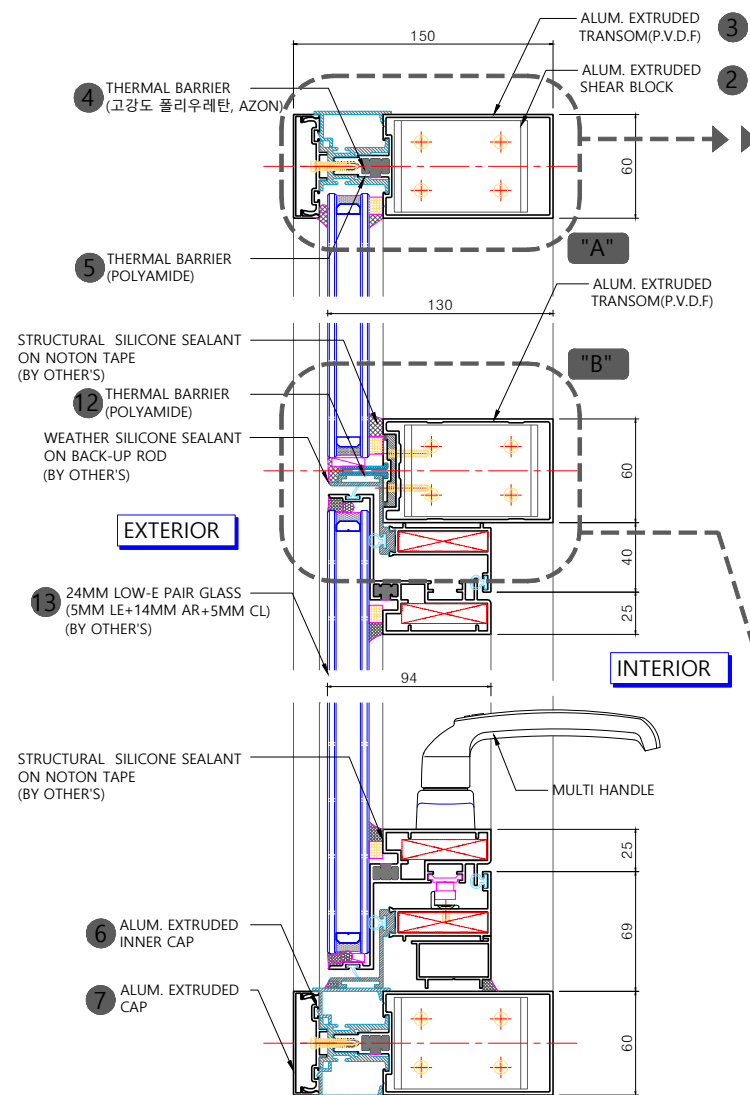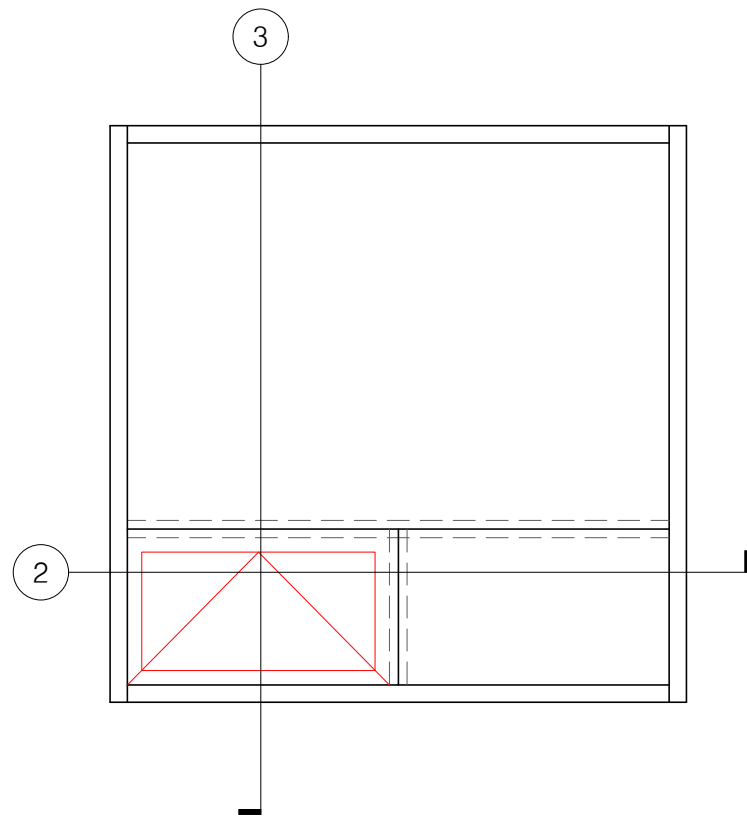

NO	자재명	NO	자재명
1	멀리온 (수직재, 알루미늄, 불소수지 2회)	9	트랜섬 (히든타입, 수평재, 알루미늄, 불소수지 2회)
2	연결 브라켓 (SHEAR BLOCK, 알루미늄, MF)	10	단열재 (폴리아미드)
3	트랜섬 (캡타입, 수평재, 알루미늄, 불소수지 2회)	11	"T" 몰딩 (히든바 측, 알루미늄, MF)
4	단열재 (고강도 폴리우레탄, AZON)	12	단열재 (폴리아미드)
5	단열재 (폴리아미드)	13	24MM 로이복층유리 (5LE + 14AR + 5CL)
6	캡 커넥터 (알루미늄, MF)		
7	외부 노출캡 (알루미늄, 불소수지 2회)		
8	홈마개 (폴리아미드)		

건축주
CLIENT
NH농협은행
(강원본부)

설계사무소
DESIGN OFFICE
지안21
Tel: 02-6014-2137 / Fax: 02-6014-2138
Email: archjian21@naver.com




NOTE.


No.	Date	Revision Description	Chkd.

설계명
PROJECT TITLE
NH농협은행
강릉 금융센터 신축공사
설계단계
DESIGN PHASE
실시설계(변경)

프로젝트번호
PROJECT CODE
JP25-0001
승인
APPROVED BY
황진희
00.00.00
검토
CHECKED BY
최용규
00.00.00
작성
Drawn By
신가영
00.00.00

도면명
DRAWING TITLE
창호상세도-2 (노출바+히든 프로젝트)
도면번호
DRAWING NO.
A62-002
축척
SCALE
A1: 1/2
A3: 1/4
일련번호
SHEET NO.
000
REV. No.
△

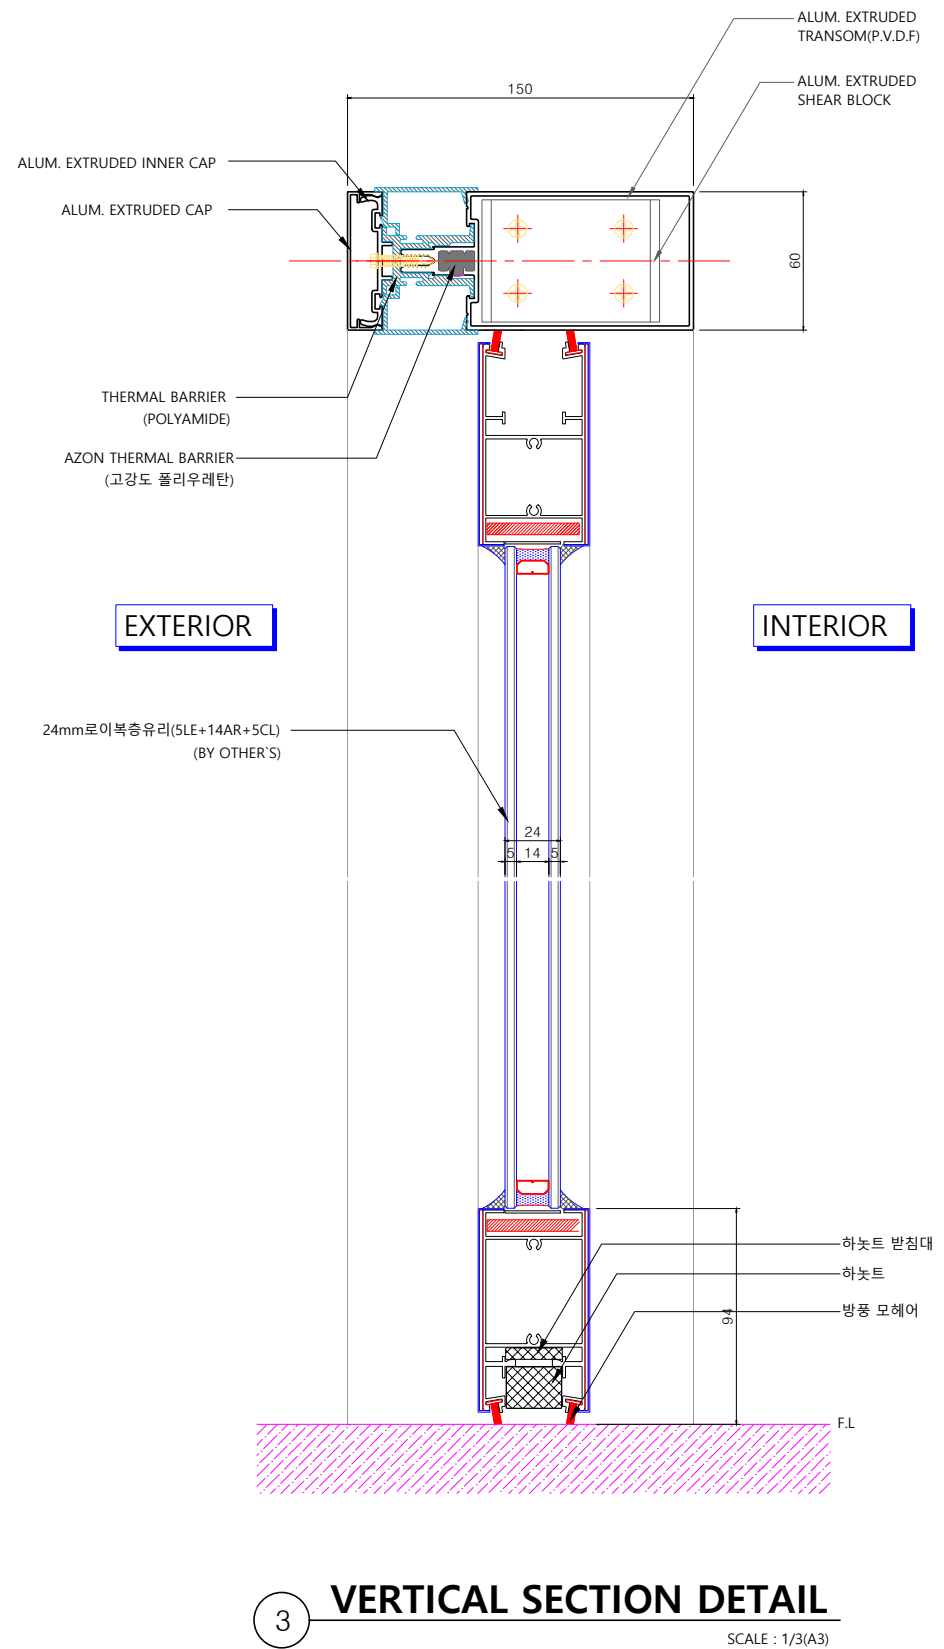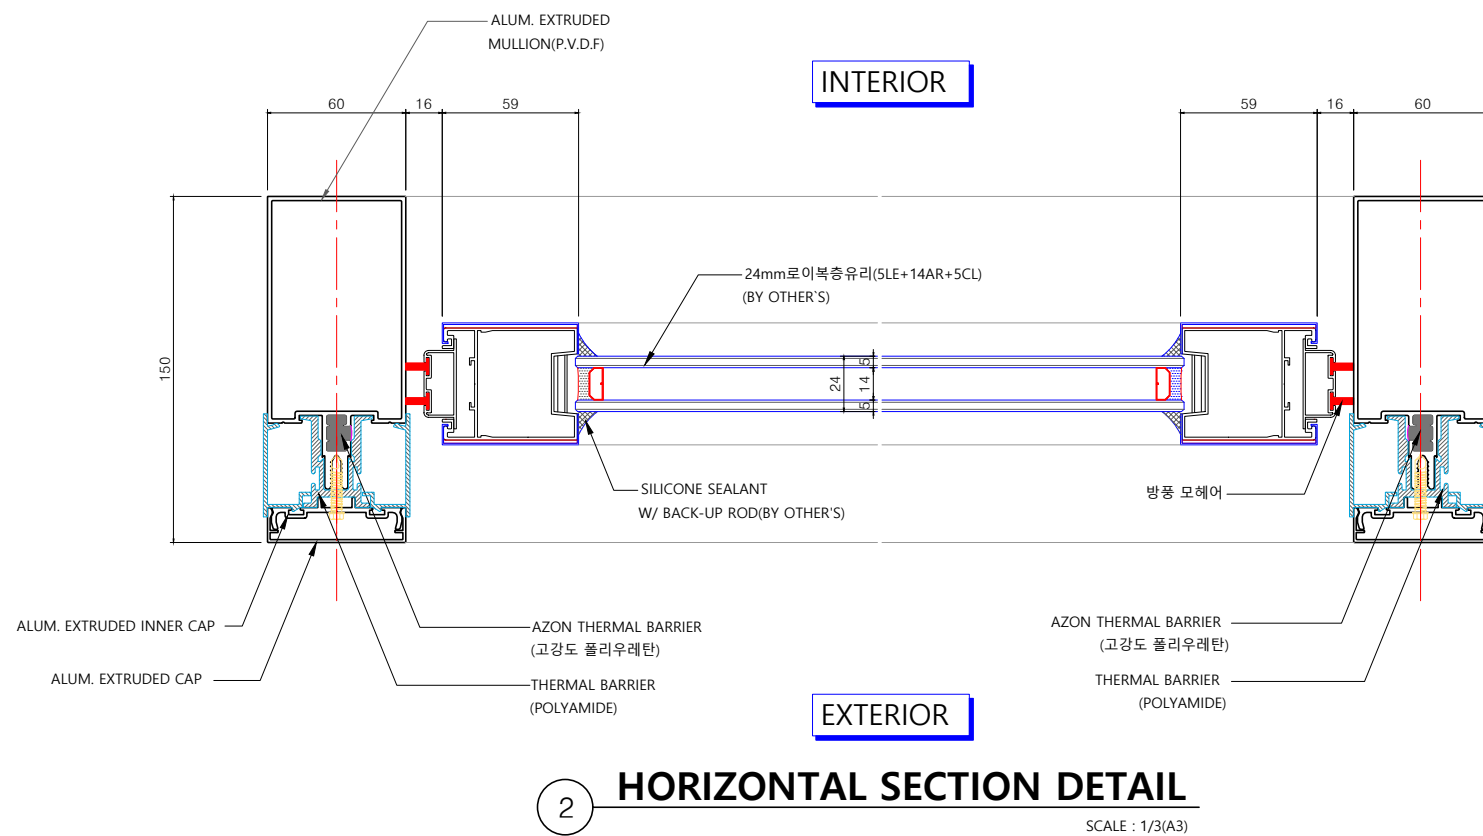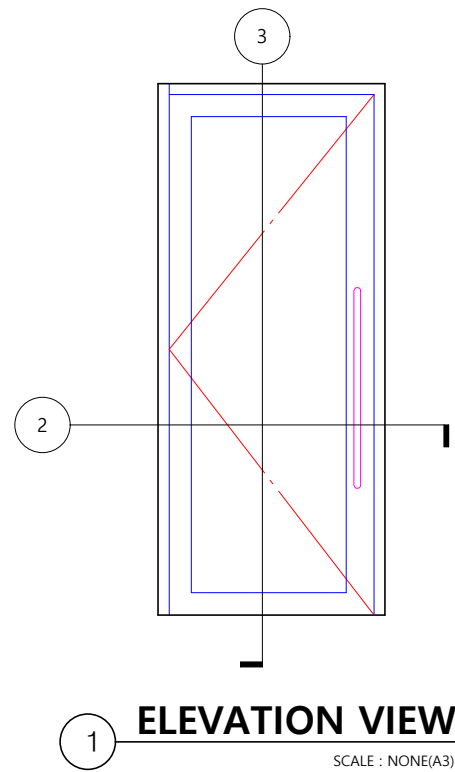

 건축주 CLIENT 	설계사무소 DESIGN OFFICE  Tel. 02-6014-2137 / Fax. 02-6014-2138 Email : archjian21@naver.com	NOTE.	△ △ △ △ <table><tr><th>No.</th><th>Date</th><th>Revision Description</th><th>Chkd.</th></tr></table>	No.	Date	Revision Description	Chkd.	설계명 PROJECT TITLE 	프로젝트번호 PROJECT CODE JP25-0001 승인 APPROVED BY 황진희 00.00.00	도면명 DRAWING TITLE 창호상세도-3 (세이프도어)		
		No.	Date	Revision Description	Chkd.							
		협력설계 CONSULTANT 건축구조 : (주)탐엔지니어링 토목 : (주) 제일기초이엔씨 전기/통신/소방 : (주)하랑엔지니어링	전문분야 SUBJECT 건축 검토 CHECKED BY 최용규 00.00.00	작성 Drawn By 설계단계 DESIGN PHASE 실시설계(변경) 신가영 00.00.00	축척 SCALE A1: 1/1.5 A3: 1/3	도면번호 DRAWING NO. A62-003	도면번호 SHEET NO. 000	REV. NO. △				



건축주 CLIENT 	설계사무소 DESIGN OFFICE  Tel. 02-6014-2137 / Fax. 02-6014-2138 Email : archjian21@naver.com	NOTE.	△				설계명 PROJECT TITLE  NH농협은행  강릉 금융센터 신축공사 협력설계 CONSULTANT 건축구조 : (주)탐맥지니어링 도록 : (주) 제일기조이엔씨 전기/통신/소방 : (주)하랑엔지니어링	프로젝트번호 PROJECT CODE JP25-0001 건축 설계단계 DESIGN PHASE 실시설계(변경)	승인 APPROVED BY 황진희 00.00.00 최용규 00.00.00 작성 Drawn By 신가영 00.00.00	도면명 DRAWING TITLE 창호상세도-4 (시스템도어)			
			△							축척 SCALE A1: 1/1.5 A3: 1/3	도면번호 DRAWING NO. A62-004		
			△								일련번호 SHEET NO. 000	REV. NO. 	
			No.	Date	Revision Description	Chkd.							