



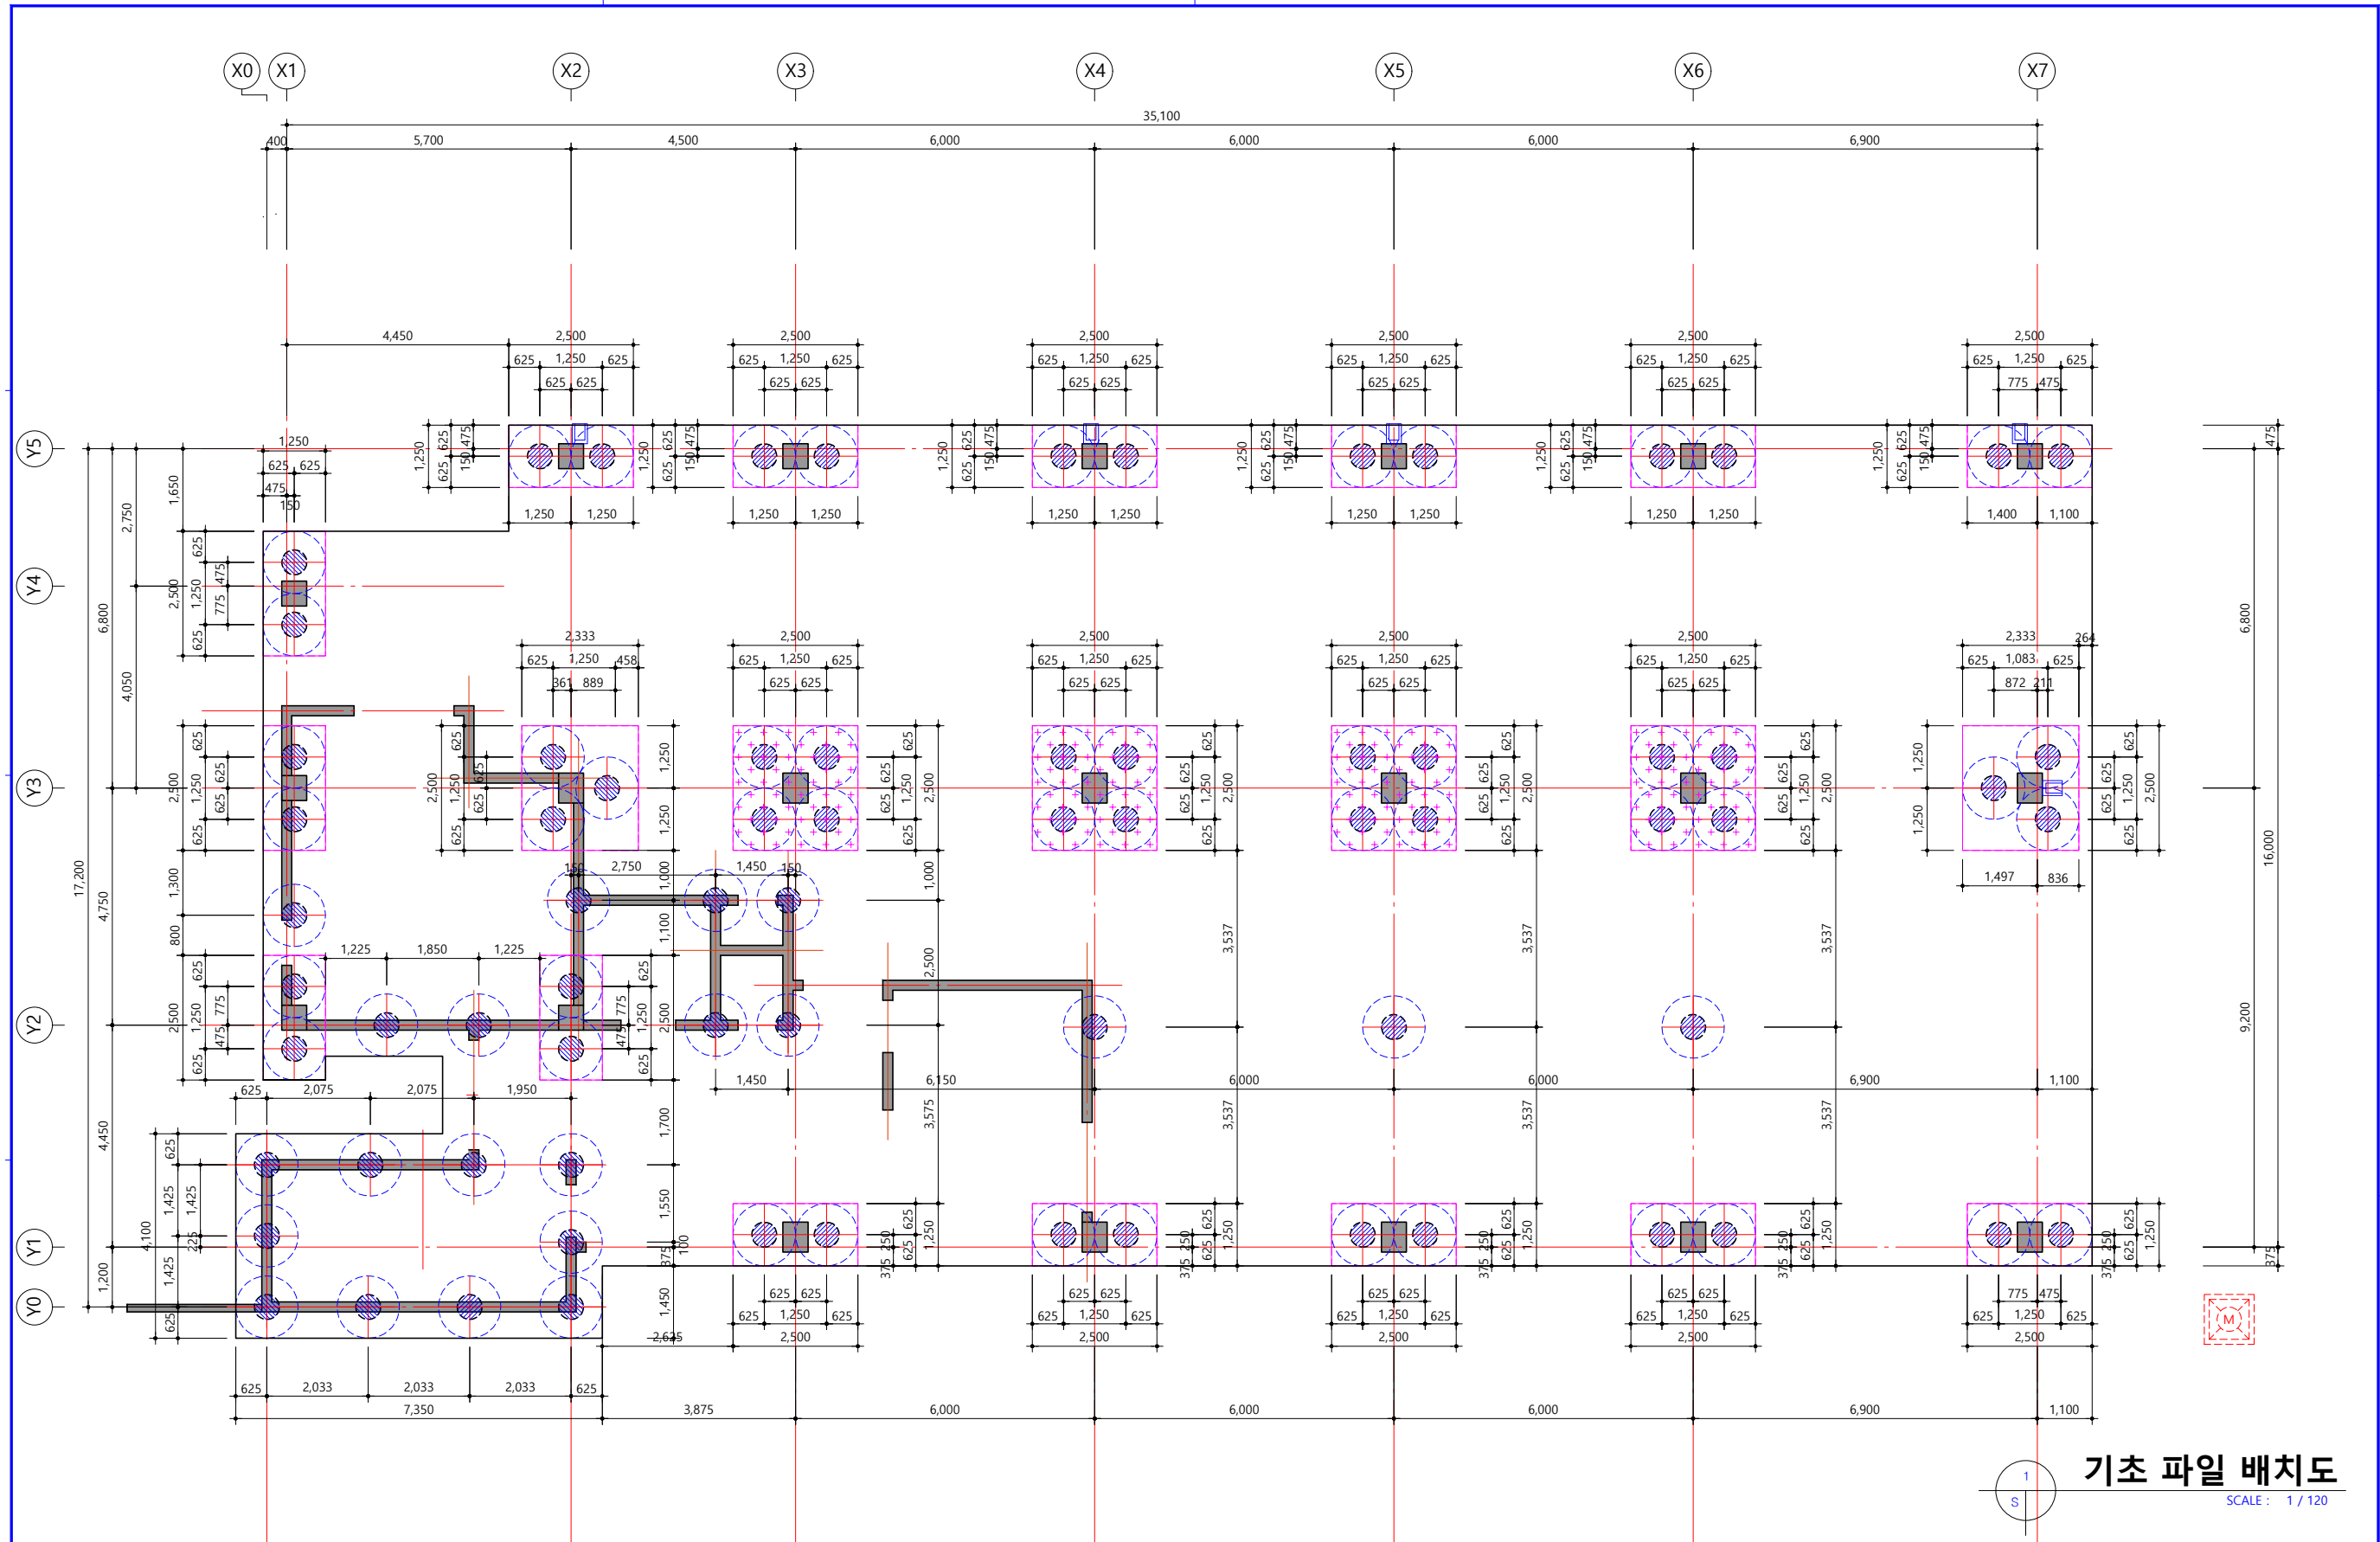


건축주 CLIENT	NH농협은행 (강원본부)	건축사무소 지안21 Tel. 02-6014-2137 / Fax: 02-6014-2138 Email : archjian21@naver.com	NOTE.	1. 콘크리트 : fck = 27MPa / 철근 : fy = 400MPa			△				설계명 PROJECT TITLE	NH농협은행		프로젝트번호 PROJECT CODE	승인 APPROVED BY		도면명 DRAWING TITLE	기초 파일 배치도		
			3. 파일기초			△				강릉 금융센터 신축공사		JP25-0001	황진희 00.00.00							
			- PHC PILE D500 허용지지력(fp)=900kN/ea			△				협력설계 CONSULTANT		건축구조 : (주)탐앤지니어링 토목 : (주)제일기조이엔씨 전기/통신/소방 : (주)하랑엔지니어링	건축	최용규 00.00.00	작성 Drawn By 신가영 00.00.00	출척 SCALE		A1: 1/60	도면번호 DRAWING NO. S11-002	
			- PILE의 길이 및 지지력은 시향타에 의해 확인 후 시공할 것.			△														
			No.	Date	Revision Description	Chkd.														

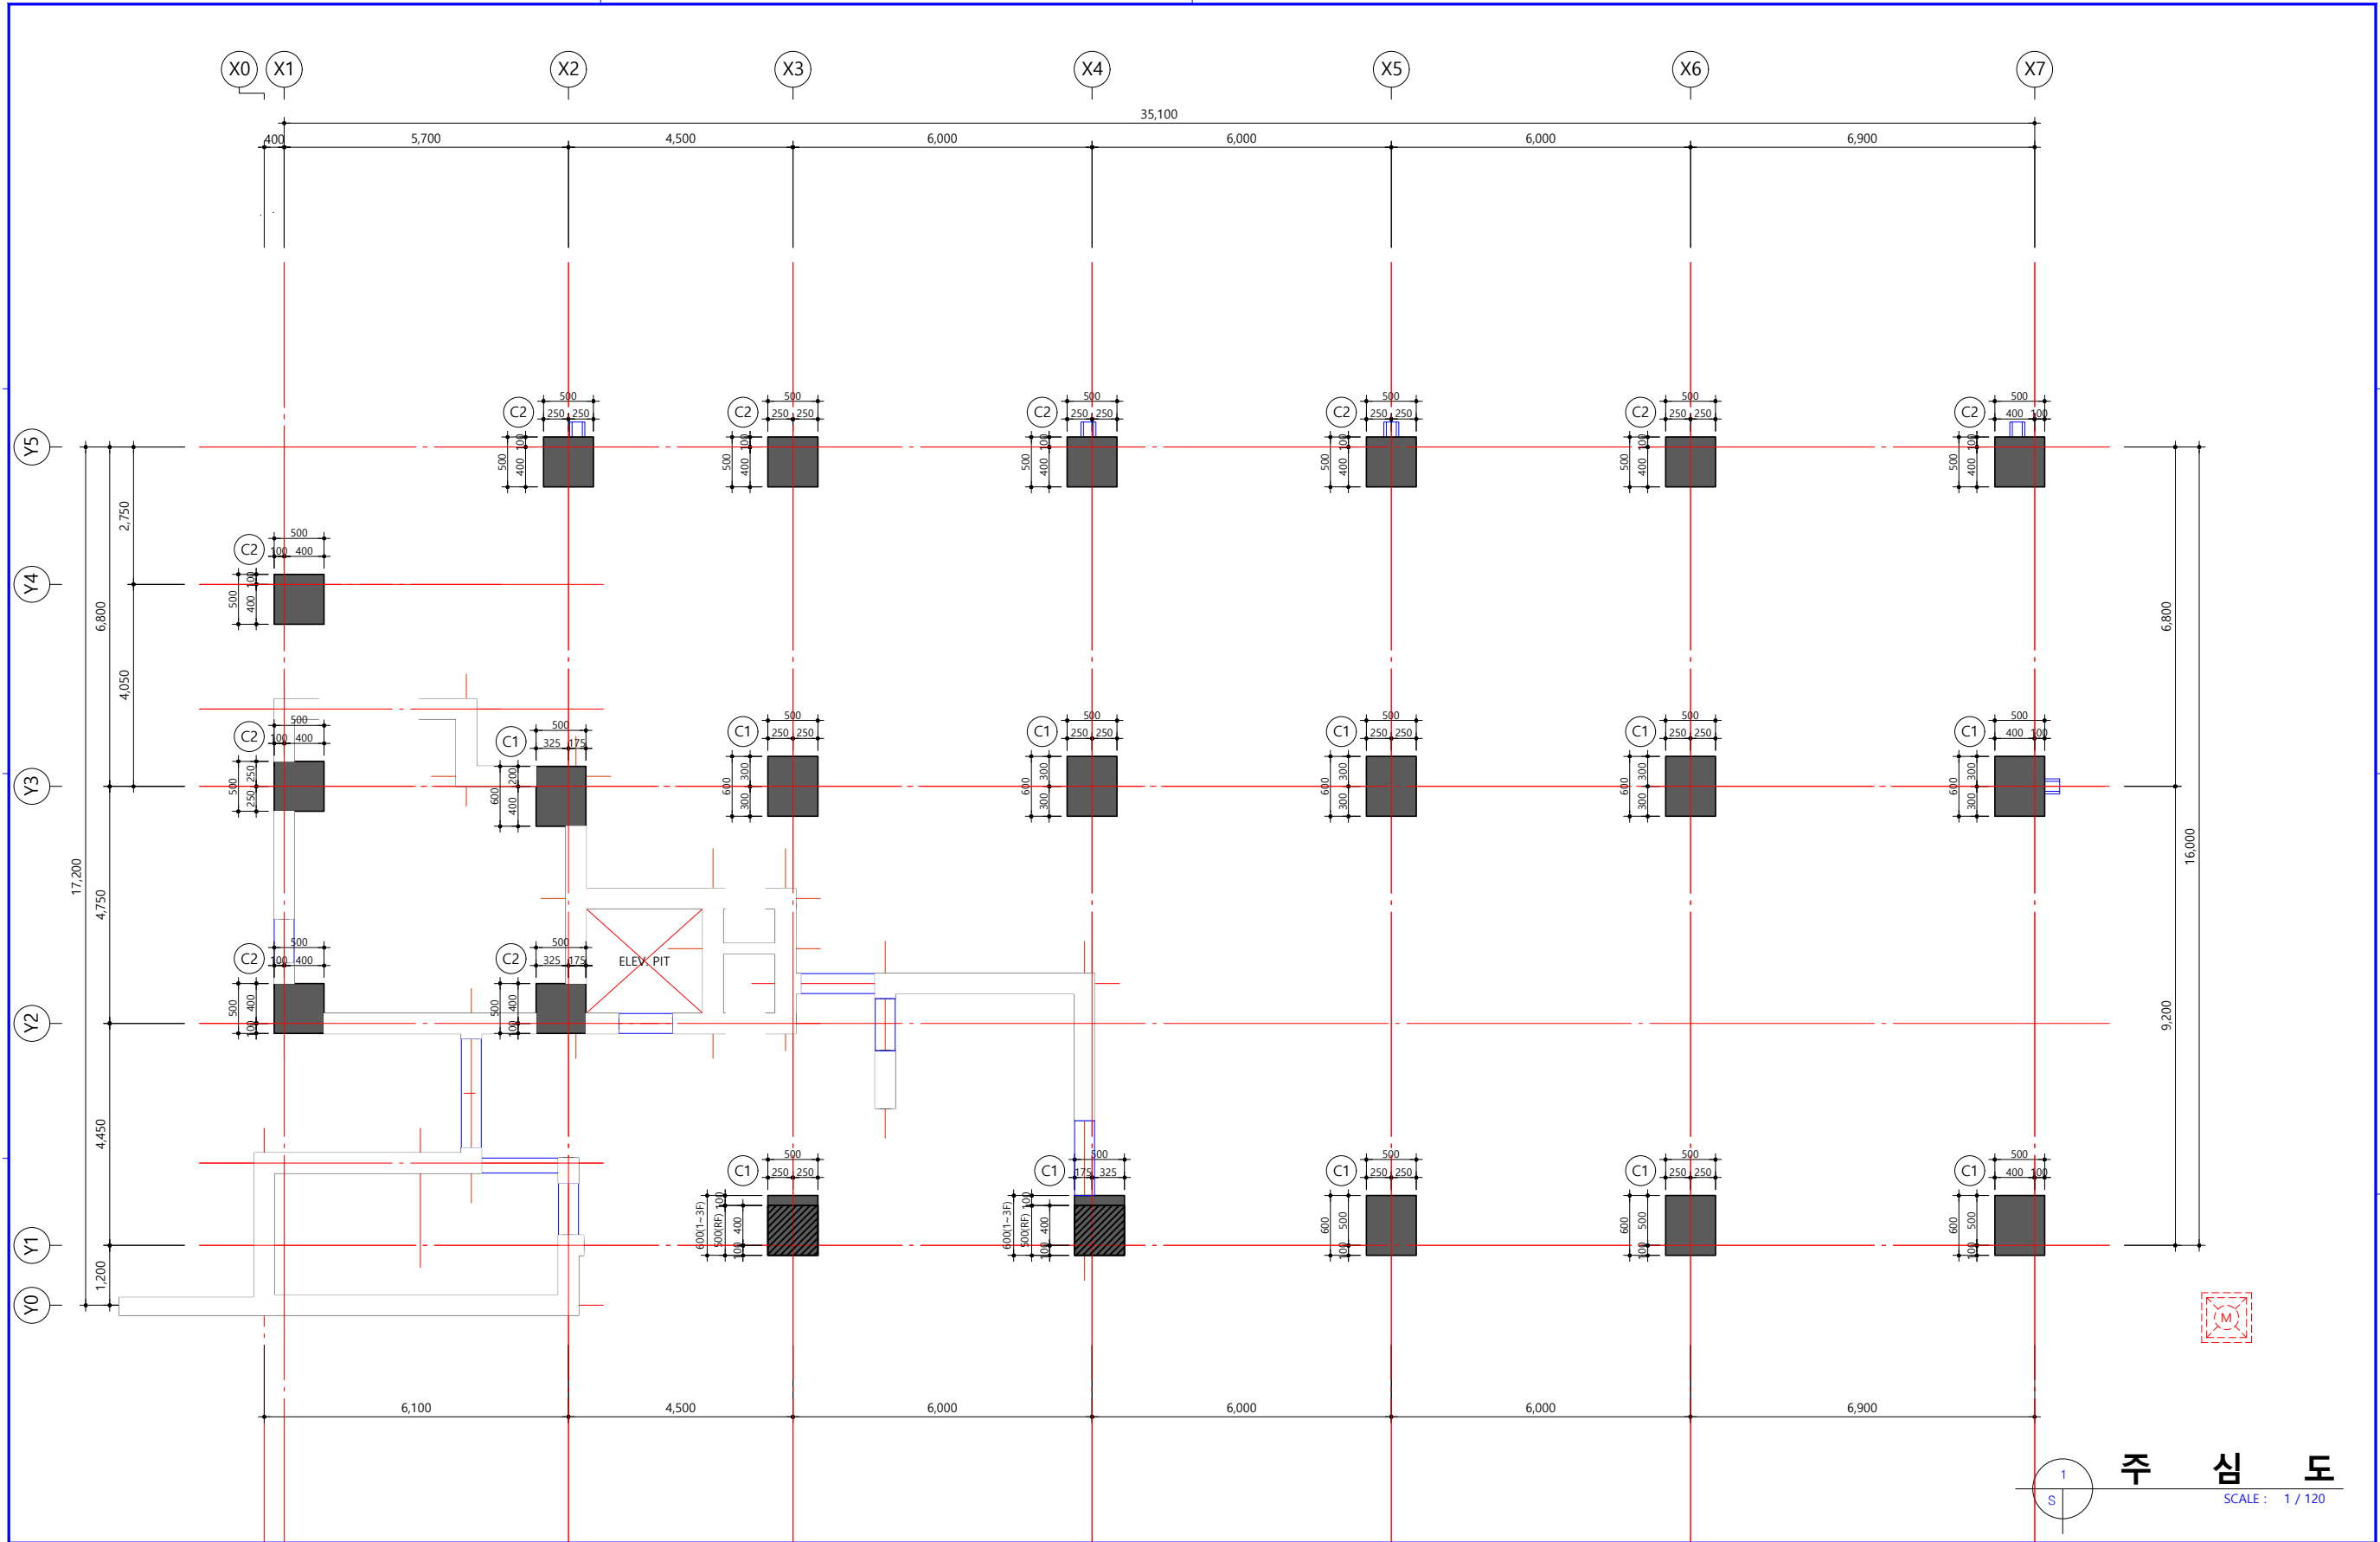

1
S
주심도
SCALE: 1/120

건축주 CLIENT   Tel. 02-6014-2137 / Fax. 02-6014-2138 Email: archjian21@naver.com	설계사무소 DESIGN OFFICE	NOTE. 1. 콘크리트 : fck = 27MPa / 철근 : fy = 400MPa 3. 파일기초 - PHC PILE D500 허용지지력(fp)=900kN/ea - PILE의 길이 및 지지력은 시황타에 의해 확인 후 시공할 것.				설계명 PROJECT TITLE 	프로젝트번호 PROJECT CODE JP25-0001 승인 APPROVED BY 황진희 00.00.00	도면명 DRAWING TITLE 주심도					
								영역설계 CONSULTANT 건축구조 : (주)탐앤지니어링 토목 : (주)제일기초이엔씨 전기/통신/소방 : (주)하랑엔지니어링	전문분야 SUBJECT 건축 검토 CHECKED BY 최용규 00.00.00	축척 SCALE A1: 1/60 A3: 1/120	도면번호 DRAWING NO. S11-003	일련번호 SHEET NO. 000	REV. No. 
													
			No.	Date	Revision Description			Chkd.			설계단계 DESIGN PHASE 실시설계(변경) 작성 Drawn By 신가영 00.00.00		

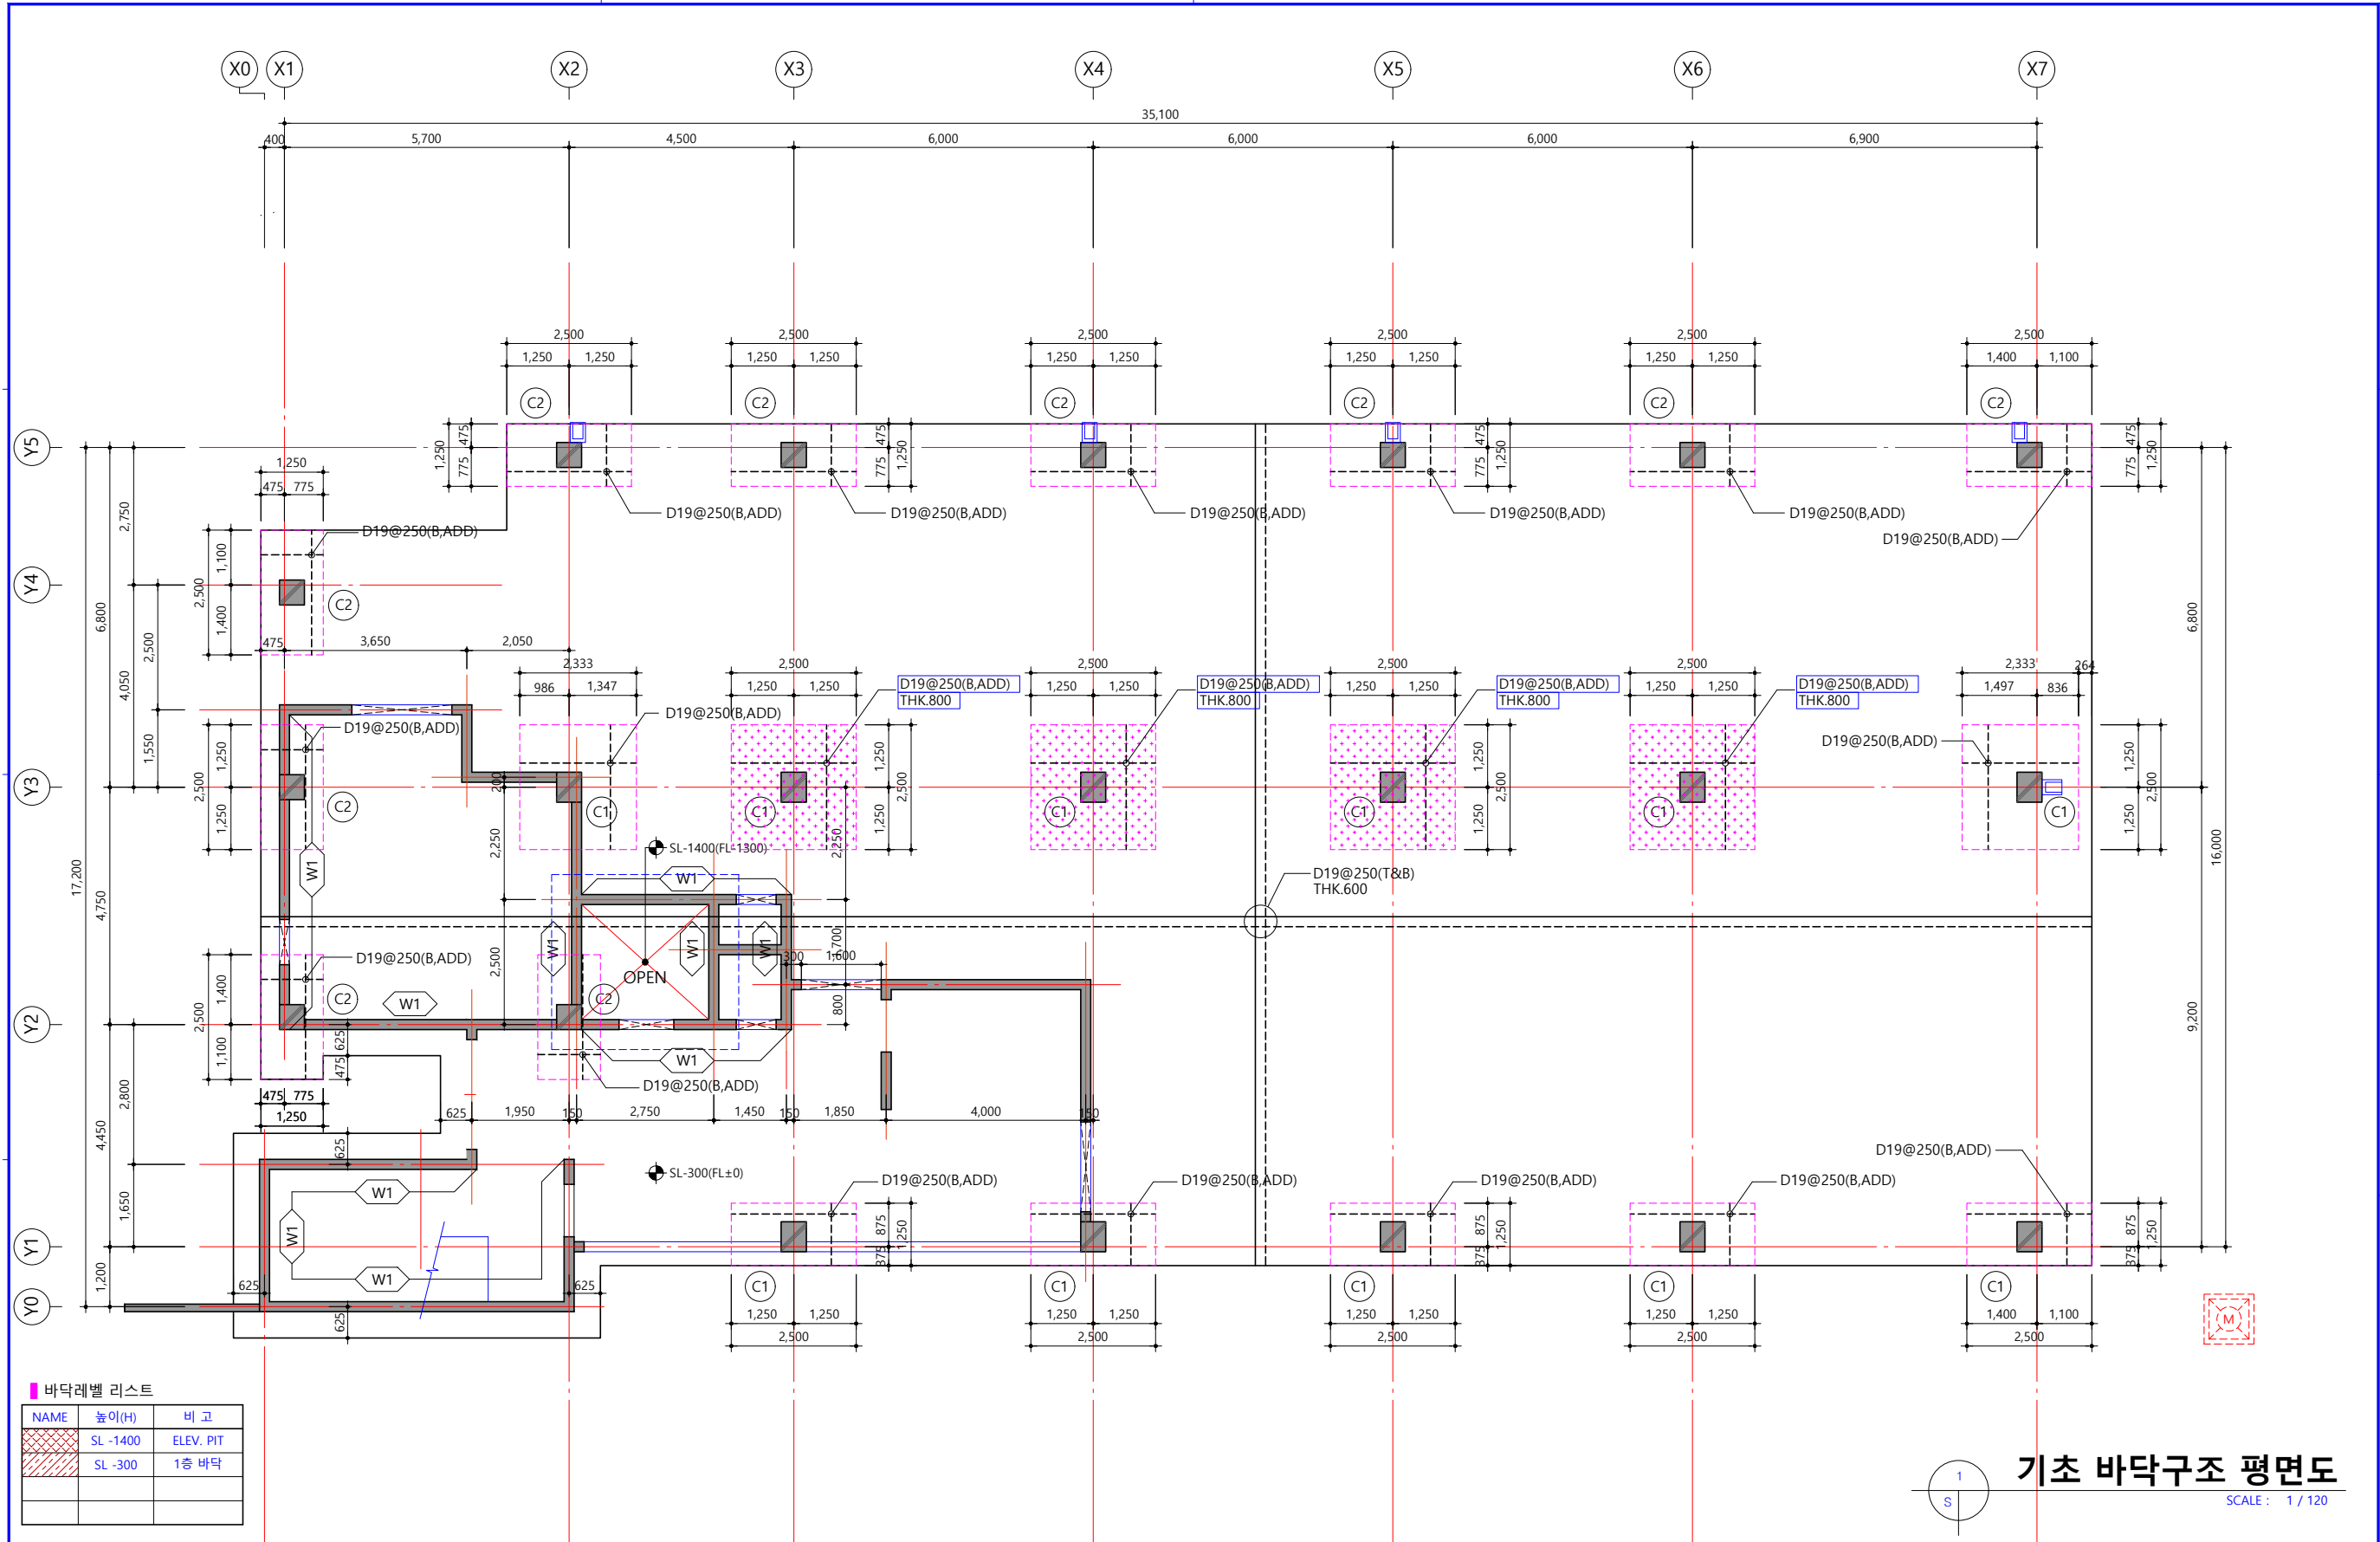


바닥레벨 리스트		
NAME	높이(H)	비고
	SL -1400	ELEV. PIT
	SL -300	1층 바닥

1
S

기초 바닥구조 평면도
SCALE : 1 / 120

건축주 CLIENT	설계사무소 DESIGN OFFICE	건축사무소 지안21 Tel. 02-6014-2137 / Fax. 02-6014-2138 Email : archjian21@naver.com	NOTE.				설계명 PROJECT TITLE		프로젝트번호 PROJECT CODE	승인 APPROVED BY	도면명 DRAWING TITLE						
						강릉 금융센터 신축공사		JP25-0001	황진희 00.00.00	기초 바닥구조 평면도							
						현장설계 CONSULTANT		건축	검토 CHECKED BY	최용규 00.00.00	축척 SCALE	A1: 1/60	도면번호 DRAWING NO.	S11-004			
						건축구조 : (주)탐앤지니어링 토목 : (주) 제일기조이엔씨 전기/통신/소방 : (주)하랑엔지니어링		설계단계 DESIGN PHASE	작성 Drawn By	실시설계(변경)					신가영 00.00.00	A3: 1/120	일련번호 SHEET NO.
						No.	Date	Revision Description	Chkd.								

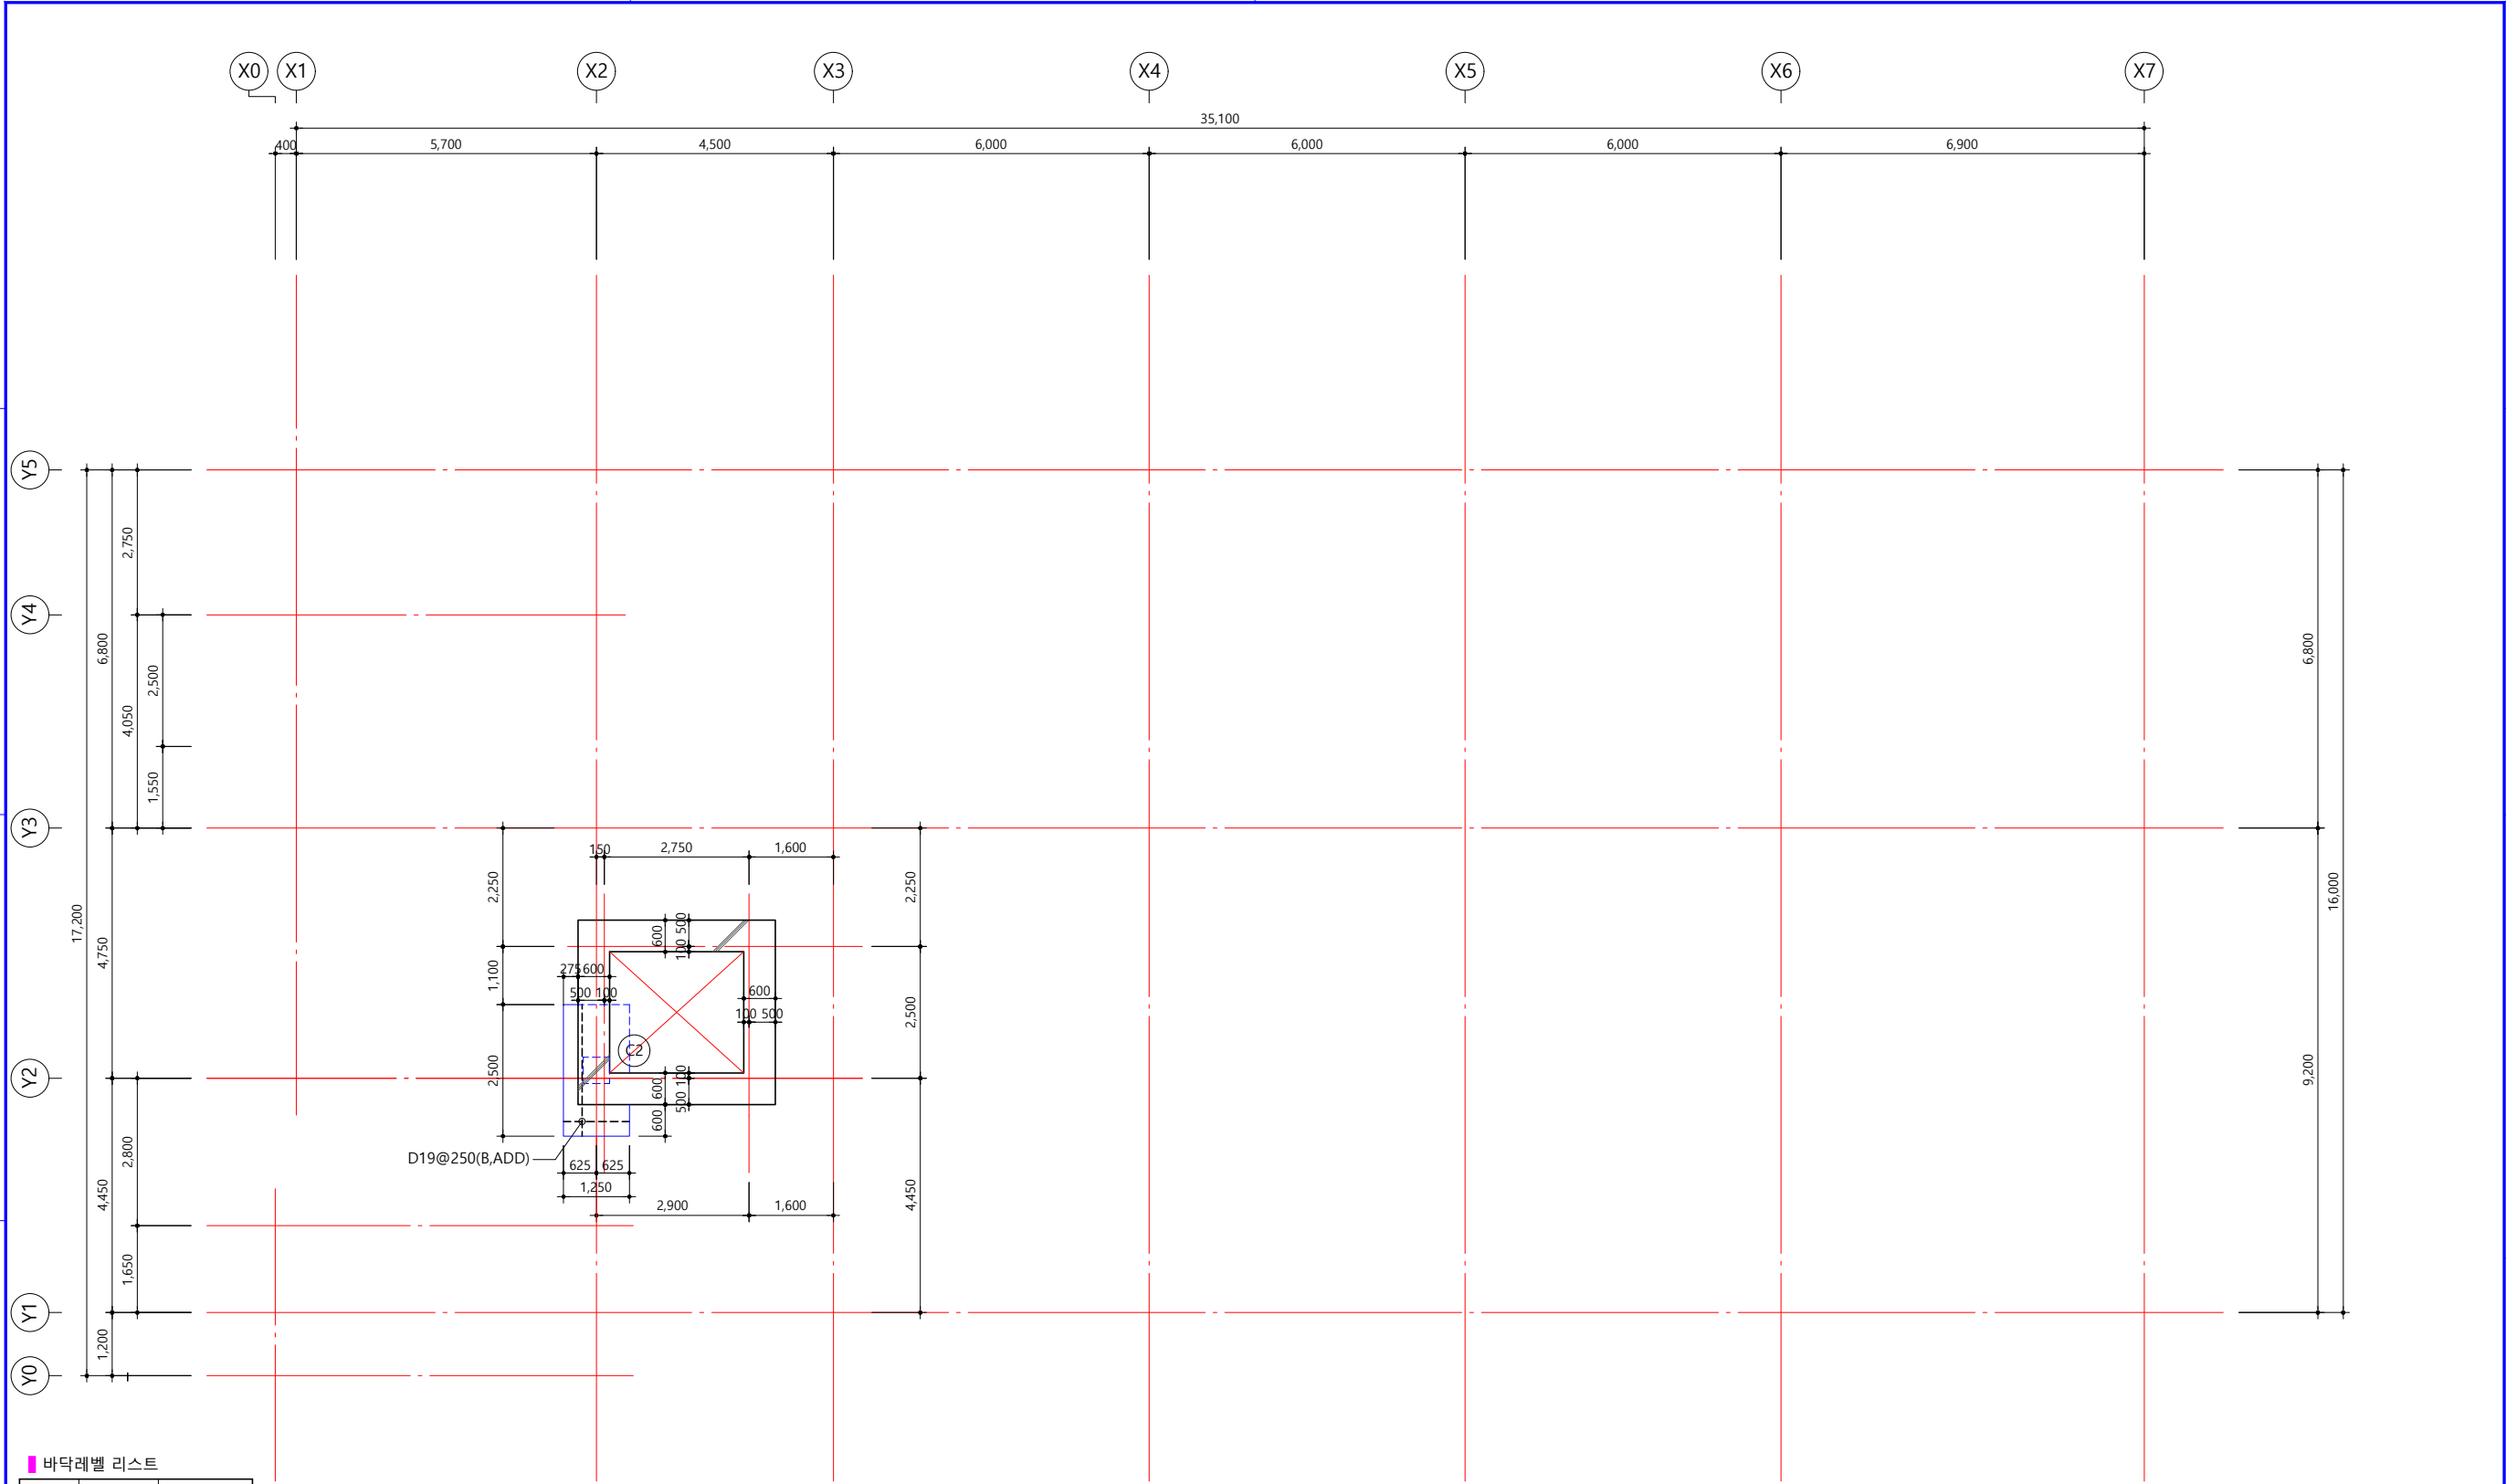


바닥레벨 리스트

NAME	높이(H)	비 고
SL -1400		ELEV. PIT

PIT 바닥 구조 평면도
SCALE : 1 / 120

건축주 CLIENT 	설계사무소 DESIGN OFFICE 건축사사무소 지안21 Tel. 02-6014-2137 / Fax. 02-6014-2138 Email : archjian21@naver.com	NOTE. 1. 콘크리트 : fck = 27MPa / 철근 : fy = 400MPa 2. 미표기 벽체 : W2 3. 외부에 노출되는 콘크리트는 방수처리 할 것 4. 미표기 슬라브 : S2 5. 파일기초 - PHC PILE D500 허용지지력(fp)=900kN/ea - PILE의 길이 및 지지력은 시향타에 의해 확인 후 시공할 것.	1			설계명 PROJECT TITLE NH농협은행 강릉 금융센터 신축공사	프로젝트번호 PROJECT CODE JP25-0001	승인 APPROVED BY 황진희 00.00.00	도면명 DRAWING TITLE PIT 바닥 구조 평면도						
			2												
			3						영역설계 CONSULTANT 건축구조 : (주)탐엔지니어링 토목 : (주) 제일기초이엔씨 전기/통신/소방 : (주)하랑엔지니어링	전문분야 SUBJECT 건축	검토 CHECKED BY 최용규 00.00.00	축척 SCALE A1: 1/60 A3: 1/120	도면번호 DRAWING NO. S11-005	일련번호 SHEET NO. 000	REV. No. 1
			4												
			5	No.	Date										

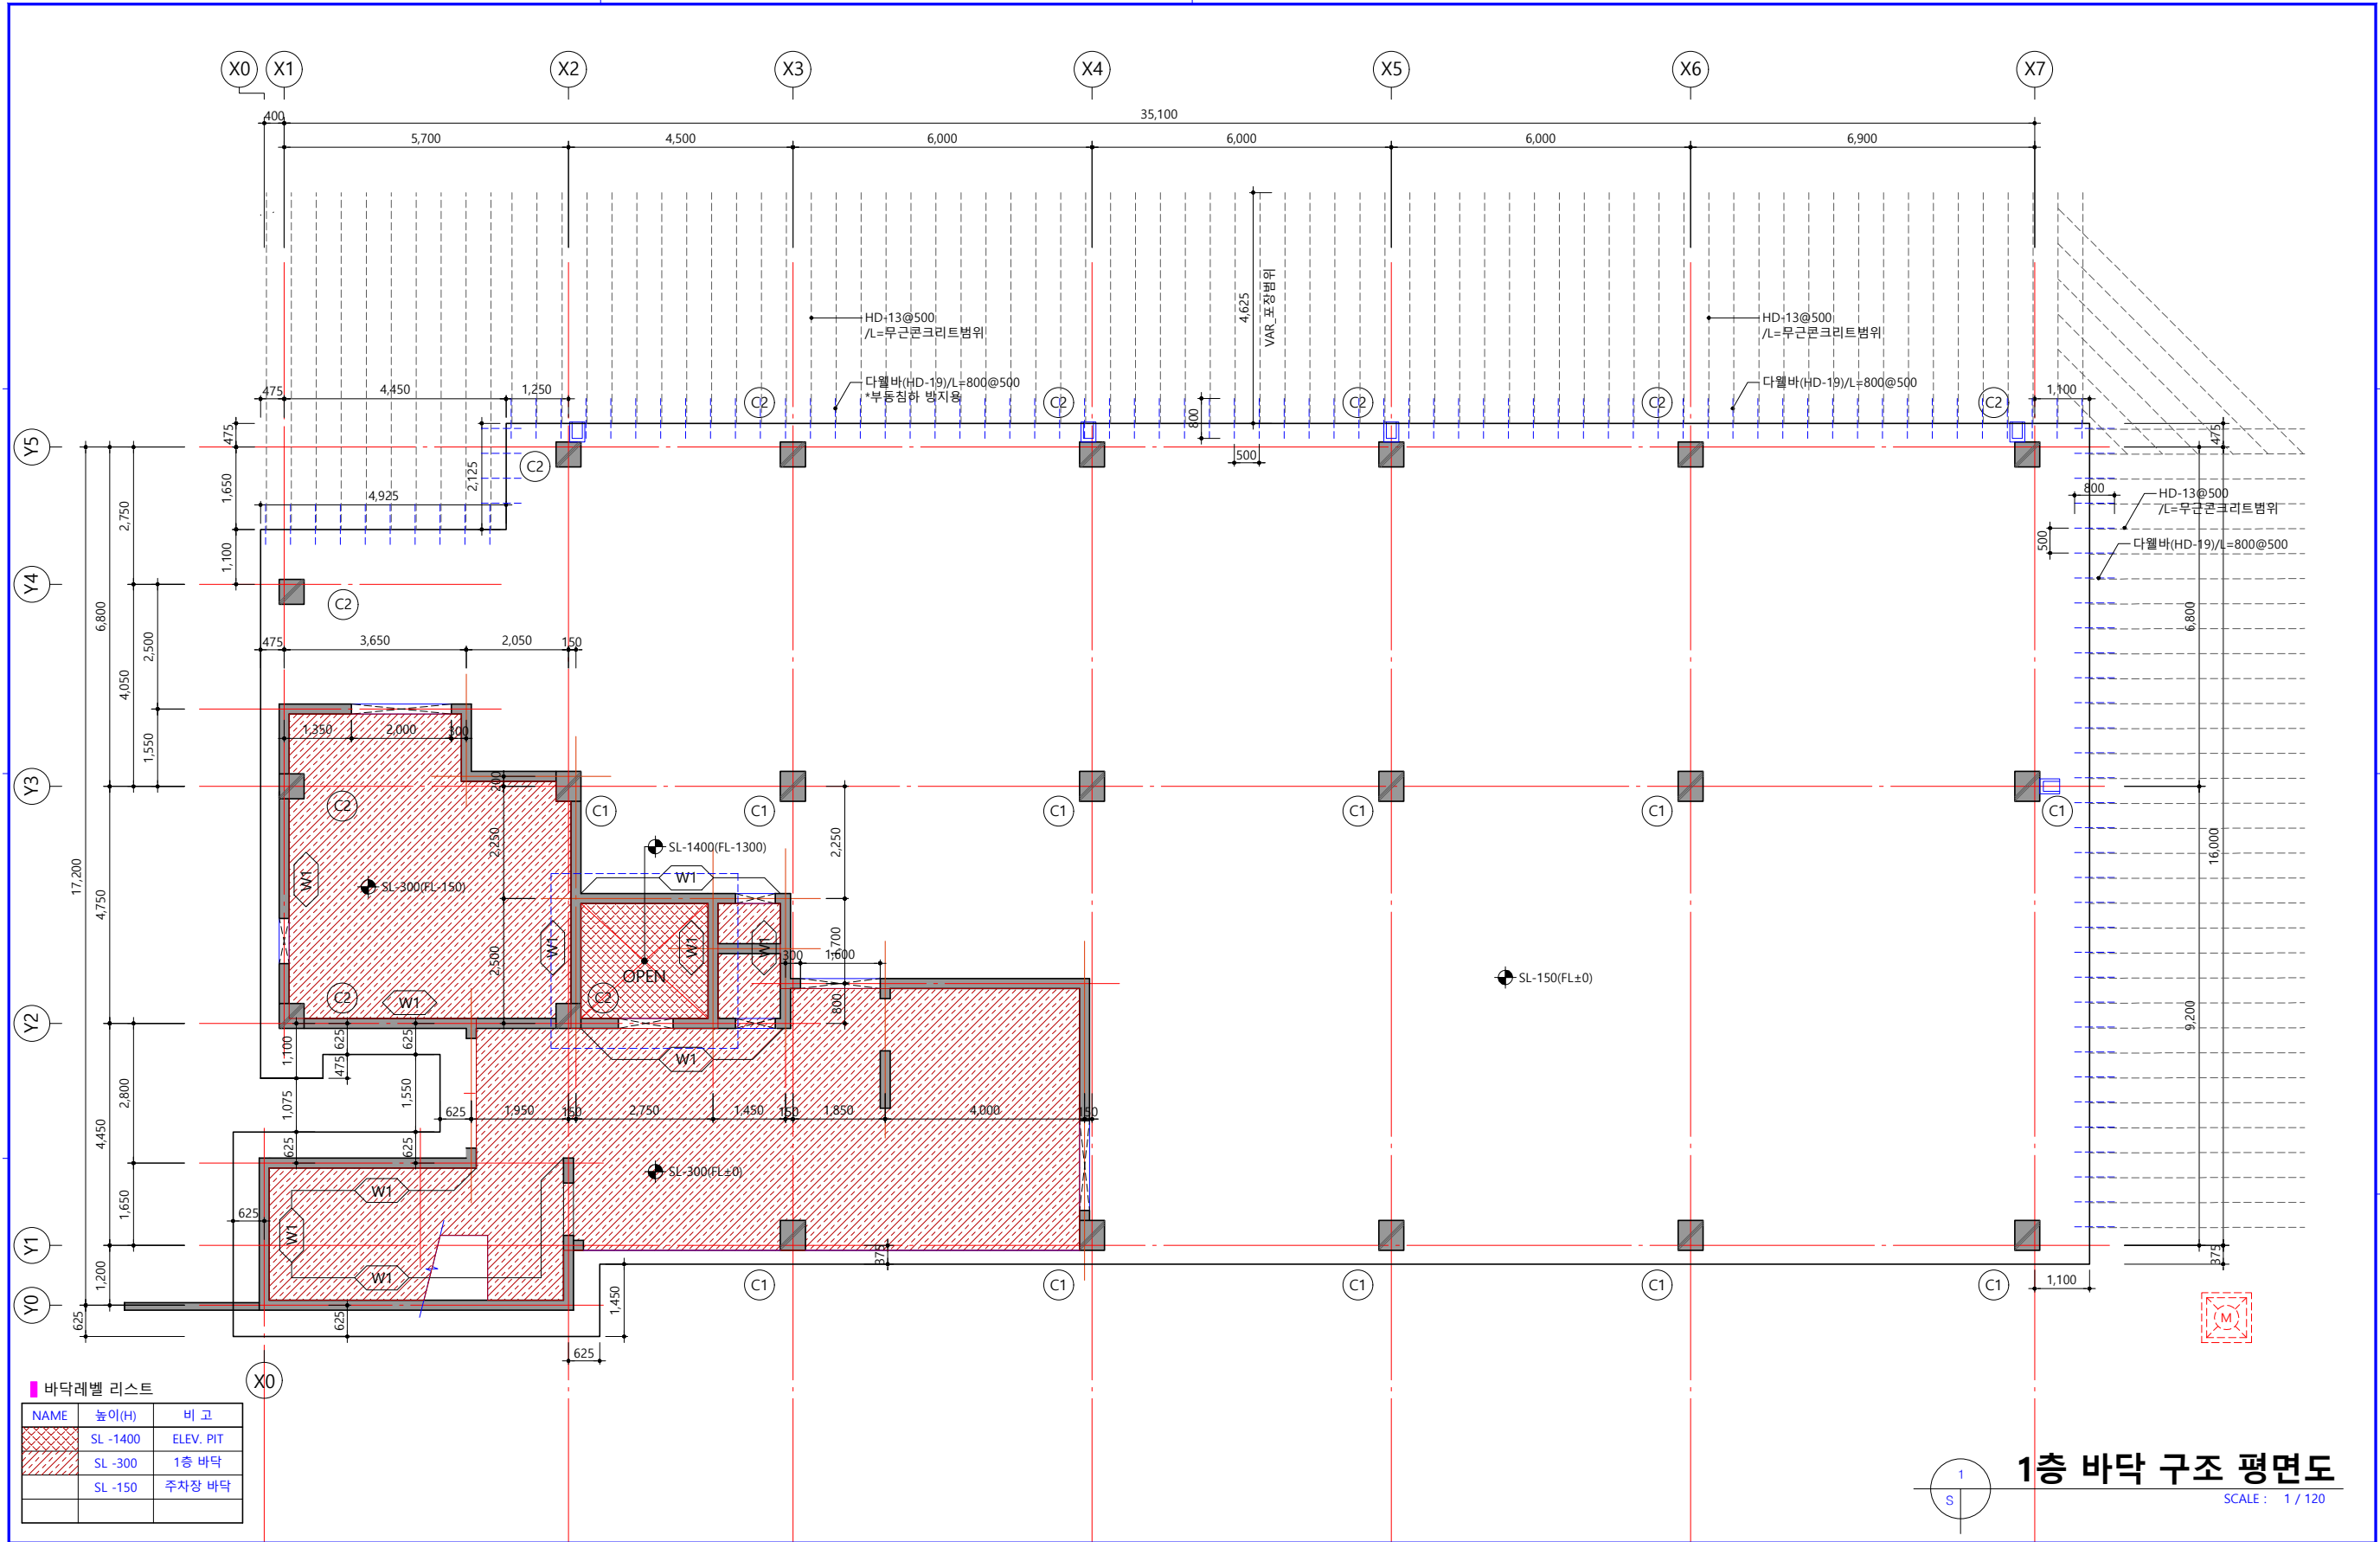

바닥레벨 리스트

NAME	높이(H)	비 고
SL -1400	ELEV. PIT	
SL -300	1층 바닥	
SL -150	주차장 바닥	

1층 바닥 구조 평면도
SCALE : 1 / 120

건축주
CLIENT

NH농협은행
(강원본부)

설계사무소
DESIGN OFFICE

지안21
Tel. 02-6014-2137 / Fax. 02-6014-2138
Email : archjian21@naver.com

NOTE.

1. 콘크리트 : fck = 27MPa / 철근 : fy = 400MPa
2. 미표기 벽체 : W2
3. 외부에 노출되는 콘크리트는 방수처리 할 것

No.	Date	Revision Description	Chkd.

설계명
PROJECT TITLE

NH농협은행
강릉 금융센터 신축공사

설계단계
CONSULTANT

건축구조 : (주)탐앤지니어링
토목 : (주) 제일기초이엔씨
전기/통신/소방 : (주)하랑엔지니어링

프로젝트번호 PROJECT CODE

JP25-0001

설계단계 DESIGN PHASE

실시설계(변경)

승인 APPROVED BY

황진희 00.00.00

검토 CHECKED BY

최용규 00.00.00


작성 Drawn By

신가영 00.00.00

도면명 DRAWING TITLE

1층 바닥 구조 평면도

축척 SCALE	A1: 1/60 A3: 1/120	도면번호 DRAWING NO.	S11-006	발판번호 SHEET NO.	000	REV. No.	
----------	-----------------------	------------------	---------	----------------	-----	----------	--

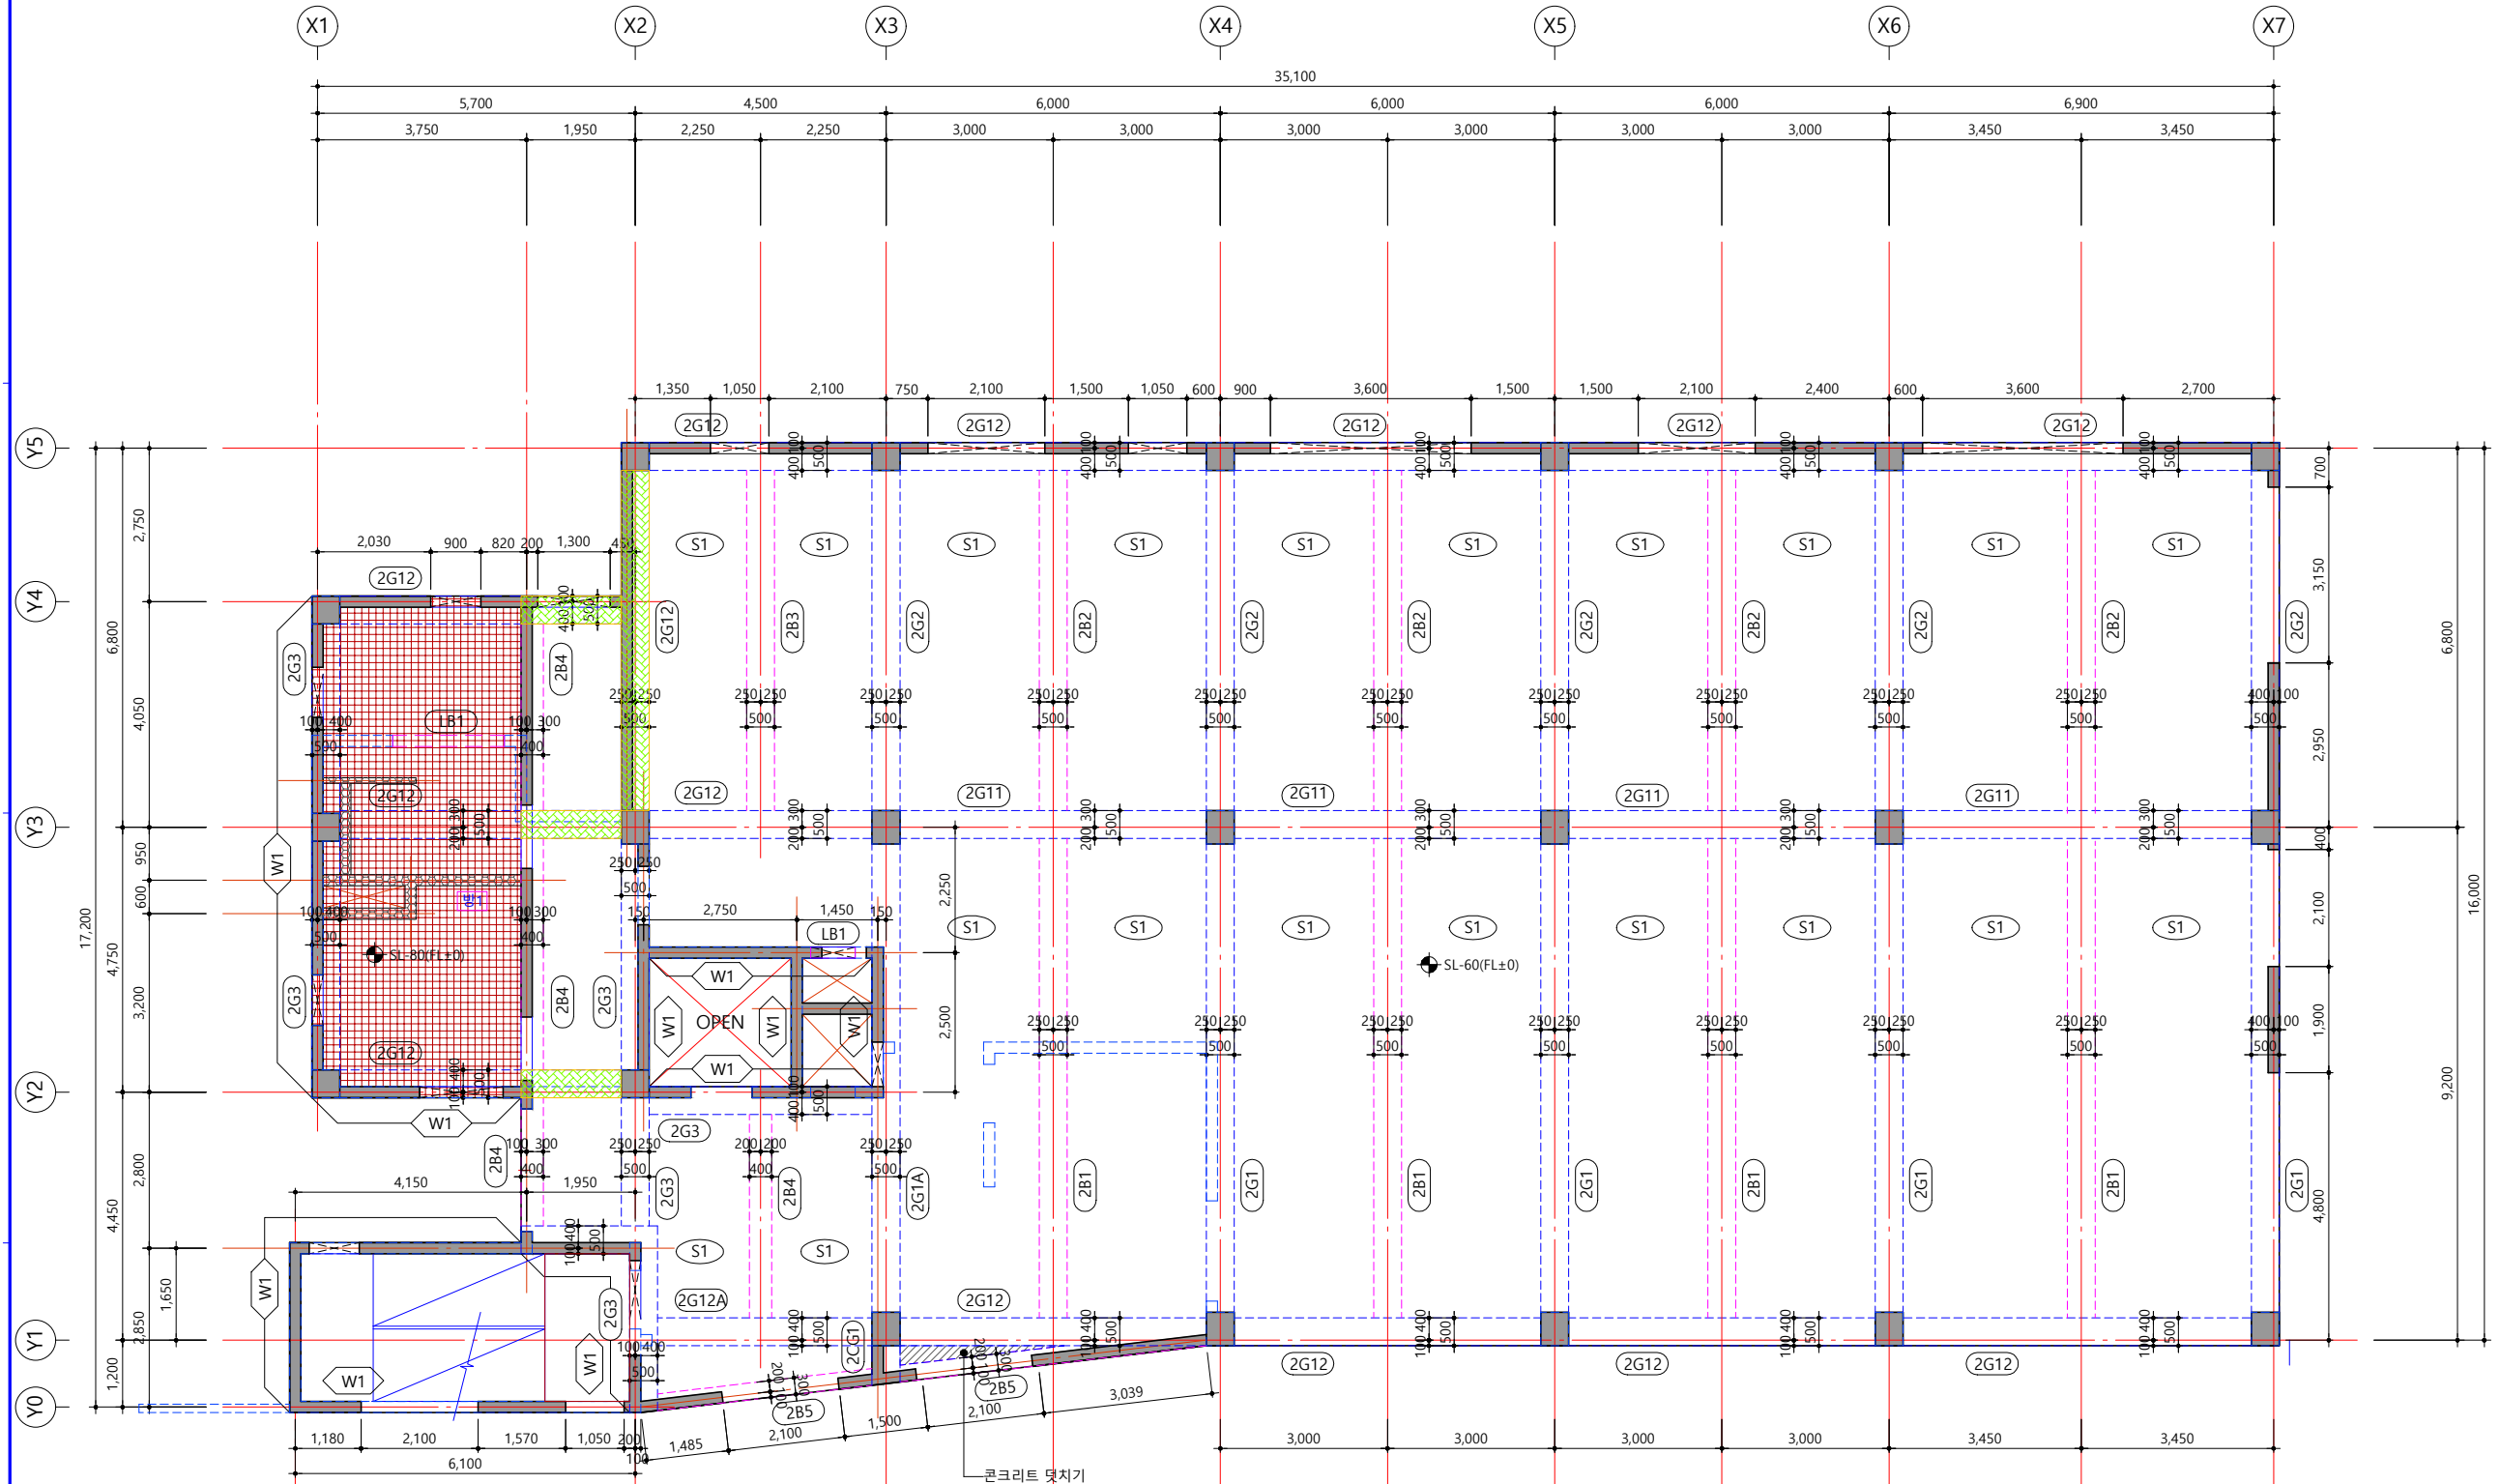

바닥레벨 리스트

NAME	높이(H)	비고
	SL -60	금융점포,계단실
	SL -80	화장실

GIRDER, BEAM LIST

NAME	SIZE(W x H)	비고	NAME	SIZE(W x H)	비고	NAME	SIZE(W x H)	비고	NAME	SIZE(W x H)	비고
2G1	500 x 700		2CG1	500 x 700		2B1	500 x 700		2B5	300 x 700	
2G1A	500 x 700		2G11	500 x 700		2B2	500 x 700				
2G2	500 x 700		2G12	500 x 700		2B3	500 x 700				
2G3	500 x 700		2G12A	500 x 700		2B4	400 x 700				

콘크리트 덧치기

NAME	높이(H)	비고
	20(상부)	복도

방수턱 리스트

NAME	높이(H)	비고
	80	화장실

2층 바닥 구조 평면도
SCALE : 1 / 120

건축주
CLIENT

NH농협은행
(강원본부)

설계사무소
DESIGN OFFICE

지안21
건축사무소
Tel. 02-6014-2137 / Fax. 02-6014-2138
Email : archjian21@naver.com

NOTE.

1. 콘크리트 : fck = 27MPa / 철근 : fy = 400MPa
2. 미표기 벽체 : W2
3. 외부에 노출되는 콘크리트는 방수처리 할 것
4. 미표기 슬라브 : S2

설계명
PROJECT TITLE

NH농협은행
강릉 금융센터 신축공사

설계단계
CONSULTANT

건축구조 : (주)탐앤지니어링
토목 : (주)제일기초이엔씨
전기/통신/소방 : (주)하랑엔지니어링

프로젝트번호 PROJECT CODE

JP25-0001

설계단계 DESIGN PHASE

실시설계(변경)

승인 APPROVED BY

황진희 00.00.00

검토 CHECKED BY

최용규 00.00.00

작성 Drawn By

신가영 00.00.00

도면명 DRAWING TITLE

2층 바닥 구조 평면도

도면번호 DRAWING NO.


S11-007

일련번호 SHEET NO.

000

REV. No.

1

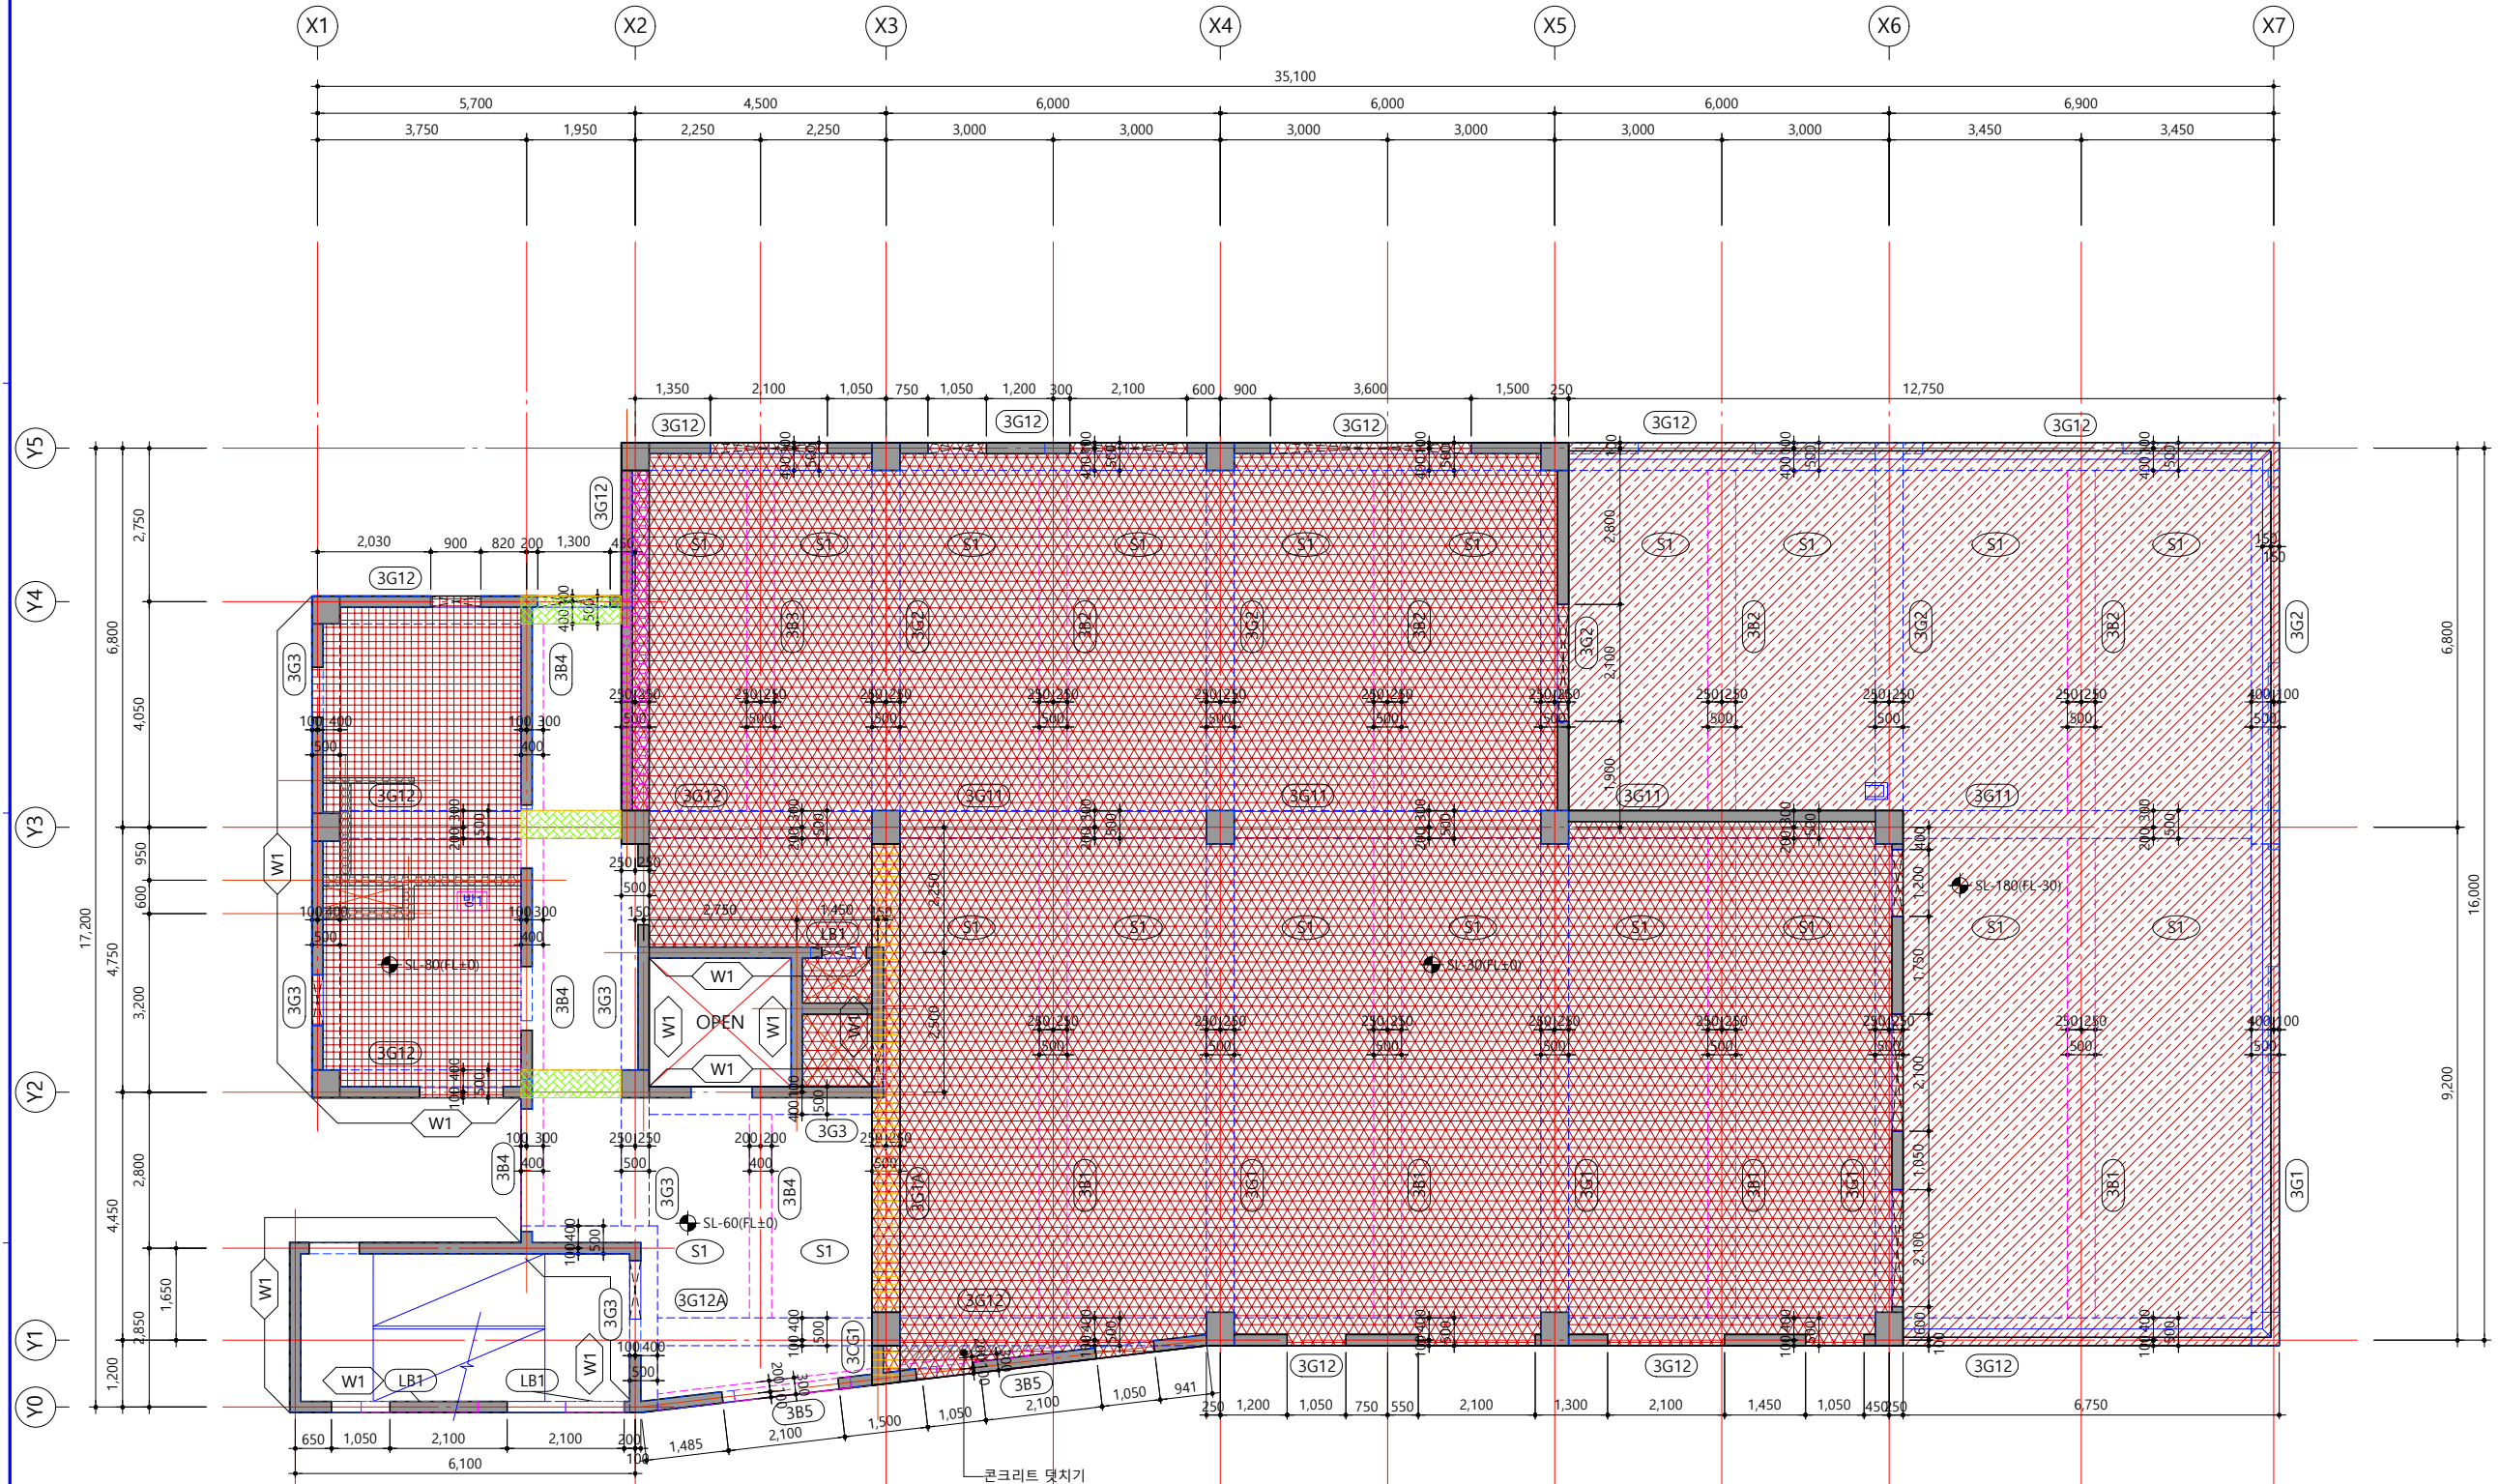

바닥레벨 리스트

NAME	높이(H)	비고
SL -30		금융점포
SL -60		출
SL -80		화장실
SL -180		발코니

GIRDER, BEAM LIST

NAME	SIZE(W x H)	비고	NAME	SIZE(W x H)	비고	NAME	SIZE(W x H)	비고	NAME	SIZE(W x H)	비고
3G1	500 x 700		3CG1	500 x 700		3B1	500 x 700		3B5	300 x 700	
3G1A	500 x 700		3G11	500 x 700		3B2	500 x 700				
3G2	500 x 700		3G12	500 x 700		3B3	500 x 700				
3G3	500 x 700		3G12A	500 x 700		3B4	400 x 700				

콘크리트 덧치기

NAME	높이(H)	비고
30(상부)		복도, 출
20(상부)		복도
50(상부)		복도

방수턱 리스트

NAME	높이(H)	비고
80		화장실

3층 바닥 구조 평면도
SCALE : 1 / 120

건축주
CLIENT

NH농협은행
(강원본부)

설계사무소
DESIGN OFFICE

지안21
Tel. 02-6014-2137 / Fax. 02-6014-2138
Email : archjian21@naver.com

NOTE.

1. 콘크리트 : fck = 27MPa / 철근 : fy = 400MPa
2. 미표기 벽체 : W2
3. 외부에 노출되는 콘크리트는 방수처리 할 것
4. 미표기 슬라브 : S2

설계명
PROJECT TITLE

NH농협은행
강릉 금융센터 신축공사

설계단계
CONSULTANT

건축구조 : (주)탐앤지니어링
토목 : (주)제일기조엔씨
전기/통신/소방 : (주)하랑엔지니어링

프로젝트번호
PROJECT CODE

JP25-0001

승인
APPROVED BY

황진희 00.00.00

검토
CHECKED BY

최용규 00.00.00

작성
Drawn By

신가영 00.00.00

실시설계(변경)

도면명
DRAWING TITLE

3층 바닥 구조 평면도

도면번호
DRAWING NO.

S11-008

출력
SCALE


A1: 1/60
A3: 1/120

도면번호
SHEET NO.

000

REV. No.

△

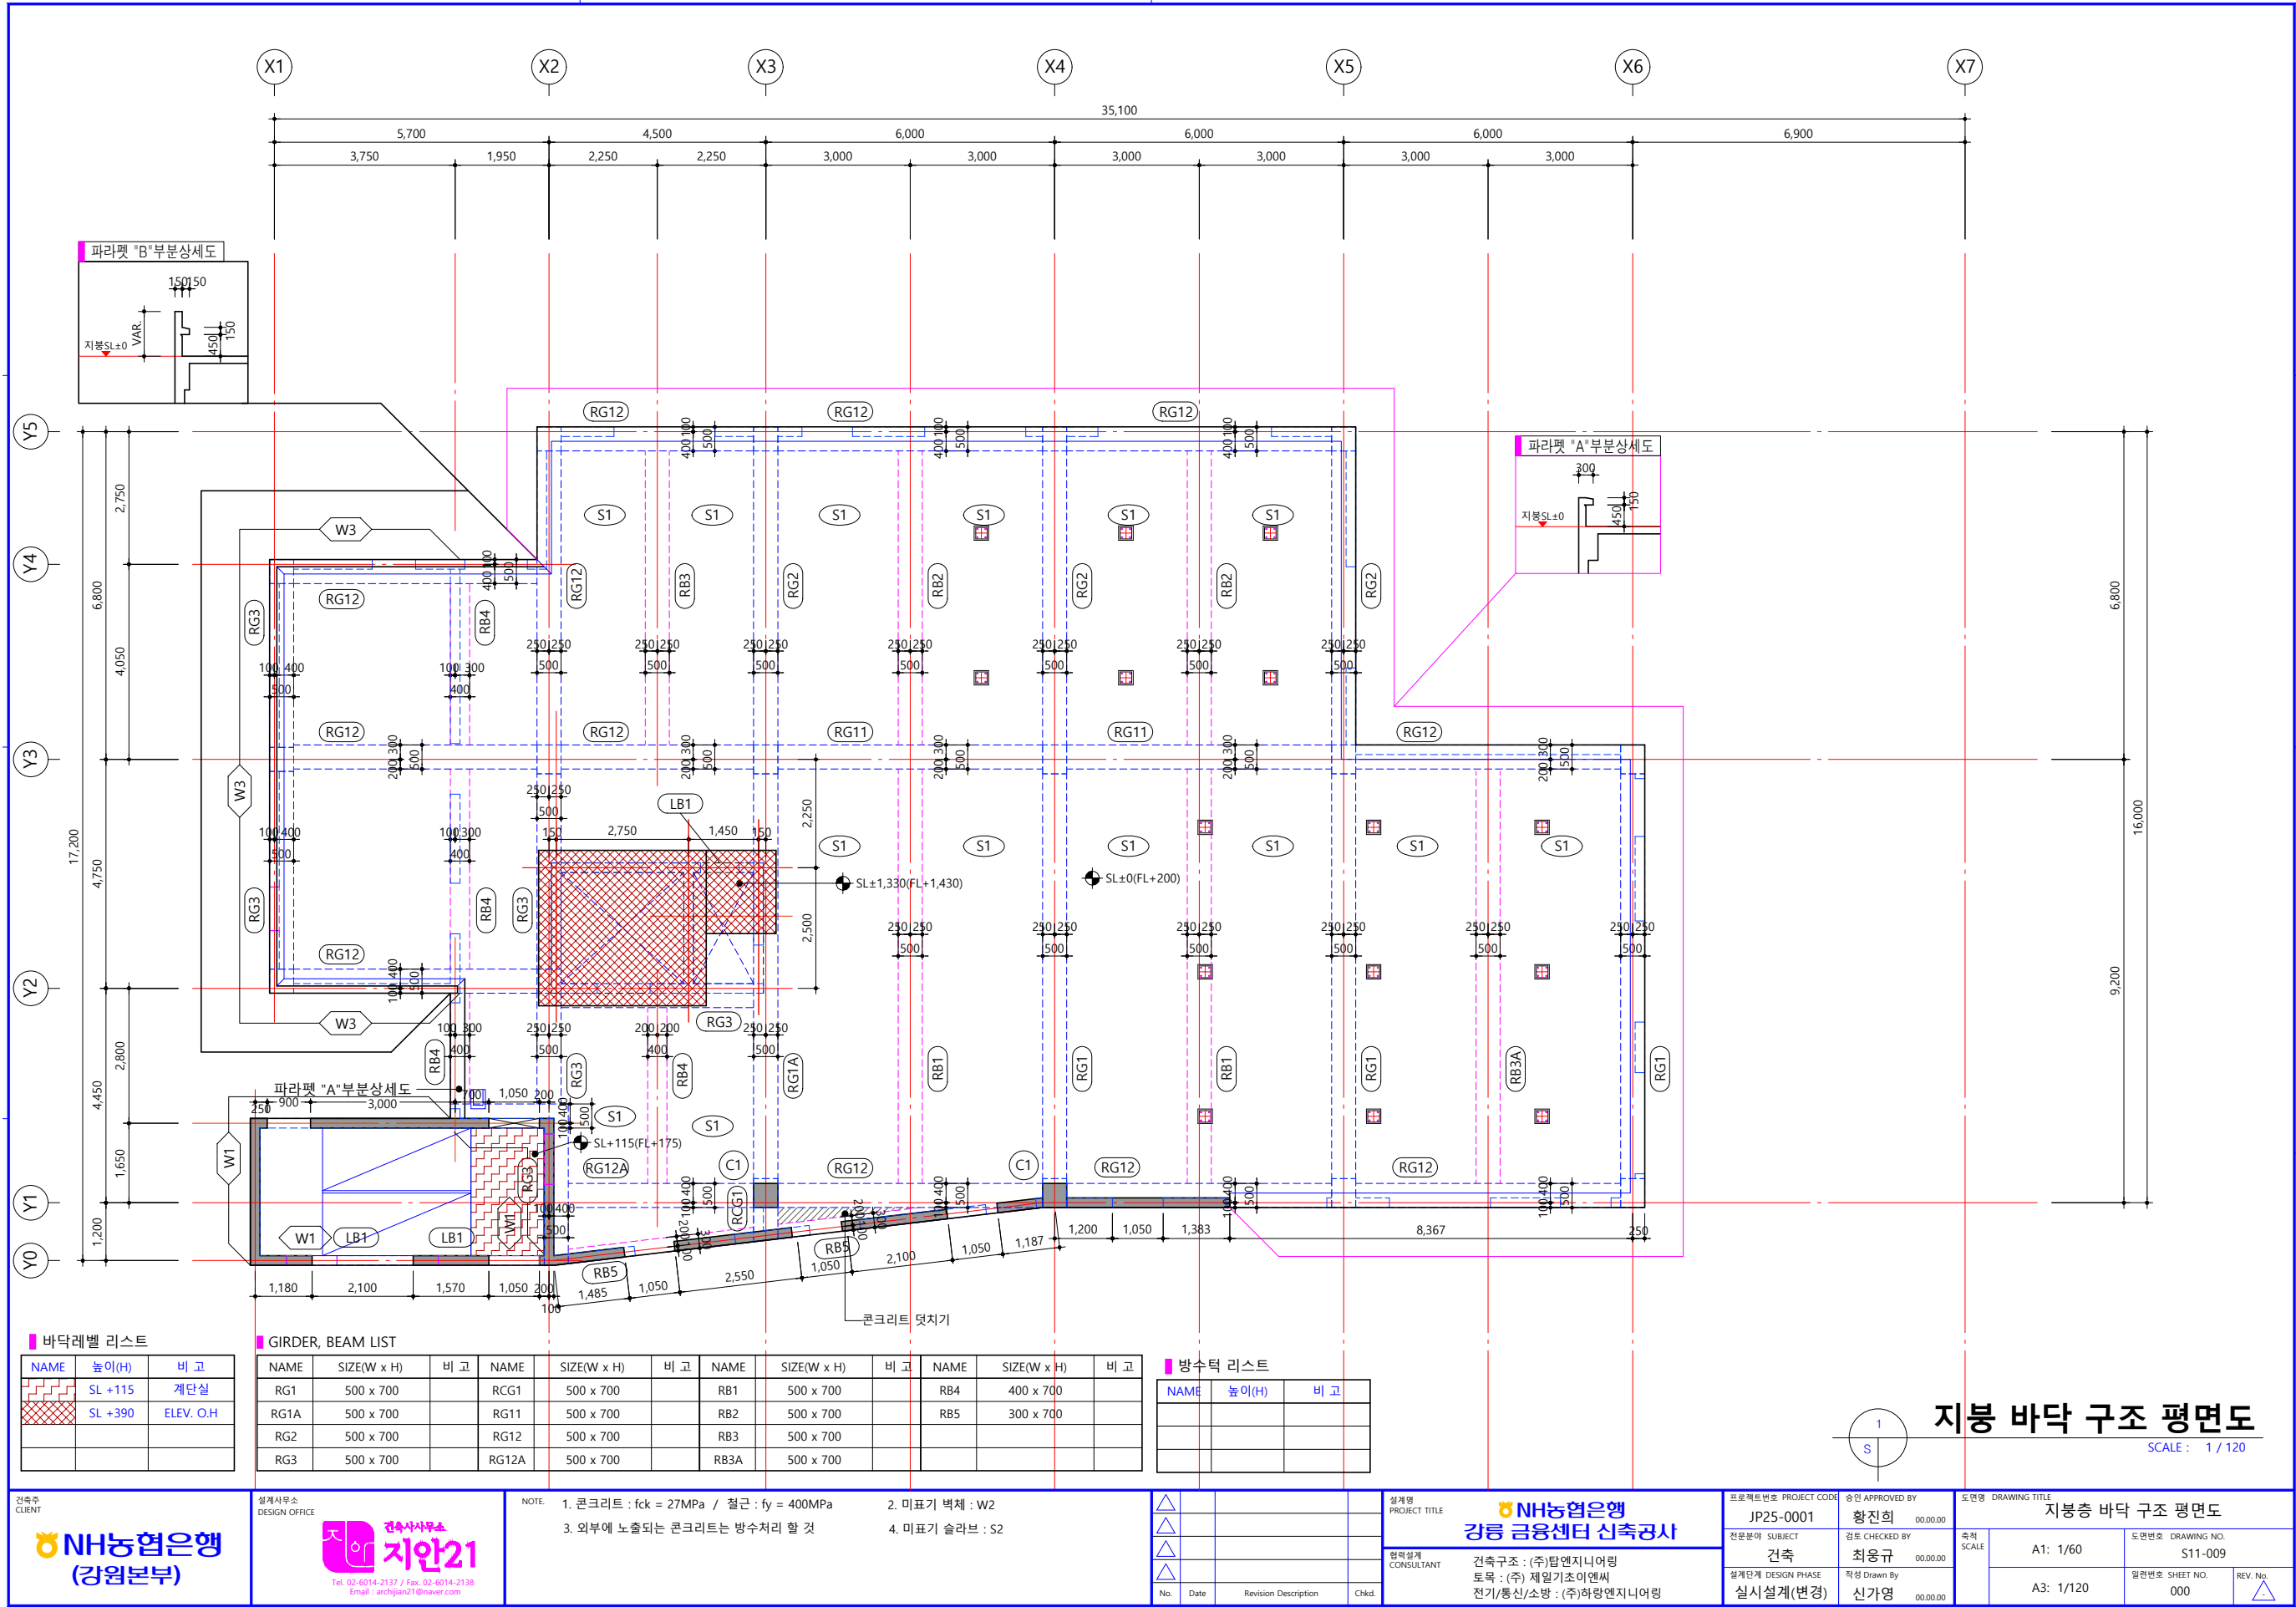

바닥레벨 리스트

NAME	높이(H)	비 고
	SL +115	계단실
	SL +390	ELEV. O.H

GIRDER, BEAM LIST

NAME	SIZE(W x H)	비 고	NAME	SIZE(W x H)	비 고	NAME	SIZE(W x H)	비 고	NAME	SIZE(W x H)	비 고
RG1	500 x 700		RCG1	500 x 700		RB1	500 x 700		RB4	400 x 700	
RG1A	500 x 700		RG11	500 x 700		RB2	500 x 700		RB5	300 x 700	
RG2	500 x 700		RG12	500 x 700		RB3	500 x 700				
RG3	500 x 700		RG12A	500 x 700		RB3A	500 x 700				

방수턱 리스트

NAME	높이(H)	비 고

지붕 바닥 구조 평면도
SCALE : 1 / 120

건축주
CLIENT

설계사무소
DESIGN OFFICE

Tel. 02-6014-2137 / Fax. 02-6014-2138
Email : archjian21@naver.com

NOTE.

1. 콘크리트 : fck = 27MPa / 철근 : fy = 400MPa

2. 미표기 벽체 : W2

3. 외부에 노출되는 콘크리트는 방수처리 할 것

4. 미표기 슬라브 : S2

△

△

△

△

No.

Date

Revision Description

Chkd.

설계명
PROJECT TITLE

영역 설계
CONSULTANT

건축구조 : (주)탐앤지니어링
토목 : (주) 제일기조이엔씨
전기/통신/소방 : (주)하랑엔지니어링

프로젝트번호 PROJECT CODE

JP25-0001

승인 APPROVED BY

황진희 00.00.00

전문분야 SUBJECT

건축

검토 CHECKED BY

최용규 00.00.00

설계단계 DESIGN PHASE

실시 설계(변경)

작성 Drawn By

신가영 00.00.00

도면명 DRAWING TITLE

지붕층 바닥 구조 평면도

도면번호 DRAWING NO.

S11-009

축척 SCALE


A1: 1/60
A3: 1/120

도면번호 SHEET NO.

000

REV. No.

△

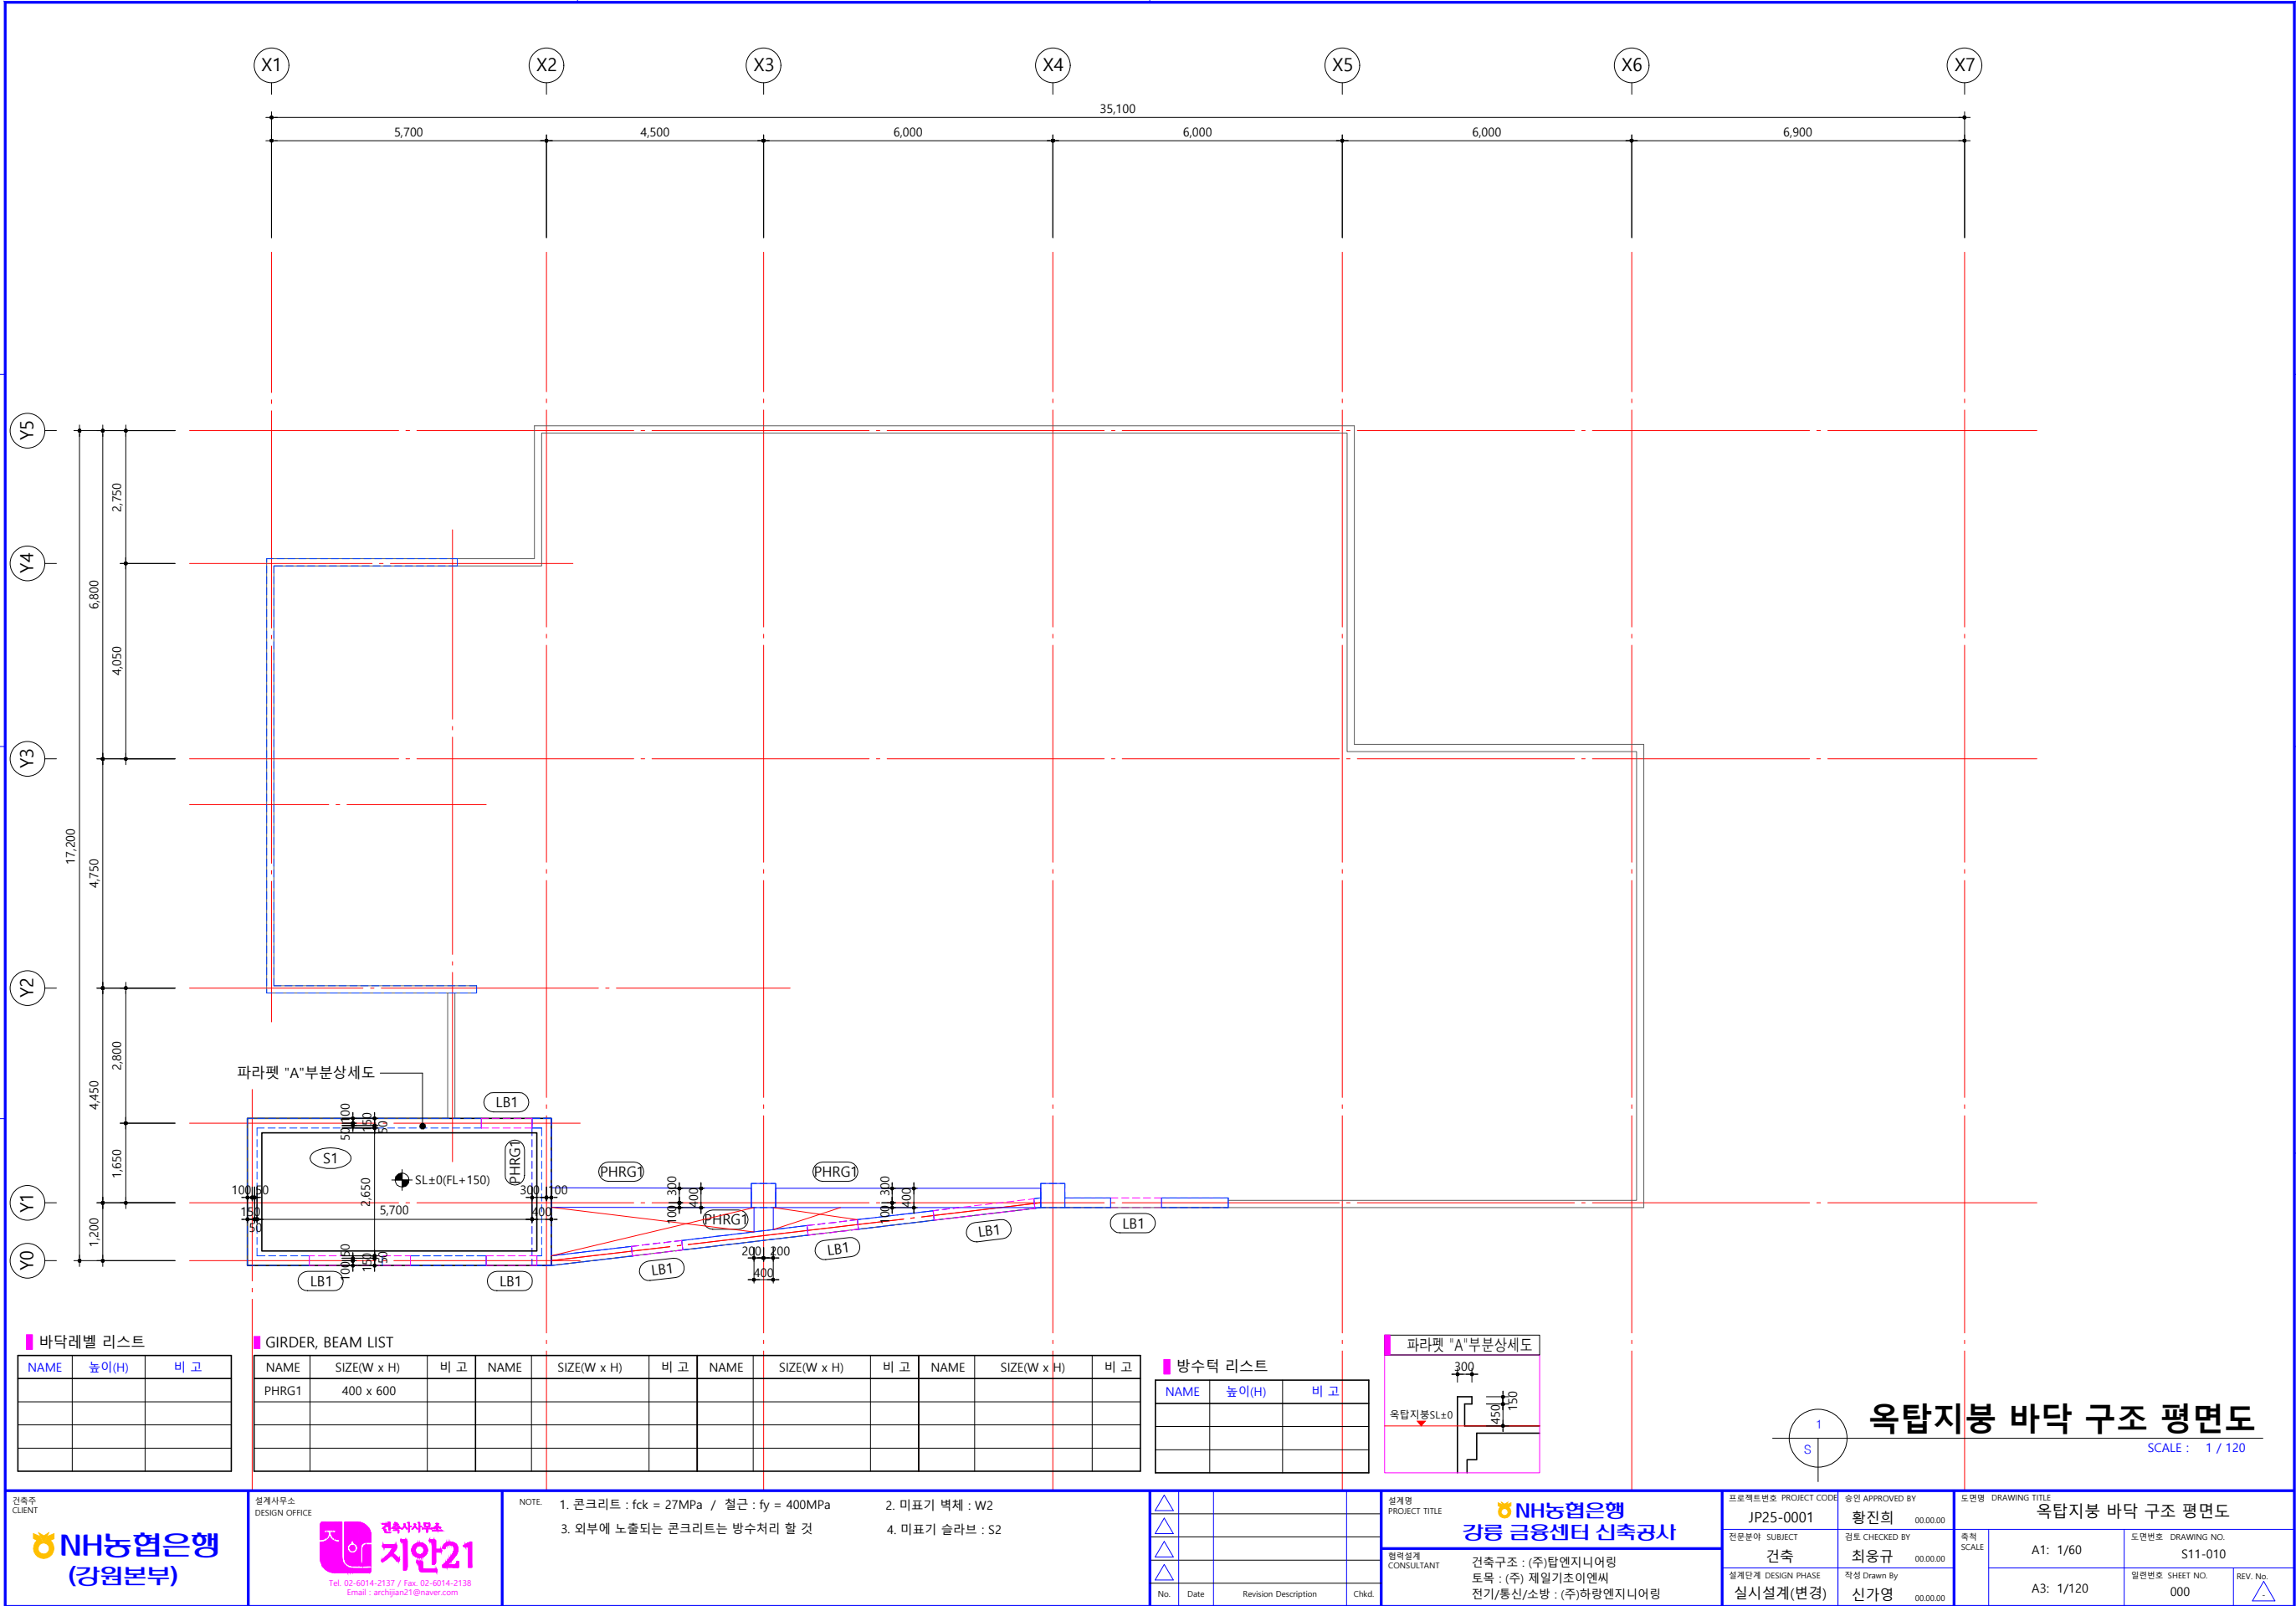

바닥레벨 리스트		
NAME	높이(H)	비고

GIRDER, BEAM LIST											
NAME	SIZE(W x H)	비고	NAME	SIZE(W x H)	비고	NAME	SIZE(W x H)	비고	NAME	SIZE(W x H)	비고
PHRG1	400 x 600										

방수터 리스트		
NAME	높이(H)	비고



건축주
CLIENT

설계사무소
DESIGN OFFICE

Tel. 02-6014-2137 / Fax. 02-6014-2138
Email : archjian21@naver.com

NOTE.

1. 콘크리트 : fck = 27MPa / 철근 : fy = 400MPa

2. 미표기 벽체 : W2

3. 외부에 노출되는 콘크리트는 방수처리 할 것

4. 미표기 슬라브 : S2

No.	Date	Revision Description	Chkd.

설계명
PROJECT TITLE

설계단계
CONSULTANT

건축구조 : (주)탐앤지니어링
토목 : (주)제일기초이엔씨
전기/통신/소방 : (주)하랑엔지니어링

프로젝트번호 PROJECT CODE	승인 APPROVED BY
JP25-0001	황진희 00.00.00
전문분야 SUBJECT	검토 CHECKED BY
건축	최용규 00.00.00
설계단계 DESIGN PHASE	작성 Drawn By
실시설계(변경)	신가영 00.00.00

도면명 DRAWING TITLE			
옥탑지붕 바닥 구조 평면도			
도면번호 DRAWING NO.	축척 SCALE	도면번호 DRAWING NO.	도면번호 DRAWING NO.
A1: 1/60	A1: 1/60	S11-010	S11-010
도면번호 DRAWING NO.	도면번호 DRAWING NO.	도면번호 DRAWING NO.	도면번호 DRAWING NO.
000	000	000	000