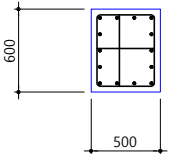
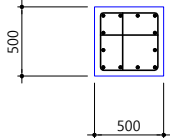
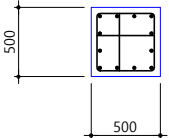
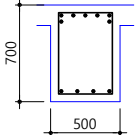
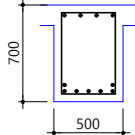
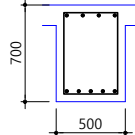
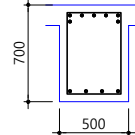
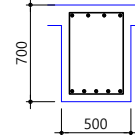
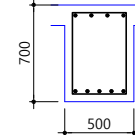
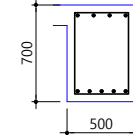
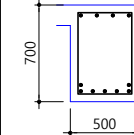
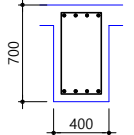
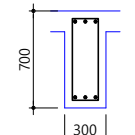
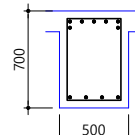
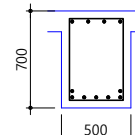
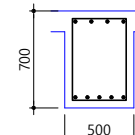
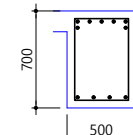
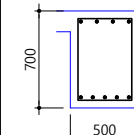
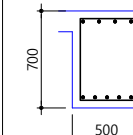
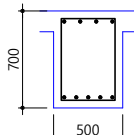
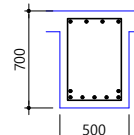
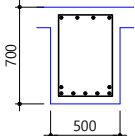
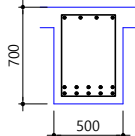
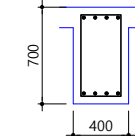
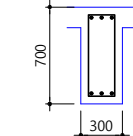
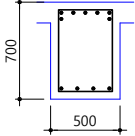
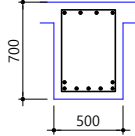
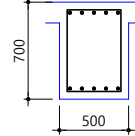
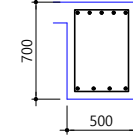
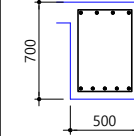
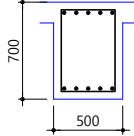
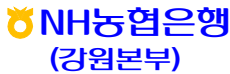
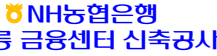


기둥 일람표

기 호	1~3 C1	R C1				
형 상						
크 기	500 X 600	500 X 500				
주근	14 - D22	12 - D22				
후프(END)	D10@150	D10@150				
후프(CEN)	D10@300	D10@300				
기 호	C2					
형 상						
크 기	500 X 500					
상부근	12 - D22					
하부근	D10@150					
스티럽	D10@300					
기 호						
형 상						
크 기						
상부근						
하부근						
스티럽						
기 호						
형 상						
크 기						
상부근						
하부근						
스티럽						

■ 보 일람표

기 호	2~3 B1			2~3 B2			2~3 B3			2~3 B4		
형 상	<CONT> 	<CENTER> 	<DISCONT> 	<CONT> 	<CENTER> 	<DISCONT> 	<END> 	<CENTER> 		<ALL> 		
크 기	500 X 700	500 X 700	500 X 700	500 X 700	500 X 700	500 X 700	500 X 700	500 X 700		400 X 700		
상부근	7 - D22	4 - D22	4 - D22	7 - D22	4 - D22	4 - D22	4 - D22	4 - D22		4 - D22		
하부근	4 - D22	7 - D22	5 - D22	4 - D22	5 - D22	5 - D22	5 - D22	7 - D22		4 - D22		
스터럽	2 - D10 @ 200	2 - D10 @ 300	2 - D10 @ 200	2 - D10 @ 200	2 - D10 @ 300	2 - D10 @ 200	2 - D10 @ 200	2 - D10 @ 300		2 - D10 @ 200		
기 호	2~3 B5			R B1			R B2			R B3		
형 상	<ALL> 			<CONT> 	<CENTER> 	<DISCONT> 	<CONT> 	<CENTER> 	<DISCONT> 	<END> 	<CENTER> 	
크 기	300 X 700			500 X 700	500 X 700	500 X 700	500 X 700	500 X 700	500 X 700	500 X 700	500 X 700	
상부근	3 - D22			7 - D22	4 - D22	4 - D22	7 - D22	4 - D22	4 - D22	4 - D22	4 - D22	
하부근	3 - D22			4 - D22	7 - D22	5 - D22	4 - D22	5 - D22	5 - D22	5 - D22	7 - D22	
스터럽	2 - D10 @ 200			2 - D10 @ 200	2 - D10 @ 300	2 - D10 @ 200	2 - D10 @ 200	2 - D10 @ 300	2 - D10 @ 200	2 - D10 @ 200	2 - D10 @ 300	
기 호	R B3A			R B4			R B5					
형 상	<END> 	<CENTER> 		<ALL> 			<ALL> 					
크 기	500 X 700	500 X 700		400 X 700			300 X 700					
상부근	4 - D22	4 - D22		4 - D22			3 - D22					
하부근	7 - D22	10 - D22		4 - D22			3 - D22					
스터럽	2 - D10 @ 200	2 - D10 @ 300		2 - D10 @ 200			2 - D10 @ 200					
기 호	2~3 G1			2~3 G1A			2~3 G2			2~3 G3		
형 상	<END> 	<CENTER> 		<ALL> 			<END> 	<CENTER> 		<ALL> 		
크 기	500 X 700	500 X 700		500 X 700			500 X 700	500 X 700		500 X 700		
상부근	7 - D22	4 - D22		5 - D22			5 - D22	4 - D22		5 - D22		
하부근	4 - D22	7 - D22		5 - D22			4 - D22	5 - D22		5 - D22		
스터럽	2 - D10 @ 150	2 - D10 @ 250		2 - D10 @ 150			2 - D10 @ 150	2 - D10 @ 250		2 - D10 @ 150		


건축주 CLIENT 	설계사무소 DESIGN OFFICE  Tel. 02-6014-2137 / Fax. 02-6014-2138 Email : archjian21@naver.com	NOTE.	No. Date Revision Description Chkd.	설계명 PROJECT TITLE  설계단계 CONSULTANT 건축구조 : (주)탐엔지니어링 토목 : (주) 제일기초이엔씨 전기/통신/소방 : (주)하랑엔지니어링	프로젝트번호 PROJECT CODE JP25-0001	승인 APPROVED BY 황진희 00.00.00	도면명 DRAWING TITLE 보 일람표-1	
					전문분야 SUBJECT 건축	검토 CHECKED BY 최용규 00.00.00	축척 SCALE A1: 1/25	도면번호 DRAWING NO. S21-002
					설계단계 DESIGN PHASE 실시설계(변경)	작성 Drawn By 신가영 00.00.00	A3: 1/50	일련번호 SHEET NO. 000 REV. No. 

■ 보 일람표

기 호	2~3 CG1			2~3 G11			2~3 G12			2~3 G12A		
형 상												
크 기	500 X 700			500 X 700	500 X 700		500 X 700	500 X 700		500 X 700		
상부근	7 - D22			9 - D22	4 - D22		7 - D22	4 - D22		5 - D22		
하부근	4 - D22			4 - D22	9 - D22		4 - D22	7 - D22		5 - D22		
스터럽	2 - D10 @ 150			2 - D13 @ 150	2 - D13 @ 150		2 - D13 @ 150	2 - D13 @ 150		2 - D13 @ 150		
기 호	R G1			R G1A			R G2			R G3		
형 상												
크 기	500 X 700	500 X 700		500 X 700			500 X 700	500 X 700		500 X 700		
상부근	7 - D22	4 - D22		5 - D22			5 - D22	4 - D22		5 - D22		
하부근	4 - D22	7 - D22		5 - D22			4 - D22	5 - D22		5 - D22		
스터럽	2 - D10 @ 150	2 - D10 @ 250		2 - D10 @ 150			2 - D10 @ 150	2 - D10 @ 250		2 - D10 @ 150		
기 호	R CG1			R G11			R G12			R G12A		
형 상												
크 기	500 X 700			500 X 700	500 X 700		500 X 700	500 X 700		500 X 700		
상부근	7 - D22			9 - D22	4 - D22		7 - D22	4 - D22		5 - D22		
하부근	4 - D22			4 - D22	9 - D22		4 - D22	7 - D22		5 - D22		
스터럽	2 - D10 @ 150			2 - D13 @ 150	2 - D13 @ 150		2 - D13 @ 150	2 - D13 @ 150		2 - D13 @ 150		
기 호	PH.R G1											
형 상												
크 기	400 X 600											
상부근	4 - D22											
하부근	4 - D22											
스터럽	2 - D10 @ 200											


건축주 CLIENT 	설계사무소 DESIGN OFFICE Tel. 02-6014-2137 / Fax. 02-6014-2138 Email : archjian21@naver.com	NOTE.				No.	Date	Revision Description	Chkd.	설계명 PROJECT TITLE 	프로젝트번호 PROJECT CODE JP25-0001	승인 APPROVED BY 황진희 00.00.00	도면명 DRAWING TITLE 보 일람표-2	
										영역설계 CONSULTANT 건축구조 : (주)탐엔지니어링 토목 : (주) 제일기초이엔씨 전기/통신/소방 : (주)하랑엔지니어링	전문분야 SUBJECT 건축	검토 CHECKED BY 최용규 00.00.00	축척 SCALE A1: 1/25	도면번호 DRAWING NO. S21-003
											설계단계 DESIGN PHASE 실시설계(변경)	작성 Drawn By 신가영 00.00.00	밀원번호 SHEET NO. 000	REV. No.

■ 슬래브 일람표

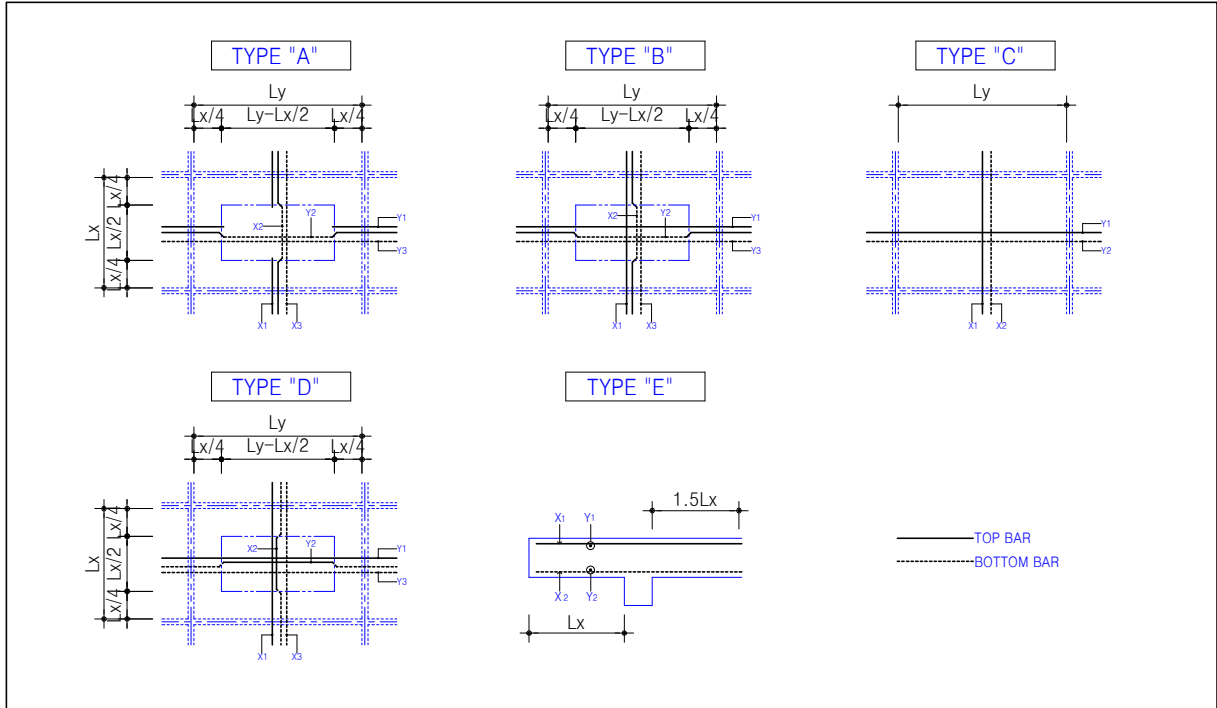


NAME	TYPE	THK.	SHORT DIRECTION (X)					LONG DIRECTION (Y)				
			X1	X2	X3	X4	X5	Y1	Y2	Y3	Y4	Y5
PH.R S1	C	150	D10 @250	D10 @250	-	-	-	D10 @250	D10 @250	-	-	-
2~R S1	C	150	D10 @200	D10 @200	-	-	-	D10 @300	D10 @300	-	-	-
2~R S2	C	150	D10 @200	D10 @200	-	-	-	D10 @200	D10 @200	-	-	-


■ SS1 계단 배근도

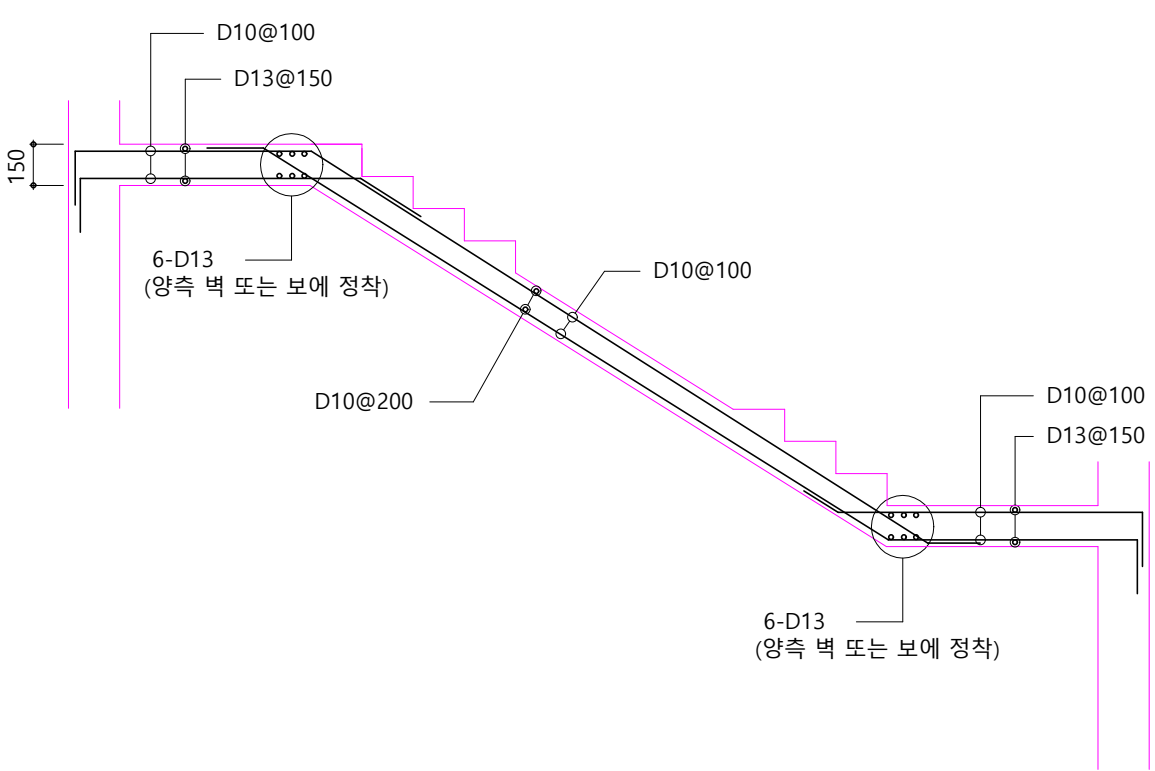


■ 벽체 일람표

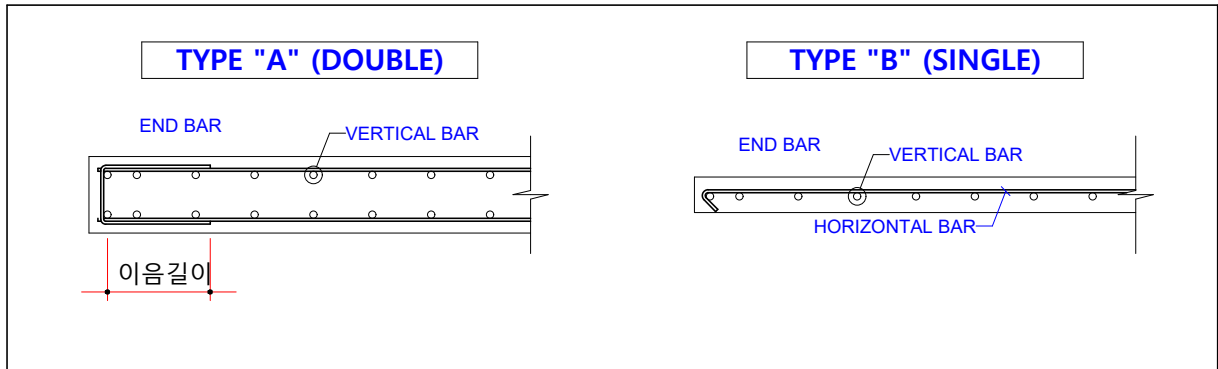


NAME	TYPE	THK.	VER. BAR	HOR. BAR	END BAR	REMARKS
W1	A	200	D10@200	D10@200	2-D13	2F~TOP
		200	D13@200	D10@200	2-D13	1F
W2	A	200	D10@250	D10@250	2-D13	ALL
W3	A	150	D10@200	D10@200	2-D13	지붕층

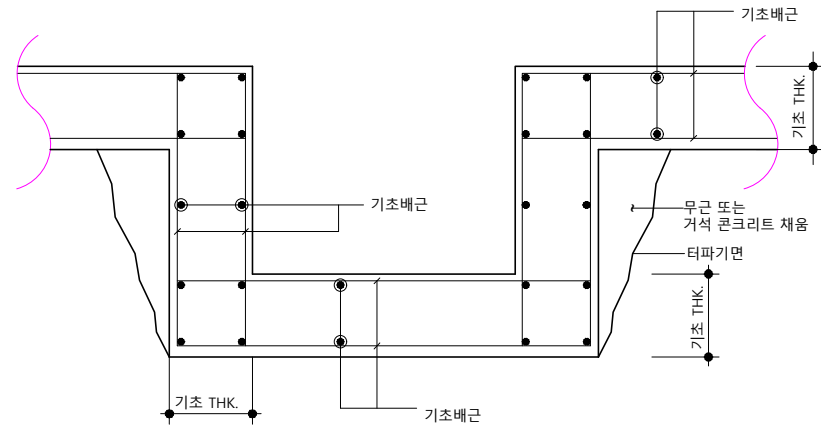


3 | ELEV. PIT 기초 단차부 배근 상세

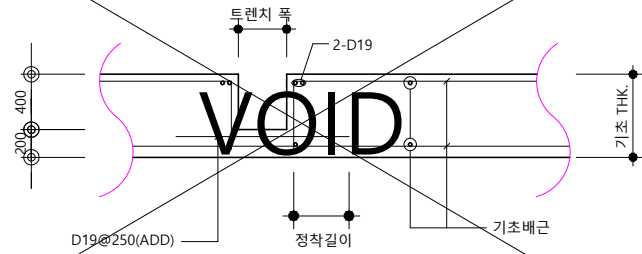


6 외부계단 트렌치 상세

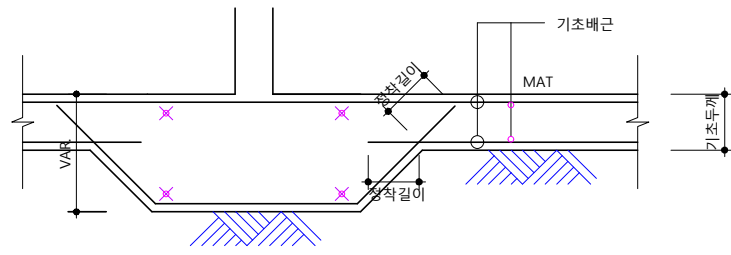

기초 하부보강 단면 상세

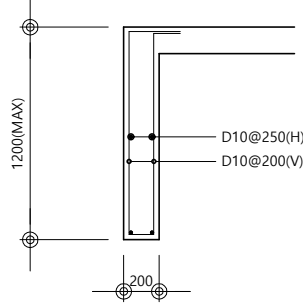

수벽 배근상세 (Thk. 200)

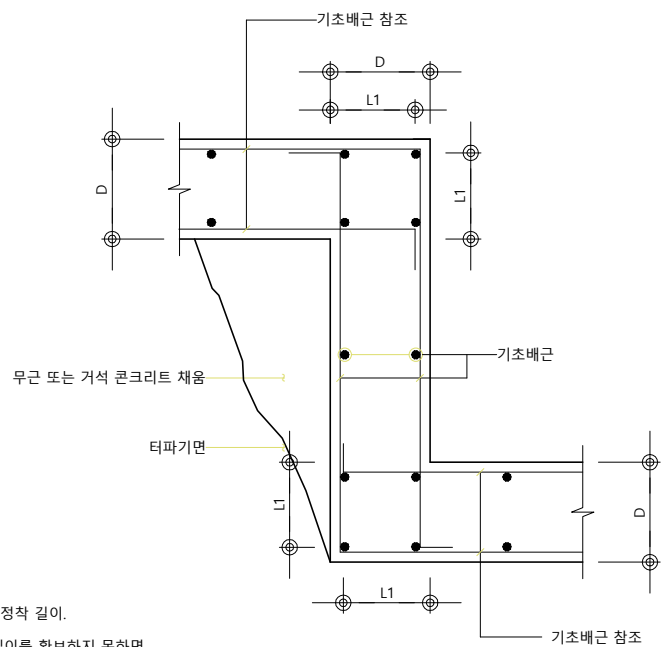

1. L1은 인장 철근 정착 길이.
2. 인장철근 정착길이를 확보하지 못하면 90° 표준 갈고리를 사용.
3. D : 기초두께

13 기초 단차 배근 상세

설계사무소
DESIGN OFFICE

NH농협은행
(강원본부)

건축사무소
ARCHITECT

지안21
Tel. 02-6014-2137 / Fax. 02-6014-2138
Email : archjian21@naver.com

NOTE.


△			
△			
△			
No.	Date	Revision Description	Chkd.

설계명 PROJECT TITLE	프로젝트번호 PROJECT CODE	승인 APPROVED BY	도면명 DRAWING TITLE
NH농협은행 강릉 금융센터 신축공사	JP25-0001	황진희 00.00.00	잡배근상세도
	발령업체 CONSULTANT	원도 CHECKED BY	축척 SCALE
	건축구조 : (주)탐앤타지니어링 도목 : (주) 제일기조이엔씨 전기/통신/소방 : (주)하랑엔지니어링	건축 최용규 00.00.00	A1: NONE 도면번호 DRAWING NO. S21-005
설계단계 DESIGN PHASE	작성 Drawn By	도면번호 SHEET NO.	REV. No.
실시설계(변경)	신가영 00.00.00	A3: NONE 000	△


■ 중간모멘트골조 내진배근상세

1) 기둥배근-내진 설계시 중간 모멘트 골조

(1) 외부 기둥 (띠철근 배근시 전구간 135도 갈고리를 적용할 것)

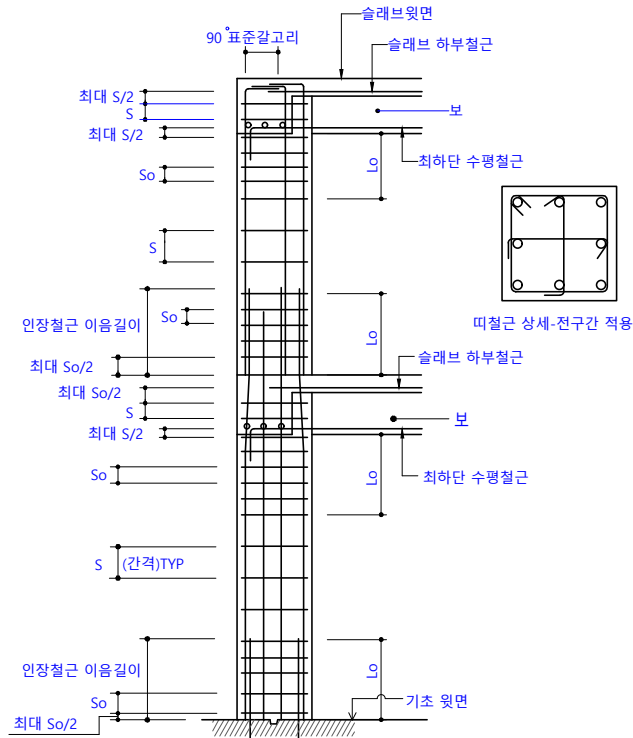


(2) 내부 기둥 (띠철근 배근시 전구간 135도 갈고리를 적용할 것)

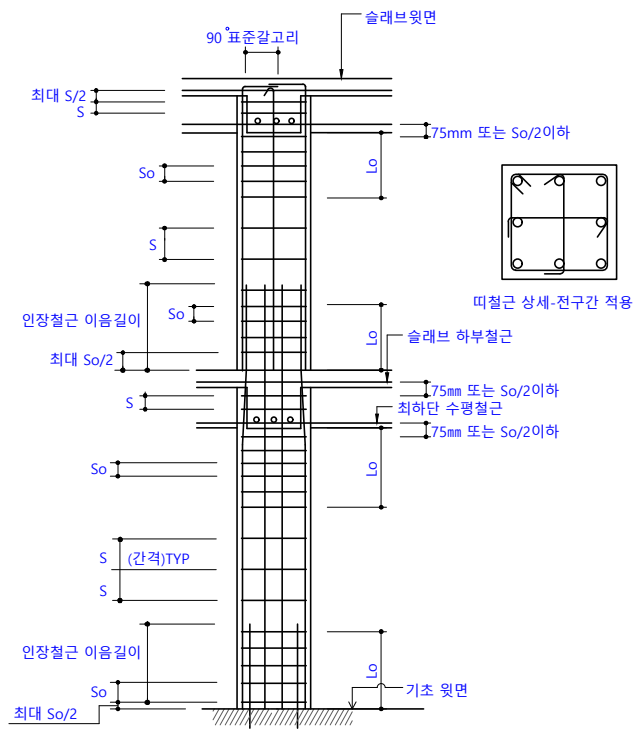


주 기 : Lo 구간은 부재 순높이의 1/6, 부재 단면의 최대 치수, 450mm이하 중 큰값 이상으로 함.
So : 8db(주근), 24d (띠철근), 1/2h (골조부재단면치수), 300mm이하 중 작은 값

2) 보 배근-내진설계시 중간모멘트 골조

(1) 보의 주철근

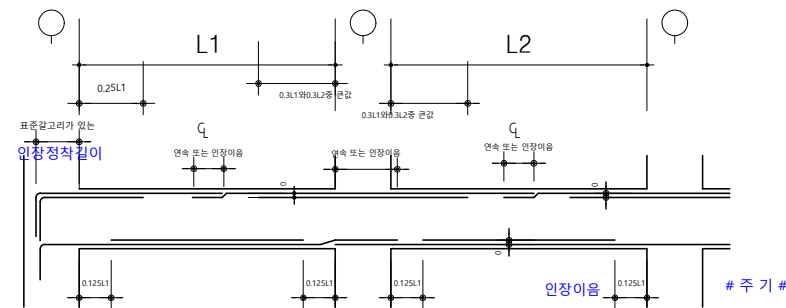

(2) 스티럽 배근

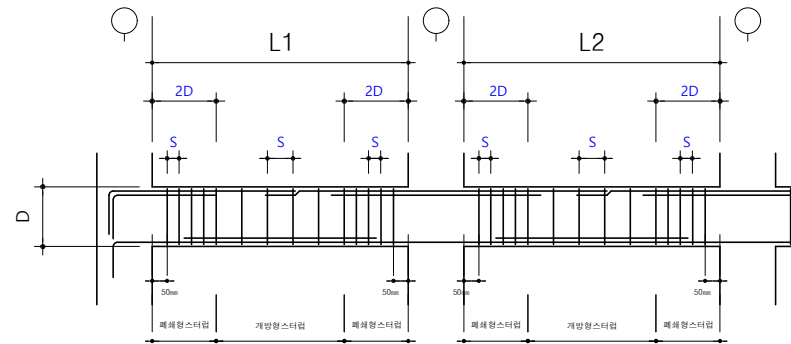

주 기


- 내진설계에서는 기둥면으로부터 부재 높이(D)의 2배에 해당하는 구간에는 폐쇄형 스티럽을 배근하여야 하며 스티럽의 간격은 (a) d/4, (b)주철근 직경의 8배, (c)스티럽 직경의 24배, (d) 30cm 중 최소값 이하로 한다. (단, 전이보는 전구간 폐쇄형 스티럽) (d = 보의 유효폭)
- 중양부 구간의 스티럽의 간격은 d/2이하로 배치하여야 한다 (단, 전이보는 제외)
- 테두리보의 경우 내진설계 유무와 관계없이 폐쇄형 스티럽을 사용한다.

3) 스티럽 상세


(1) 개방형 스티럽 : 덮개 철근(cap tie)이 필요 없는 보

비틀림의 영향이 없고 전단에 의하여 배근이 되는 보

내진설계 적용대상이 아닌 경우와, 내진설계시 보통 모멘트 골조인 경우

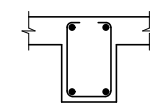


내부 90° 표준 갈고리

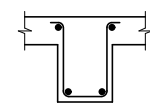


바깥 90° 표준 갈고리


(2) 폐쇄형 스티럽 : 전단과 비틀림을 동시에 받는 보, 테두리보

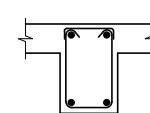


양쪽에 슬래브가 있는 보

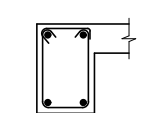


한쪽에 슬래브가 있는 보

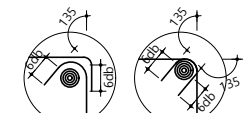

갈고리 상세

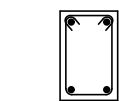


양쪽 모두 슬래브가 없는 보

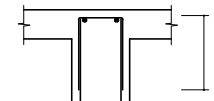

일반철근 이용길이 (8급 이용) 적용
춤이 깊은 보

(3) 후프철근 : 중간모멘트골조에서 보 단부배근 상세

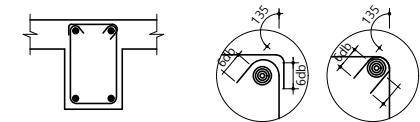

갈고리 상세

건축주 CLIENT NH농협은행 (강원본부)	설계사무소 DESIGN OFFICE 지안21 건축사무소 Tel. 02-6014-2137 / Fax. 02-6014-2138 Email : archjian21@naver.com	NOTE.	△				설계명 PROJECT TITLE NH농협은행 강원 금융센터 신축공사 협력설계 CONSULTANT 건축구조 : (주)탐앤지니어링 토목 : (주) 제일기초이엔씨 전기/통신/소방 : (주)하랑엔지니어링	프로젝트번호 PROJECT CODE JP25-0001	승인 APPROVED BY 황진희 00.00.00	도면명 DRAWING TITLE 내진배근상세도			
		△						전문분야 SUBJECT 건축	검토 CHECKED BY 최용규 00.00.00	축척 SCALE A1: NONE A3: NONE	도면번호 DRAWING NO. S21-006		
		△						설계단계 DESIGN PHASE 실시 설계(변경)	작성 Drawn By 신가영 00.00.00		밀련번호 SHEET NO. 000	REV. NO. △	
		No.	Date	Revision Description	Chkd.								