


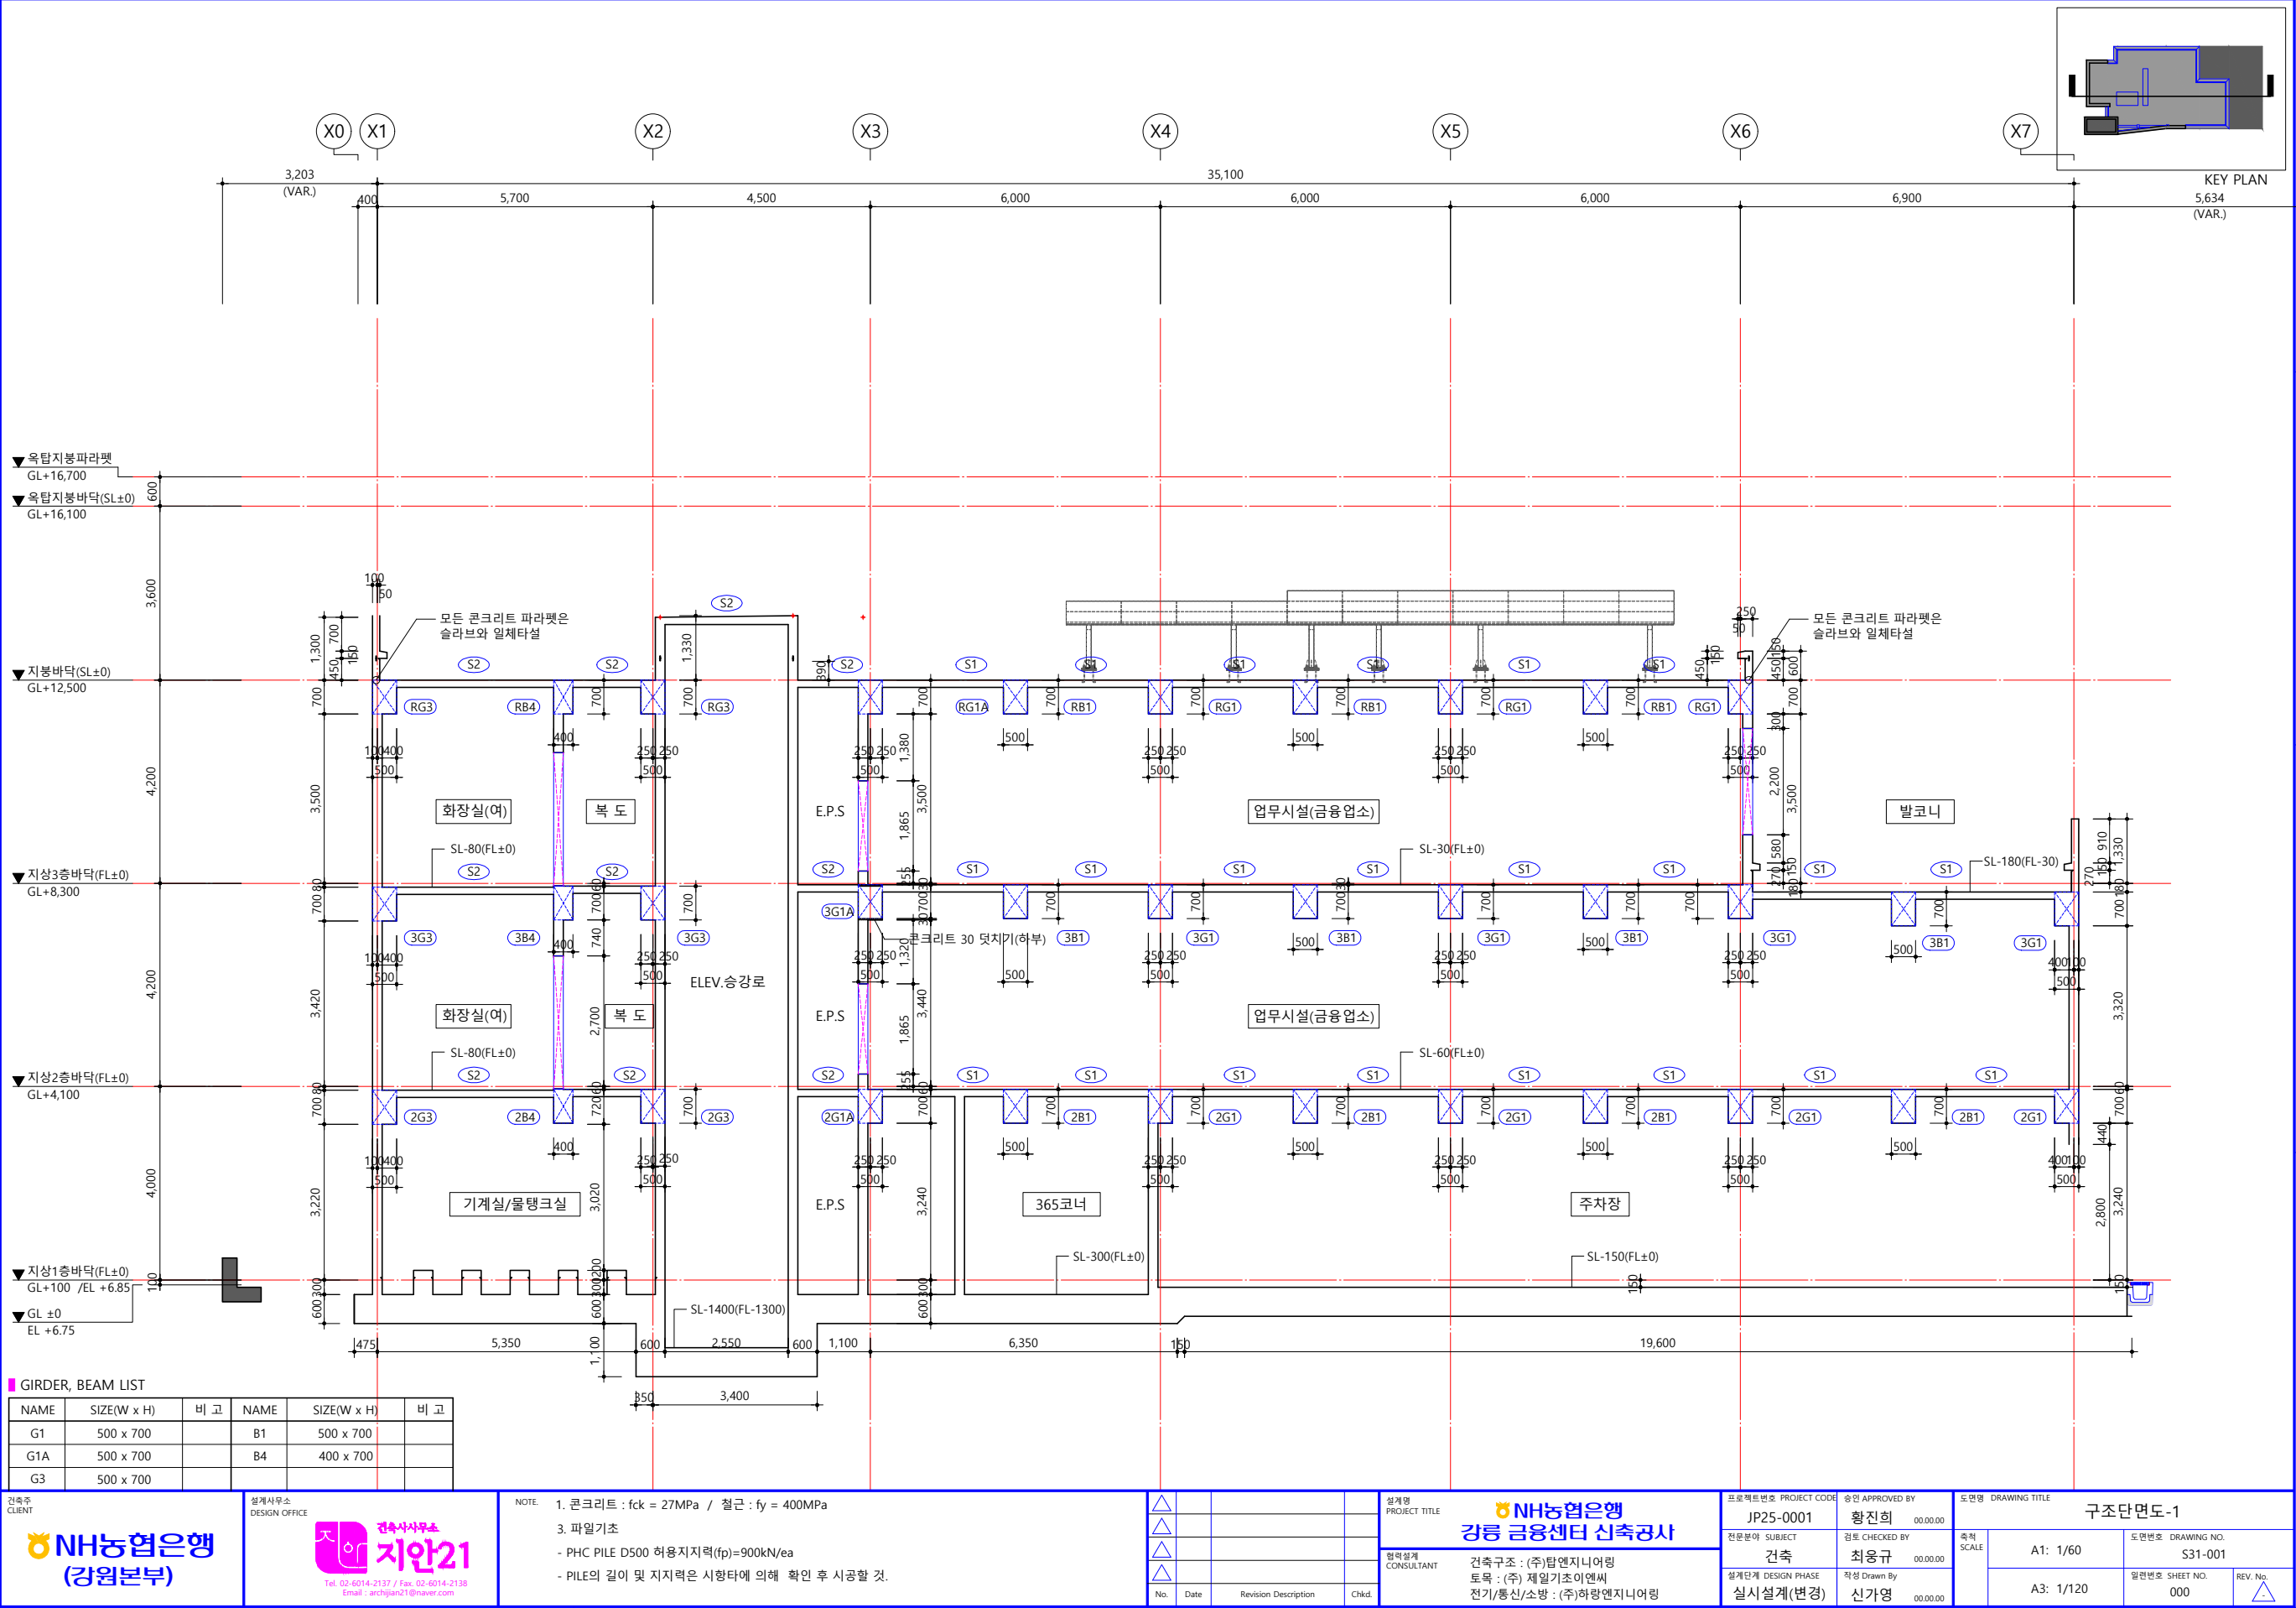

GIRDER, BEAM LIST

| NAME | SIZE(W x H) | 비 고 | NAME | SIZE(W x H) | 비 고 |
|------|-------------|-----|------|-------------|-----|
| G1   | 500 x 700   |     | B1   | 500 x 700   |     |
| G1A  | 500 x 700   |     | B4   | 400 x 700   |     |
| G3   | 500 x 700   |     |      |             |     |

건축주  
CLIENT

설계사무소  
DESIGN OFFICE

Tel. 02-6014-2137 / Fax. 02-6014-2138  
Email : archjian21@naver.com

NOTE.

1. 콘크리트 : fck = 27MPa / 철근 : fy = 400MPa  
3. 파일기초  
- PHC PILE D500 허용지지력(fp)=900kN/ea  
- PILE의 길이 및 지지력은 시향타에 의해 확인 후 시공할 것.

설계명  
PROJECT TITLE

설계단계  
CONSULTANT

건축구조 : (주)탐앤지니어링  
토목 : (주)제일기초이엔씨  
전기/통신/소방 : (주)하랑엔지니어링

프로젝트번호  
PROJECT CODE

JP25-0001

승인  
APPROVED BY

황진희 00.00.00

전문분야  
SUBJECT

건축

검토  
CHECKED BY

최용규 00.00.00

실시설계  
DESIGN PHASE

실시설계(변경)

작성  
Drawn By

신가영 00.00.00

도면명  
DRAWING TITLE

구조단면도-1


도면번호  
DRAWING NO.

S31-001


밀면번호  
SHEET NO.

000

REV. No.

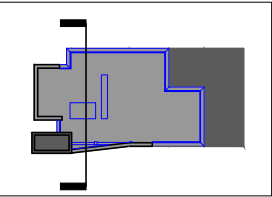

KEY PLAN

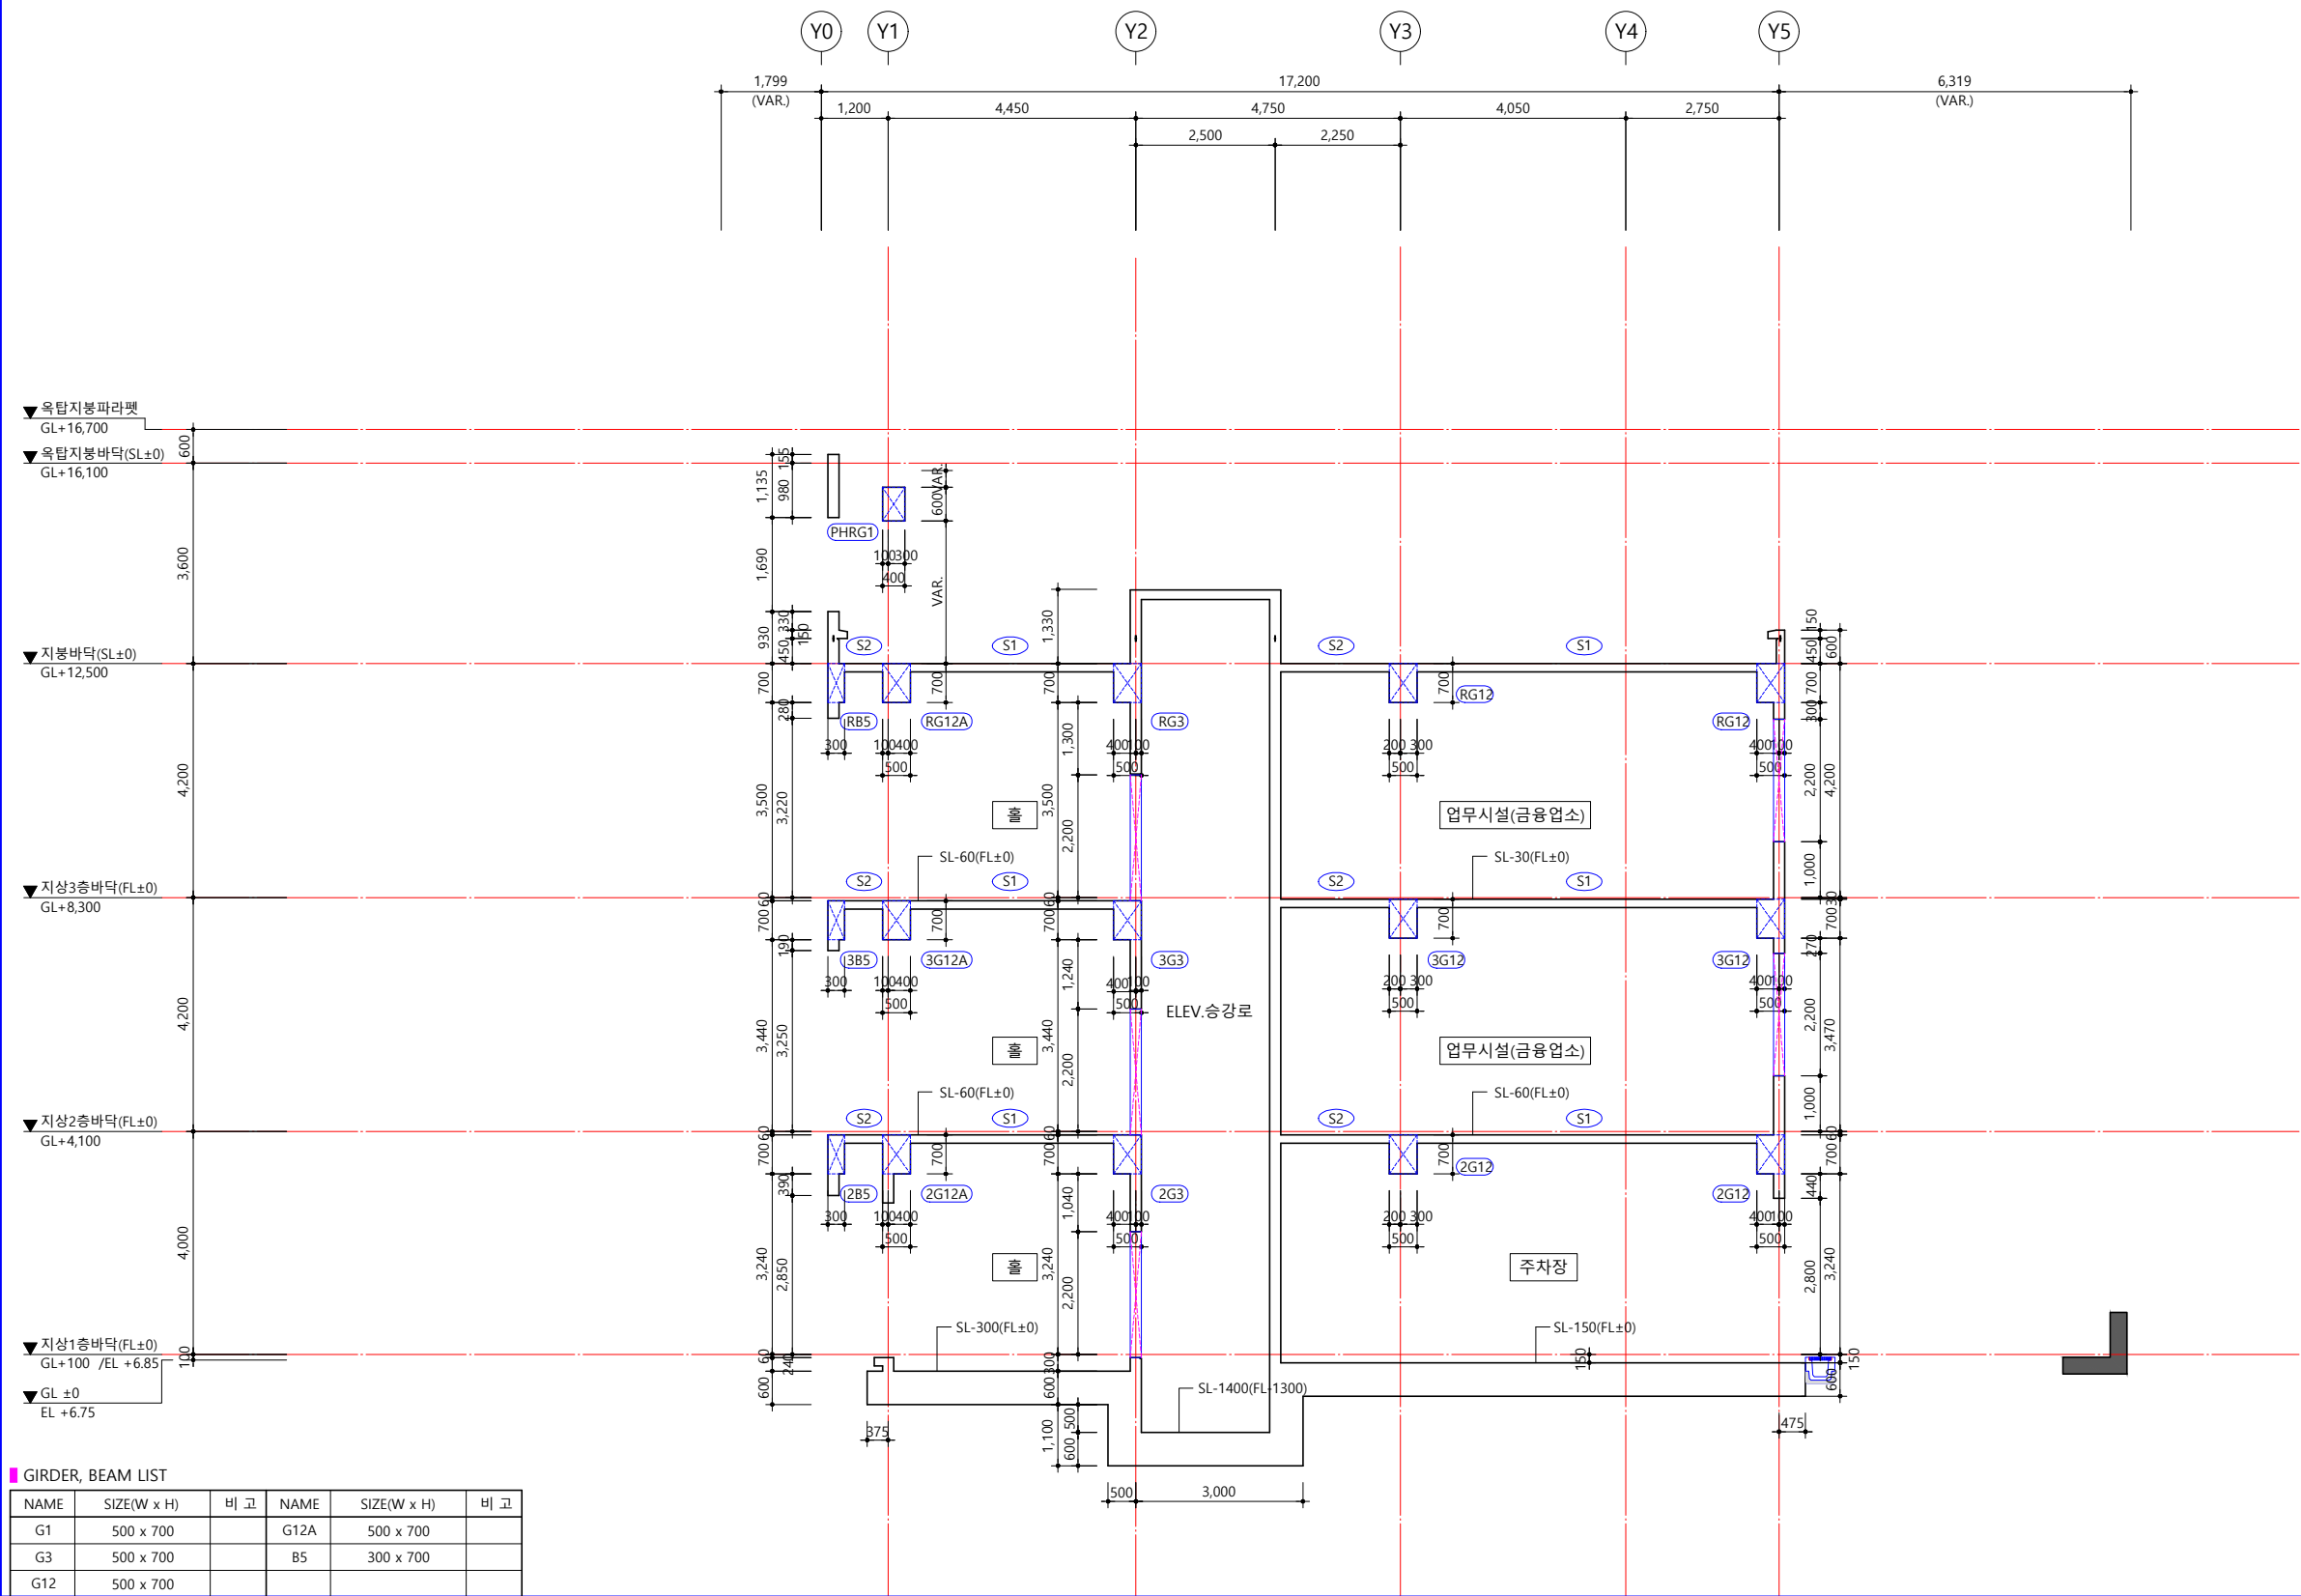

GIRDER, BEAM LIST

| NAME | SIZE(W x H) | 비 고 | NAME | SIZE(W x H) | 비 고 |
|------|-------------|-----|------|-------------|-----|
| G1   | 500 x 700   |     | G12A | 500 x 700   |     |
| G3   | 500 x 700   |     | B5   | 300 x 700   |     |
| G12  | 500 x 700   |     |      |             |     |

건축주  
CLIENT

설계사무소  
DESIGN OFFICE

Tel. 02-6014-2137 / Fax. 02-6014-2138  
Email : archjian21@naver.com

NOTE.

|     |      |                      |       |                      |                                |
|-----|------|----------------------|-------|----------------------|--------------------------------|
| △   |      |                      |       | 설계명<br>PROJECT TITLE | <b>NH농협은행<br/>강릉 금융센터 신축공사</b> |
| △   |      |                      |       | 영역<br>SUBJECT        | 건축                             |
| △   |      |                      |       | 설계단계<br>DESIGN PHASE | 실시설계(변경)                       |
| No. | Date | Revision Description | Chkd. | 승인<br>APPROVED BY    | 황진희 00.00.00                   |
|     |      |                      |       | 검토<br>CHECKED BY     | 최용규 00.00.00                   |
|     |      |                      |       | 작성<br>Drawn By       | 신가영 00.00.00                   |

프로젝트번호  
PROJECT CODE

JP25-0001

도면명  
DRAWING TITLE

구조단면도-2

도면번호  
DRAWING NO.


S31-002

밀면번호  
SHEET NO.

000

REV. No.

△

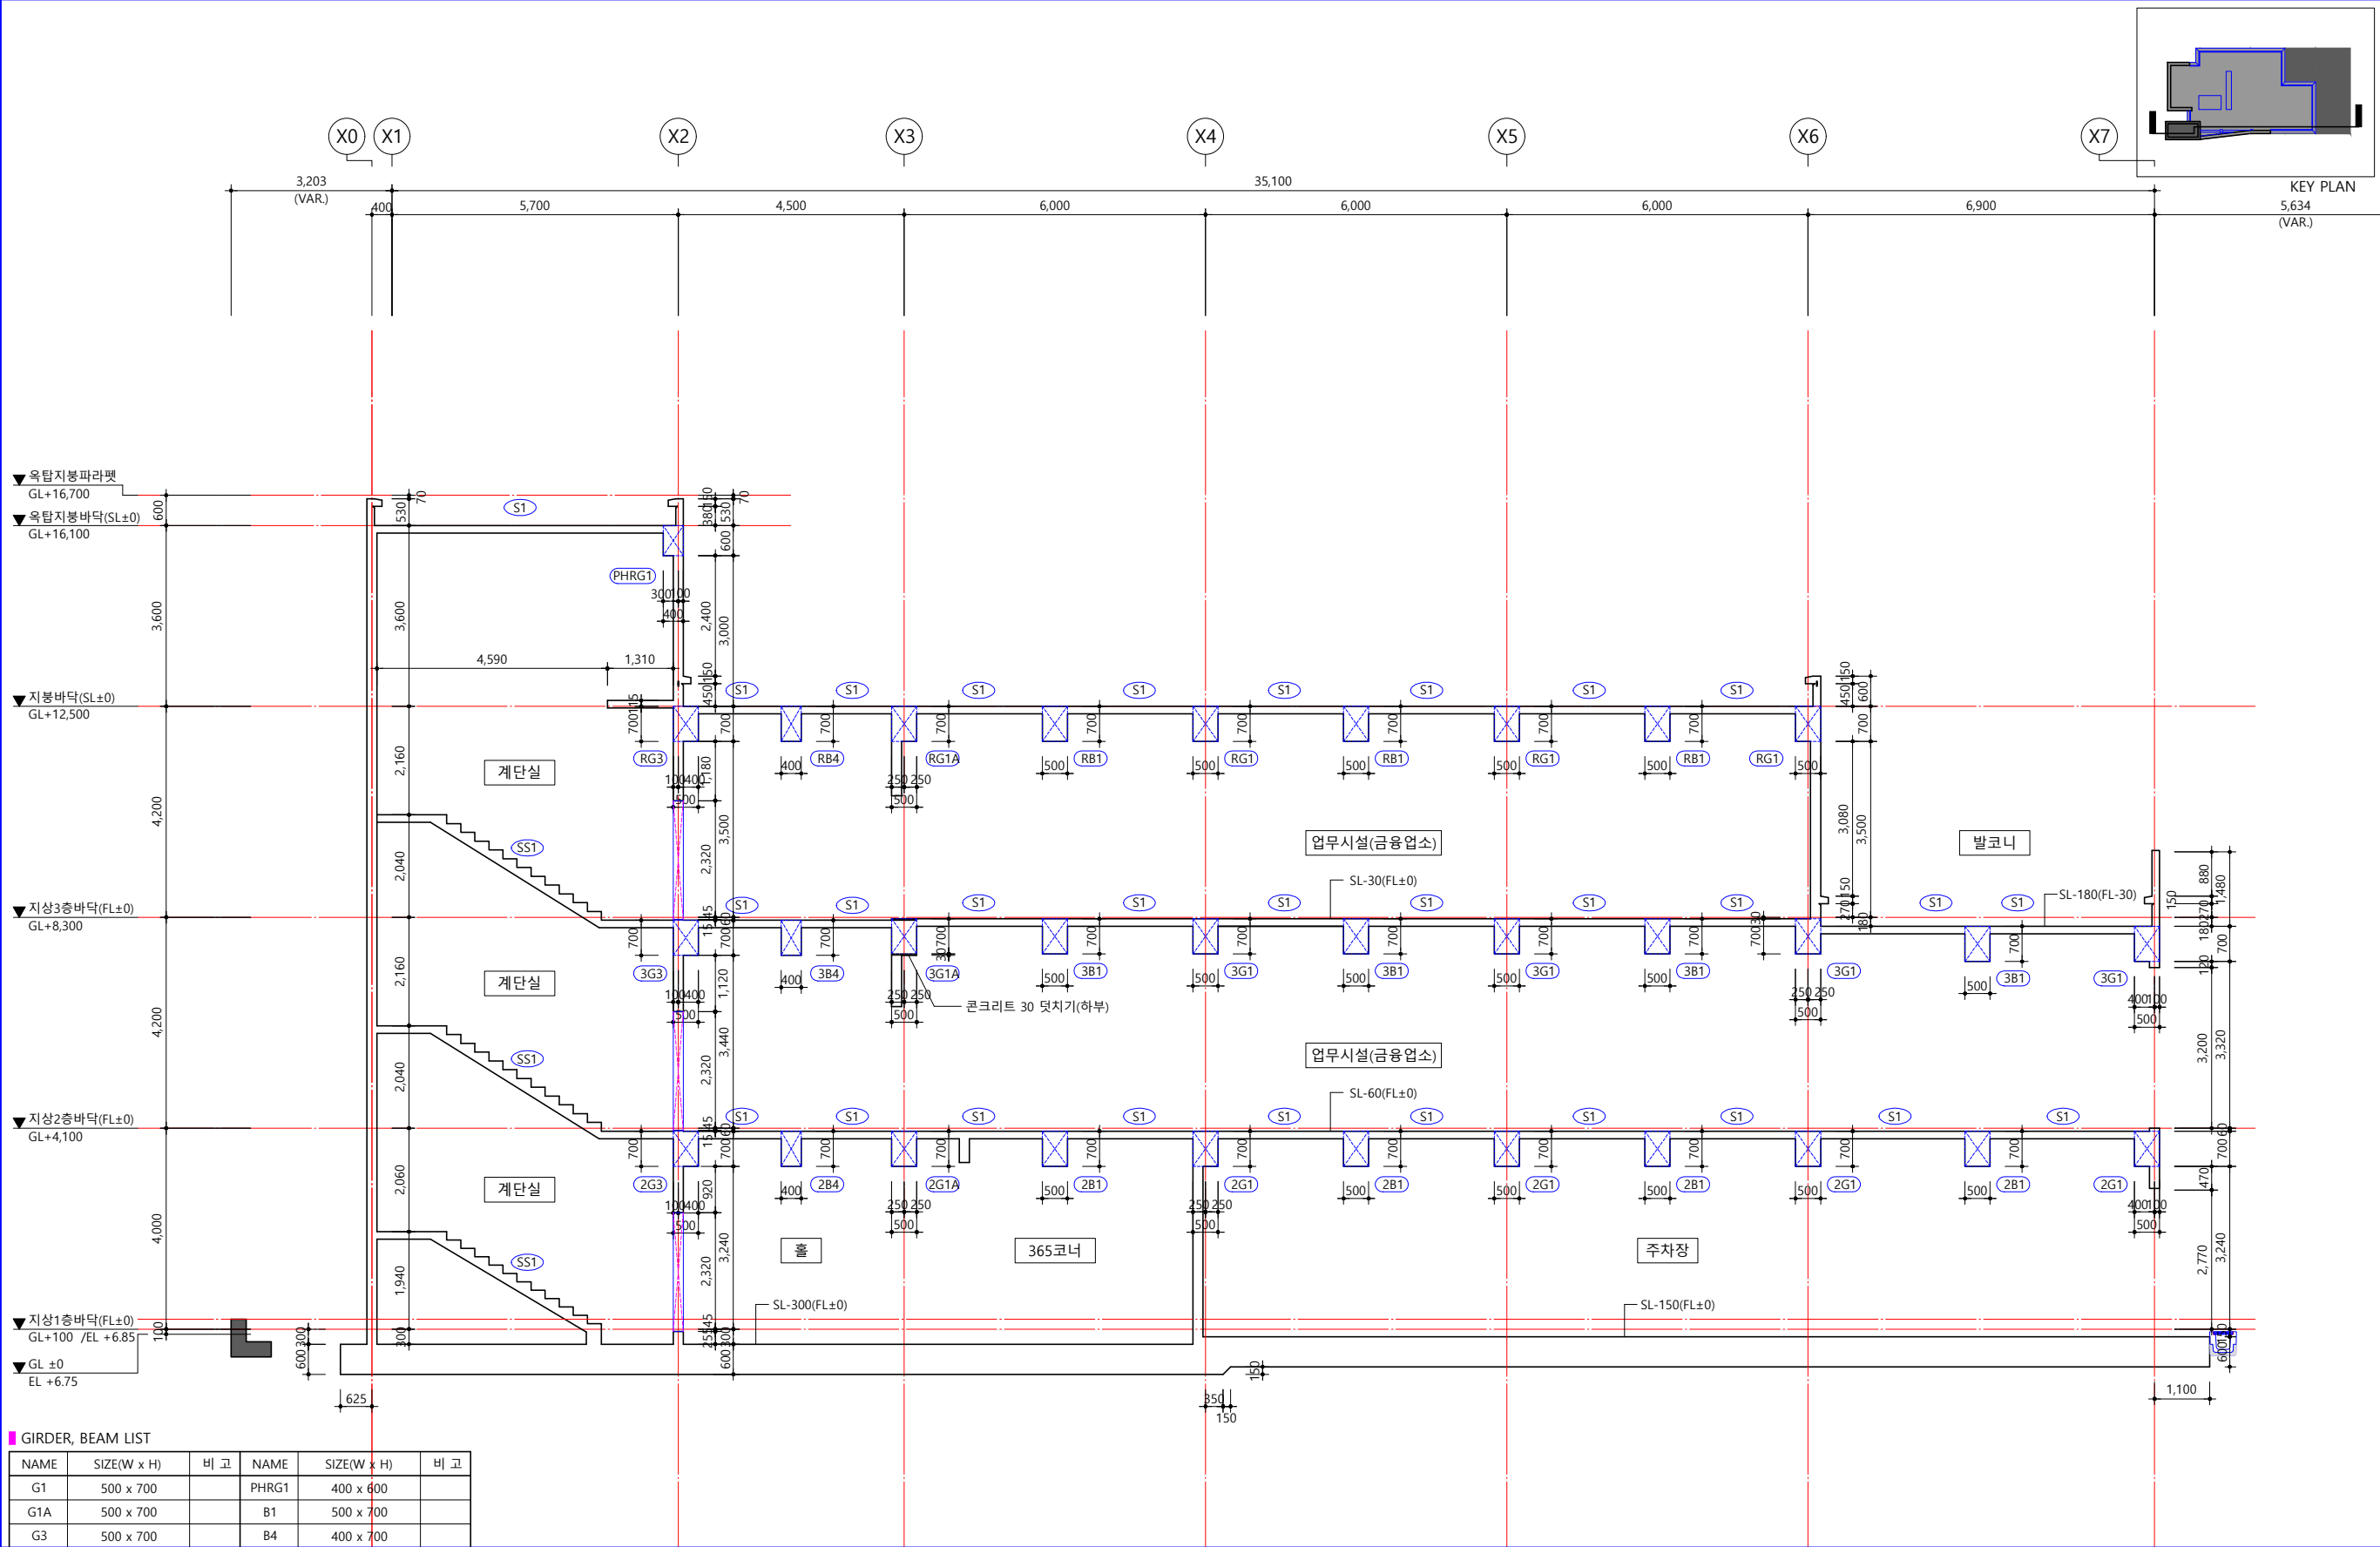

GIRDER, BEAM LIST

| NAME | SIZE(W x H) | 비 고 | NAME  | SIZE(W x H) | 비 고 |
|------|-------------|-----|-------|-------------|-----|
| G1   | 500 x 700   |     | PHRG1 | 400 x 600   |     |
| G1A  | 500 x 700   |     | B1    | 500 x 700   |     |
| G3   | 500 x 700   |     | B4    | 400 x 700   |     |

건축주  
CLIENT

설계사무소  
DESIGN OFFICE

Tel. 02-6014-2137 / Fax. 02-6014-2138  
Email : archjian21@naver.com

NOTE.

|     |      |                      |       |                        |                                                              |
|-----|------|----------------------|-------|------------------------|--------------------------------------------------------------|
| △   |      |                      |       | 설계명<br>PROJECT TITLE   | <br>강릉 금융센터 신축공사                                             |
| △   |      |                      |       | 전문분야<br>SUBJECT        | 건축                                                           |
| △   |      |                      |       | 협력설계<br>CONSULTANT     | 건축구조 : (주)탐앤지니어링<br>토목 : (주)제일기초이엔씨<br>전기/통신/소방 : (주)하랑엔지니어링 |
| No. | Date | Revision Description | Chkd. | 프로젝트번호<br>PROJECT CODE | JP25-0001                                                    |

승인  
APPROVED BY

00.00.00

황진희

검토  
CHECKED BY

00.00.00

최용규

작성  
Drawn By

00.00.00

신가영

실시설계(변경)

도면명  
DRAWING TITLE

구조단면도-3

축척  
SCALE

A1: 1/60  
A3: 1/120

도면번호  
DRAWING NO.


S31-003

밀면번호  
SHEET NO.


000

REV. No.

△

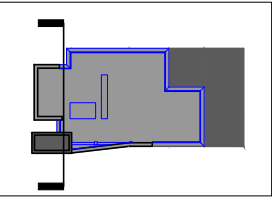

KEY PLAN

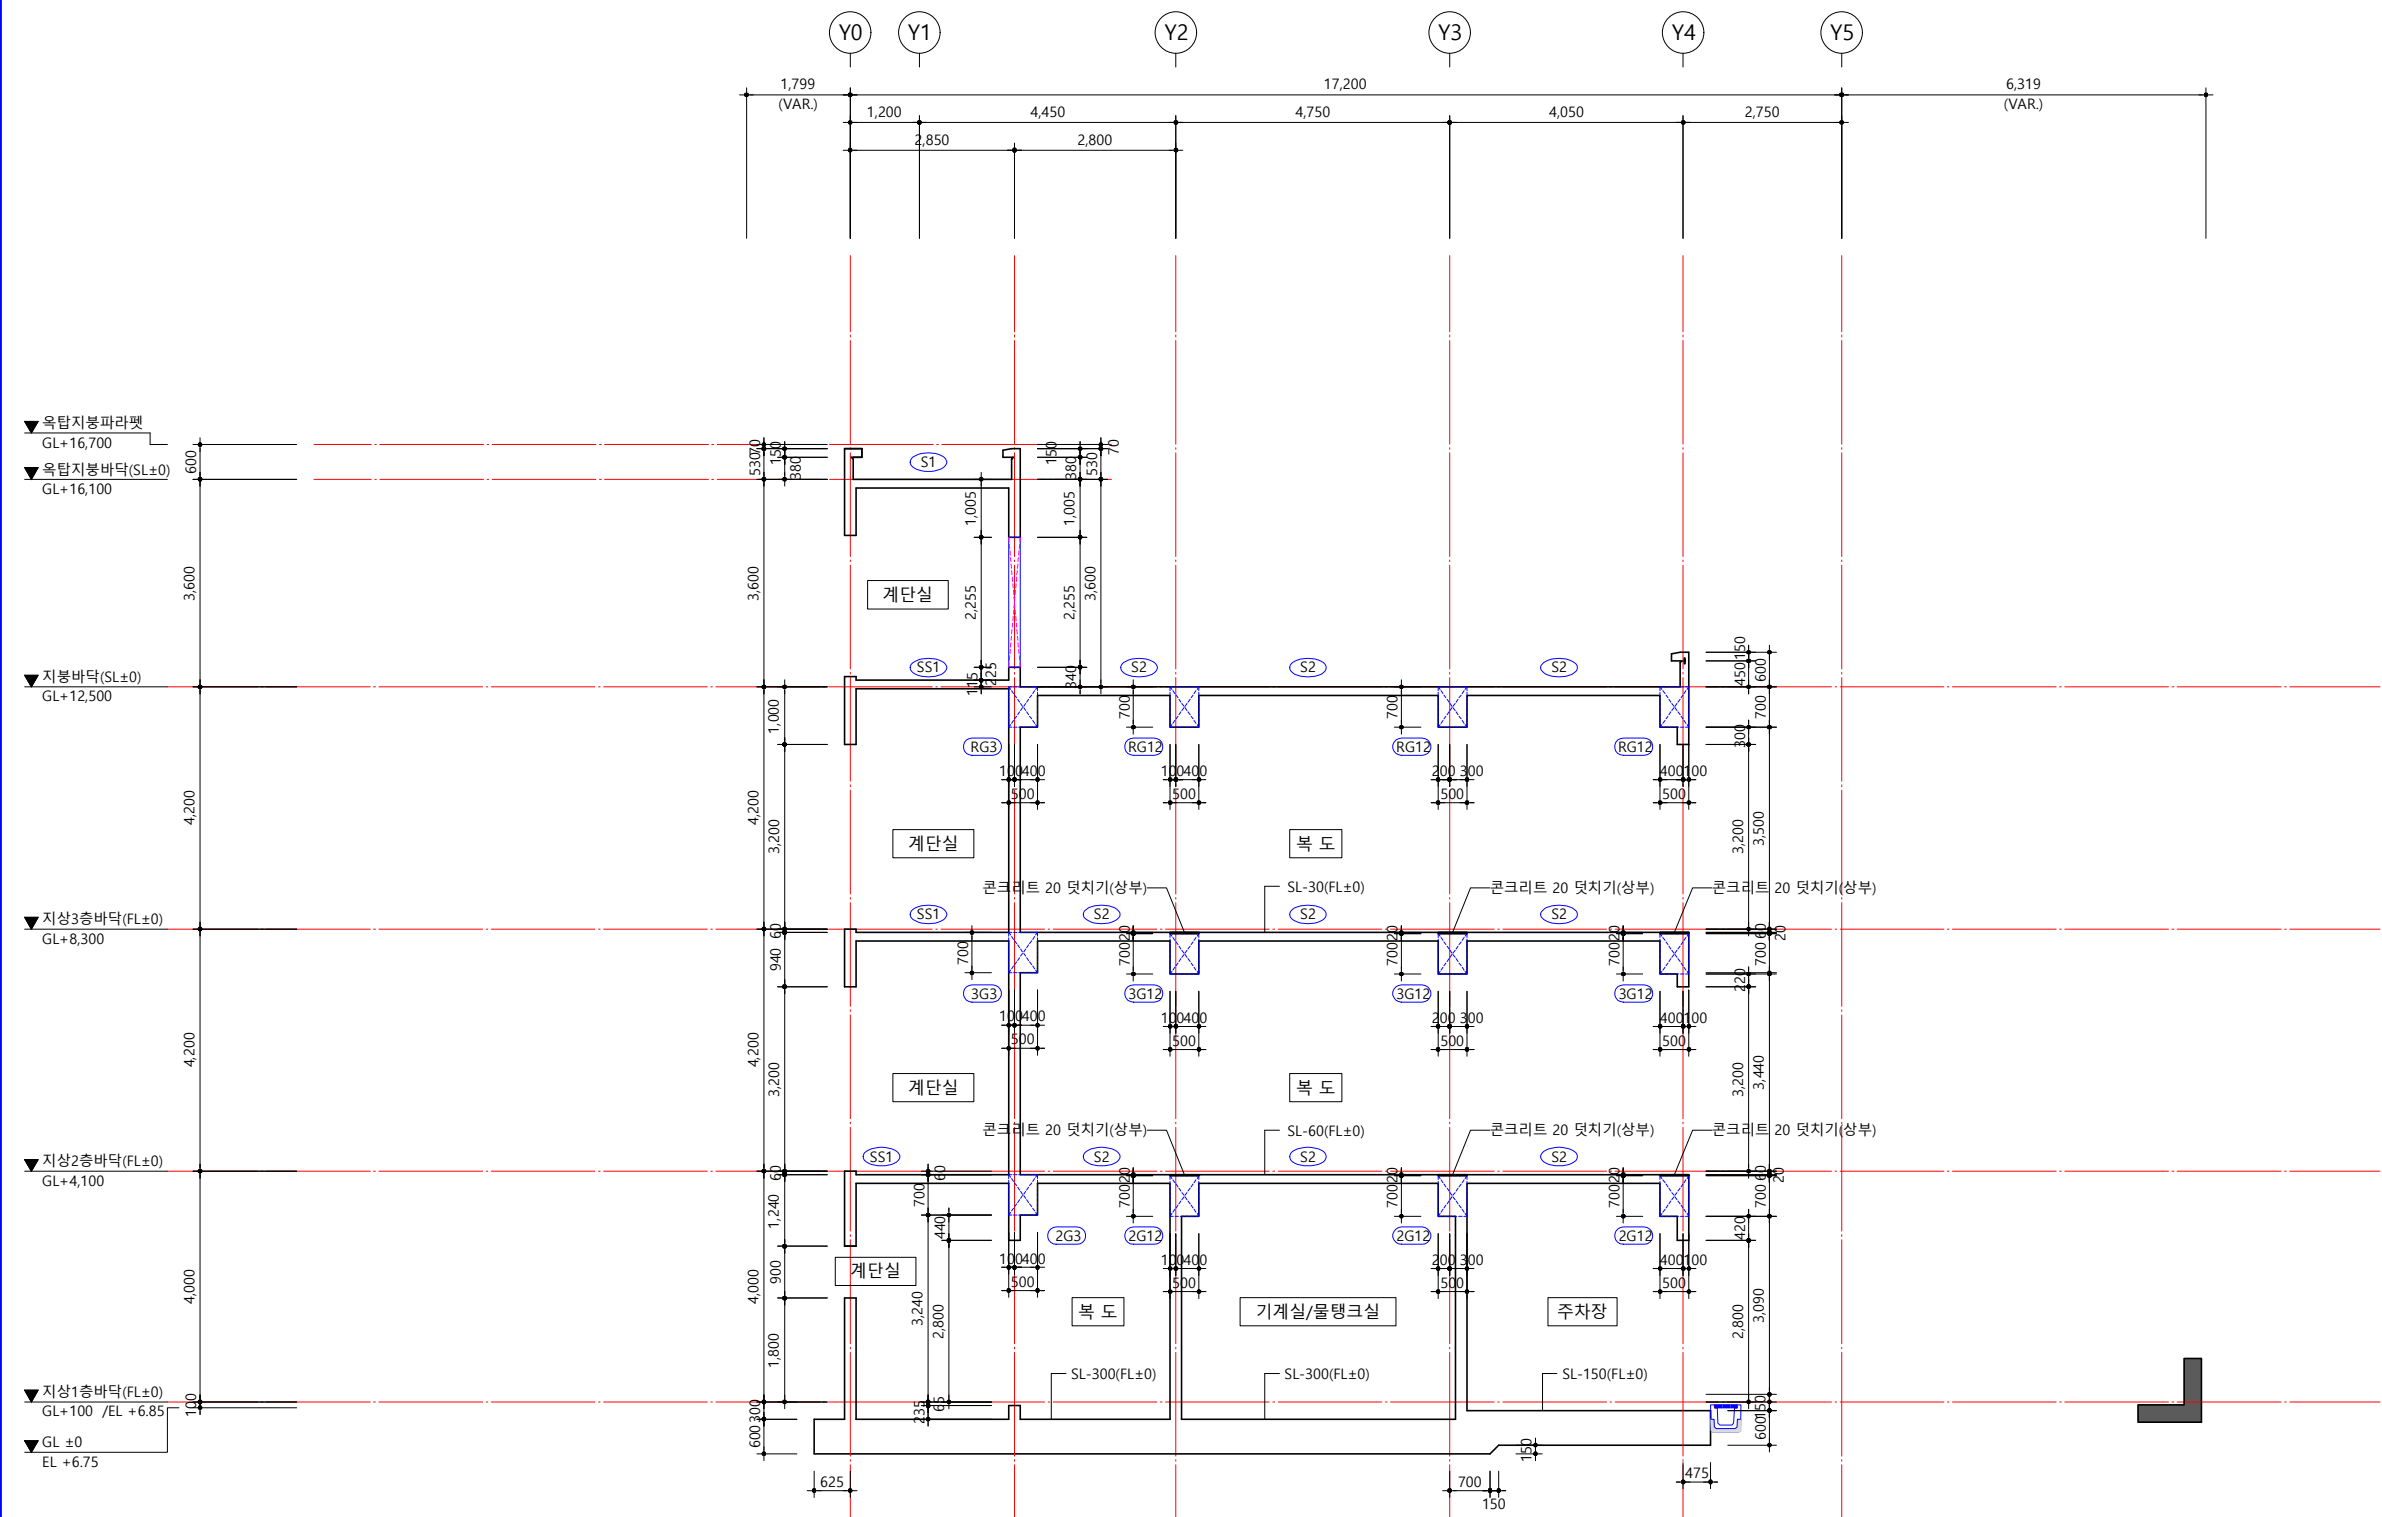

GIRDER, BEAM LIST

| NAME | SIZE(W x H) | 비 고 | NAME | SIZE(W x H) | 비 고 |
|------|-------------|-----|------|-------------|-----|
| G3   | 500 x 700   |     |      |             |     |
| G12  | 500 x 700   |     |      |             |     |

건축주  
CLIENT


설계사무소  
DESIGN OFFICE

Tel. 02-6014-2137 / Fax. 02-6014-2138  
Email : archjian21@naver.com


NOTE.

|   |  |  |  |                      |                                                              |
|---|--|--|--|----------------------|--------------------------------------------------------------|
| △ |  |  |  | 설계명<br>PROJECT TITLE | <b>NH농협은행<br/>강릉 금융센터 신축공사</b>                               |
| △ |  |  |  | 영역 설계<br>CONSULTANT  | 건축구조 : (주)탐앤지니어링<br>토목 : (주)제일기조이엔씨<br>전기/통신/소방 : (주)하랑엔지니어링 |
| △ |  |  |  | No.                  | Date                                                         |
| △ |  |  |  | Revision Description | Chkd.                                                        |

|                        |           |                   |                 |                      |           |                     |
|------------------------|-----------|-------------------|-----------------|----------------------|-----------|---------------------|
| 프로젝트번호<br>PROJECT CODE | JP25-0001 | 승인<br>APPROVED BY | 황진희<br>00.00.00 | 도면명<br>DRAWING TITLE | 구조단면도-4   |                     |
| 전문분야<br>SUBJECT        | 건축        | 검토<br>CHECKED BY  | 최용규<br>00.00.00 | 축척<br>SCALE          | A1: 1/60  | 도면번호<br>DRAWING NO. |
| 설계단계<br>DESIGN PHASE   | 실시설계(변경)  | 작성<br>Drawn By    | 신가영<br>00.00.00 |                      | A3: 1/120 | 도면번호<br>DRAWING NO. |
|                        |           |                   |                 |                      |           | S31-004             |
|                        |           |                   |                 |                      |           | 일련번호<br>SHEET NO.   |
|                        |           |                   |                 |                      |           | 000                 |
|                        |           |                   |                 |                      |           | REV. No.            |
|                        |           |                   |                 |                      |           | △                   |

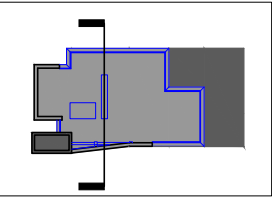

KEY PLAN

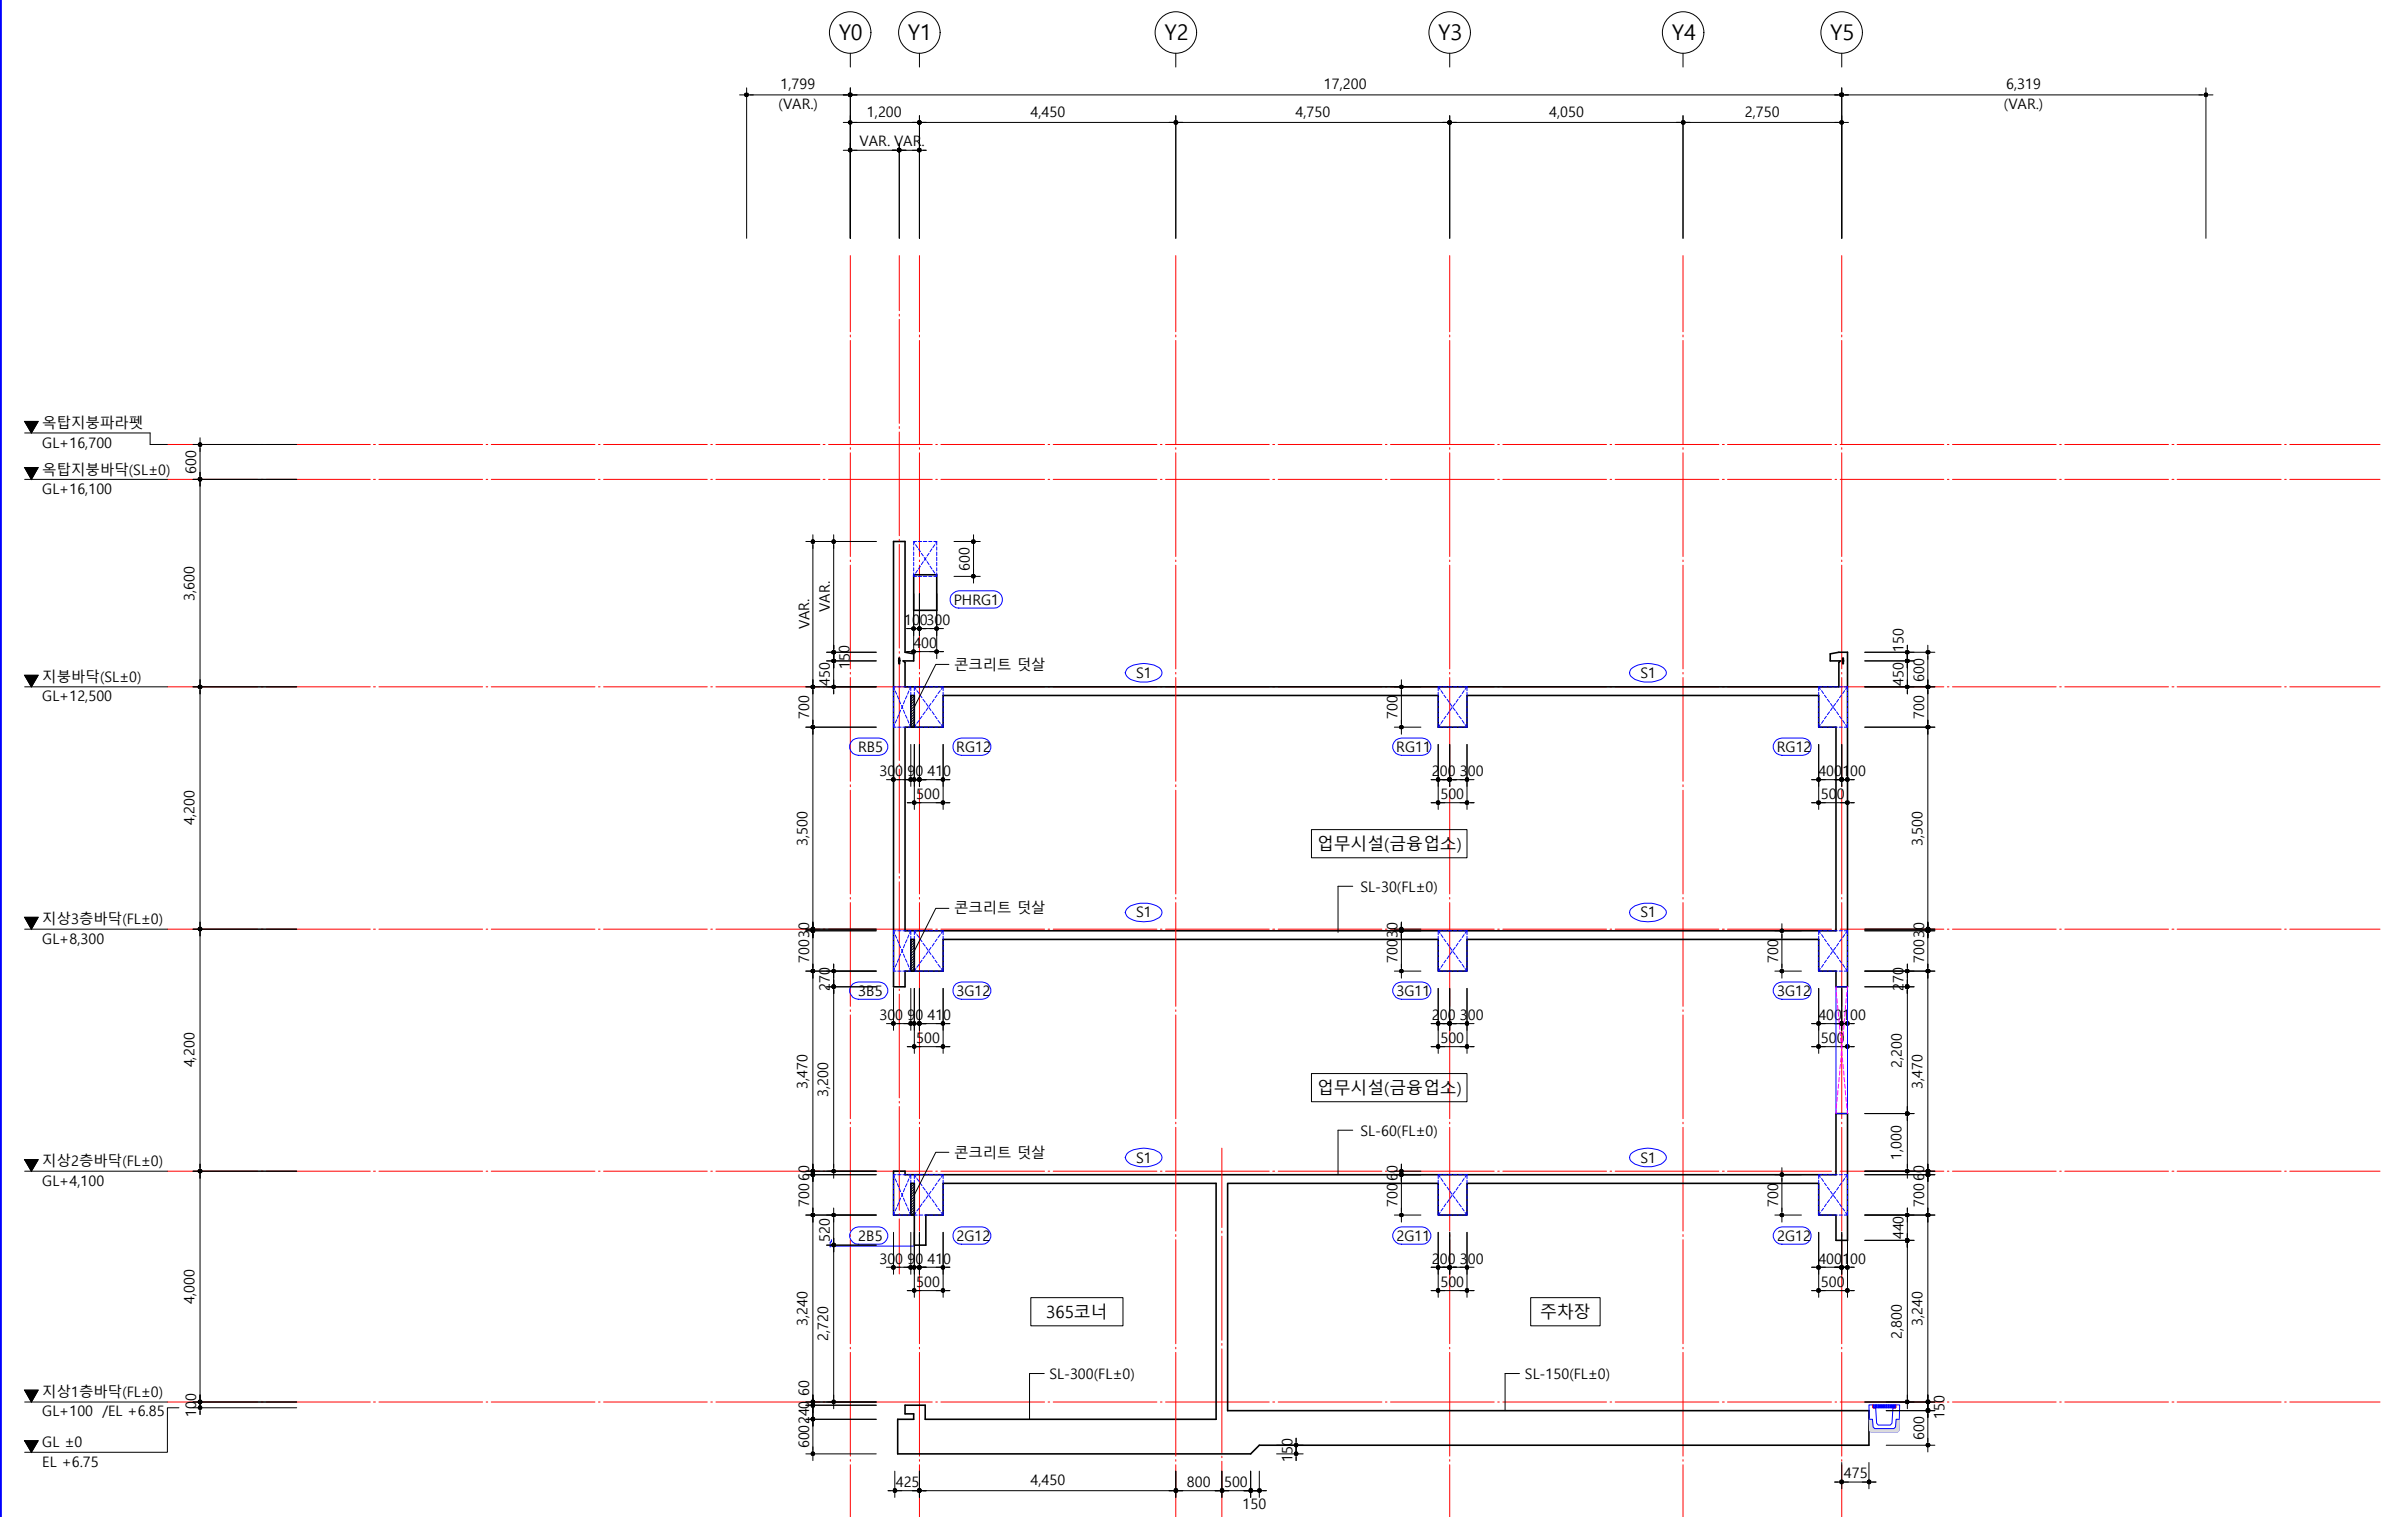

GIRDER, BEAM LIST

| NAME  | SIZE(W x H) | 비 고 | NAME | SIZE(W x H) | 비 고 |
|-------|-------------|-----|------|-------------|-----|
| G11   | 500 x 700   |     | B5   | 300 x 700   |     |
| G12   | 500 x 700   |     |      |             |     |
| PHRG1 | 400 x 600   |     |      |             |     |

건축주  
CLIENT

설계사무소  
DESIGN OFFICE

Tel. 02-6014-2137 / Fax. 02-6014-2138  
Email : archjian21@naver.com

NOTE.

|     |      |                      |       |  |
|-----|------|----------------------|-------|--|
| △   |      |                      |       |  |
| △   |      |                      |       |  |
| △   |      |                      |       |  |
| △   |      |                      |       |  |
| No. | Date | Revision Description | Chkd. |  |

설계명  
PROJECT TITLE

설계  
CONSULTANT

건축구조 : (주)탐앤지니어링  
토목 : (주) 제일기초이엔씨  
전기/통신/소방 : (주)하랑엔지니어링

프로젝트번호 PROJECT CODE

JP25-0001

승인 APPROVED BY

황진희 00.00.00

전문분야 SUBJECT

건축

검토 CHECKED BY

최용규 00.00.00

설계단계 DESIGN PHASE

실시설계(변경)

작성 Drawn By

신가영 00.00.00

도면명 DRAWING TITLE

구조단면도-5

도면번호 DRAWING NO.

S31-005

출력 SCALE


A1: 1/60  
A3: 1/120

도면번호 SHEET NO.


000

REV. No.

△

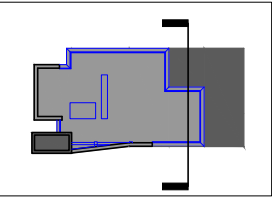

KEY PLAN

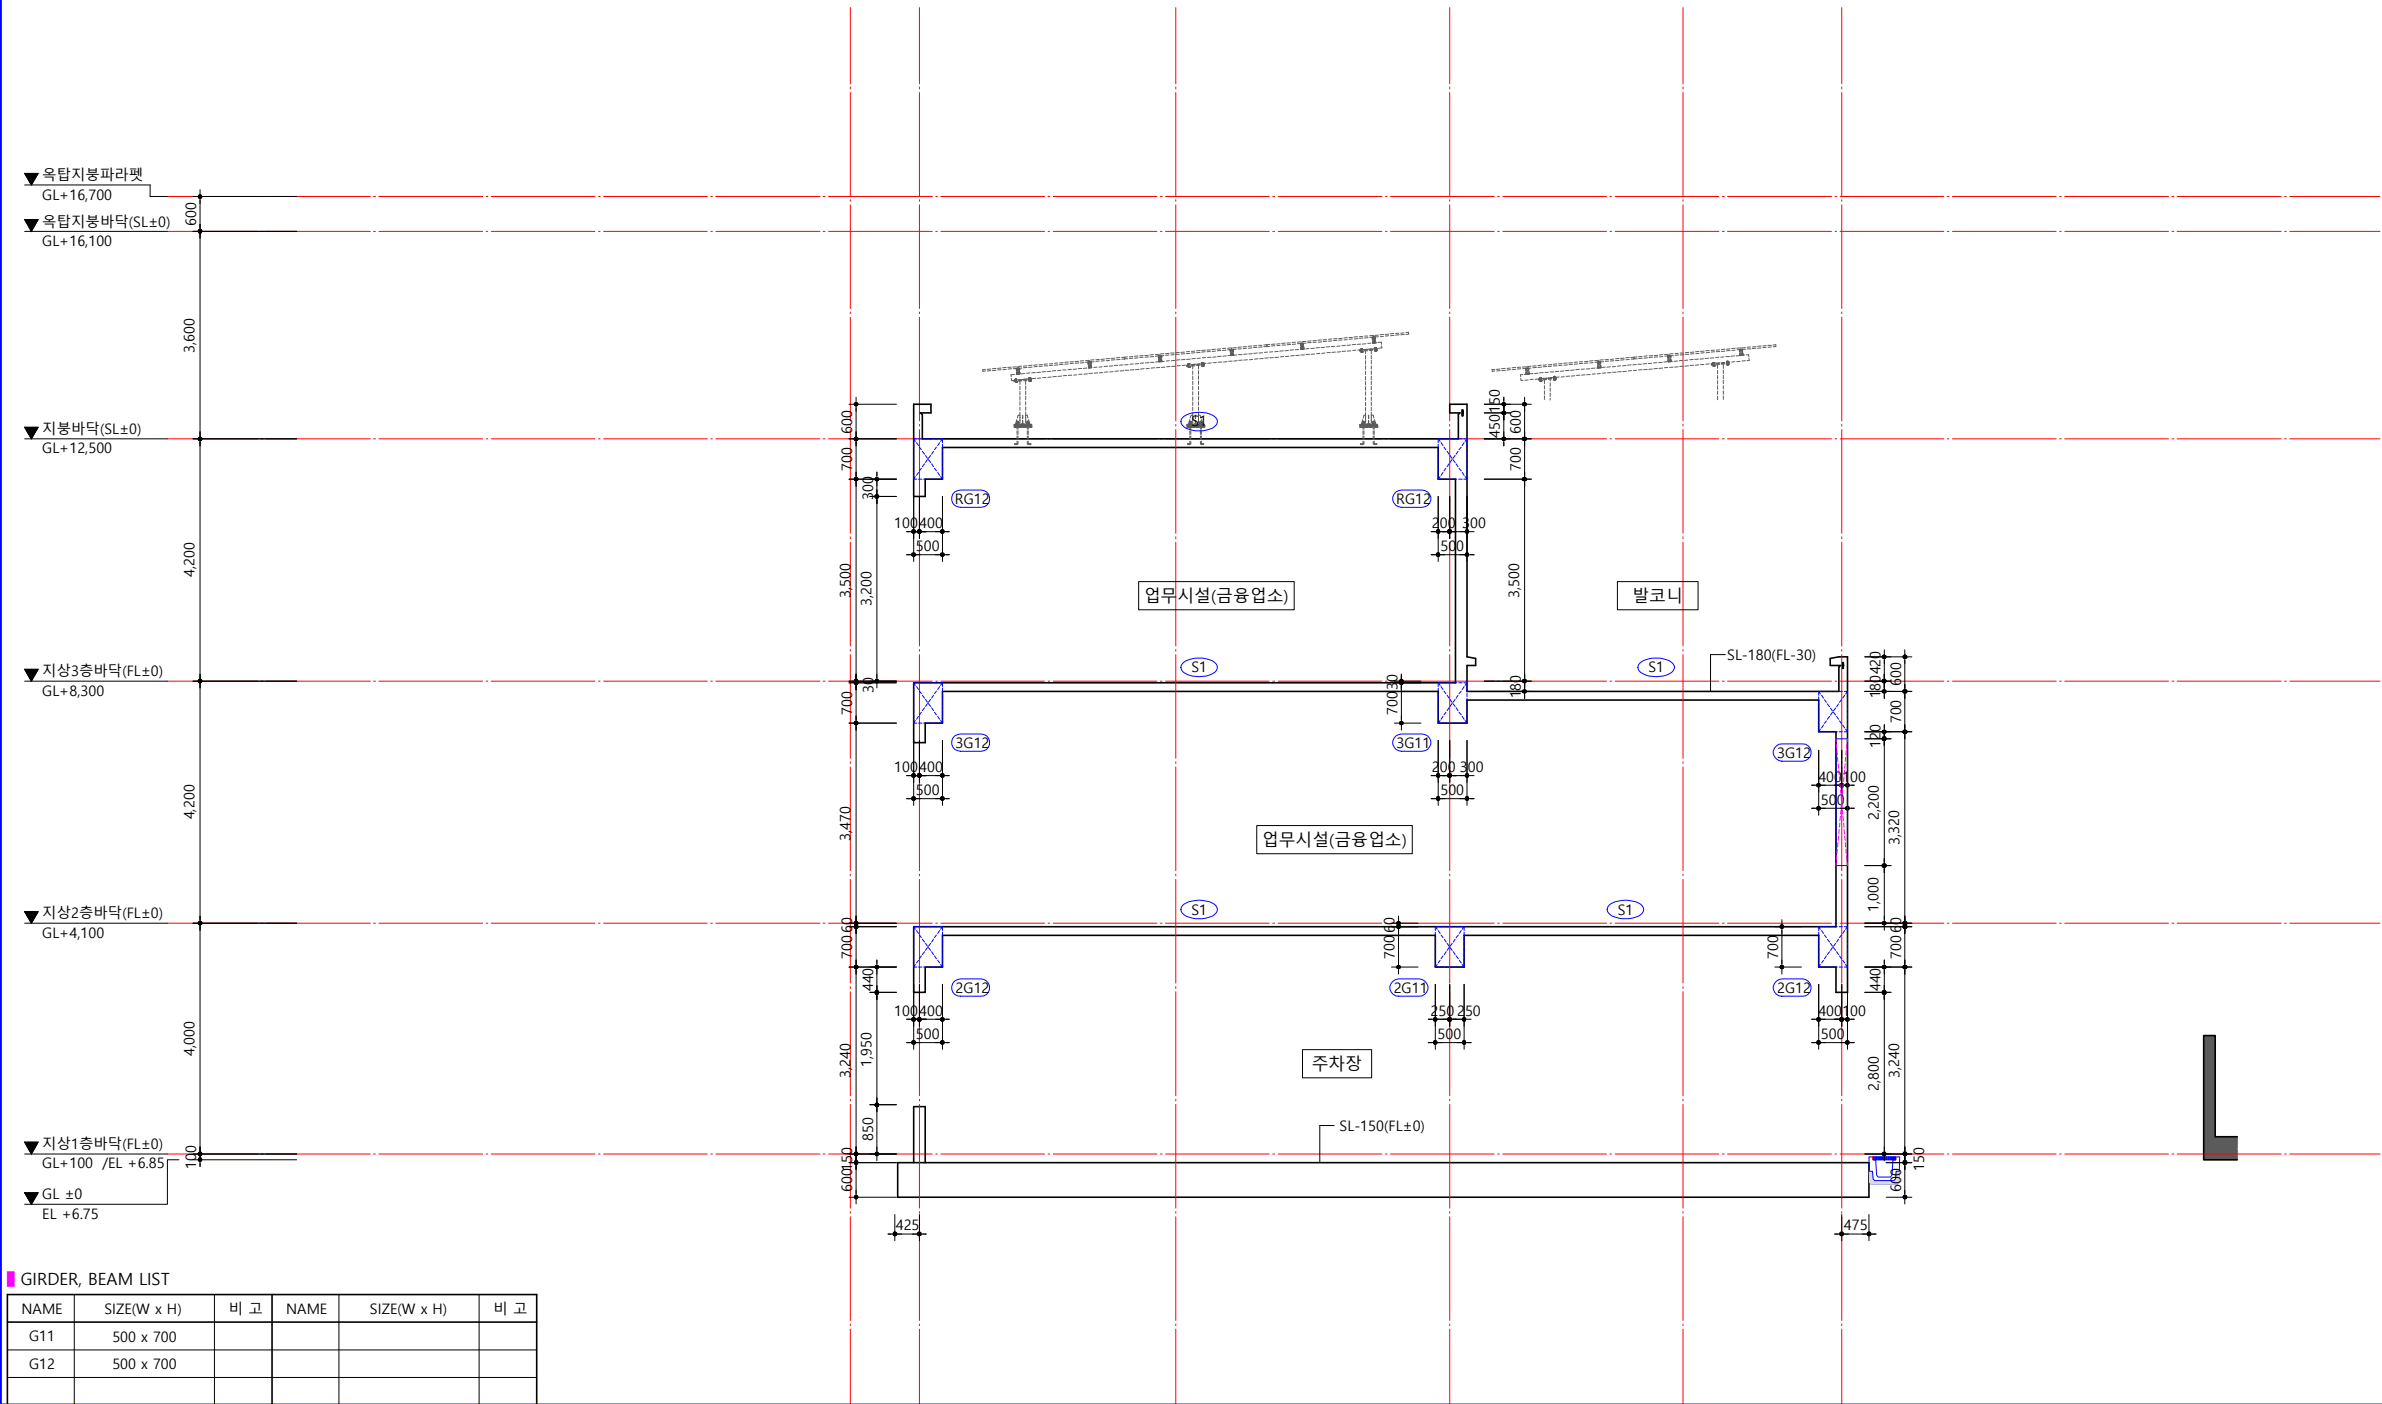

■ GIRDER, BEAM LIST

| NAME | SIZE(W x H) | 비고 | NAME | SIZE(W x H) | 비고 |
|------|-------------|----|------|-------------|----|
| G11  | 500 x 700   |    |      |             |    |
| G12  | 500 x 700   |    |      |             |    |

건축주  
CLIENT

설계사무소  
DESIGN OFFICE

Tel. 02-6014-2137 / Fax. 02-6014-2138  
Email : archjian21@naver.com

NOTE.

|     |      |                      |       |  |  |
|-----|------|----------------------|-------|--|--|
| △   |      |                      |       |  |  |
| △   |      |                      |       |  |  |
| △   |      |                      |       |  |  |
| △   |      |                      |       |  |  |
| No. | Date | Revision Description | Chkd. |  |  |

설계명  
PROJECT TITLE

설계단계  
CONSULTANT

건축구조 : (주)탐앤지니어링  
토목 : (주)제일기초이엔씨  
전기/통신/소방 : (주)하랑엔지니어링

프로젝트번호 PROJECT CODE

JP25-0001

설계단계 DESIGN PHASE

실시설계(변경)

승인 APPROVED BY

황진희 00.00.00

검토 CHECKED BY

최용규 00.00.00

작성 Drawn By

신가영 00.00.00

도면명 DRAWING TITLE

구조단면도-6

도면번호 DRAWING NO.

S31-006

출력 SCALE

A1: 1/60  
A3: 1/120

일련번호 SHEET NO.

000

REV. No.

△